



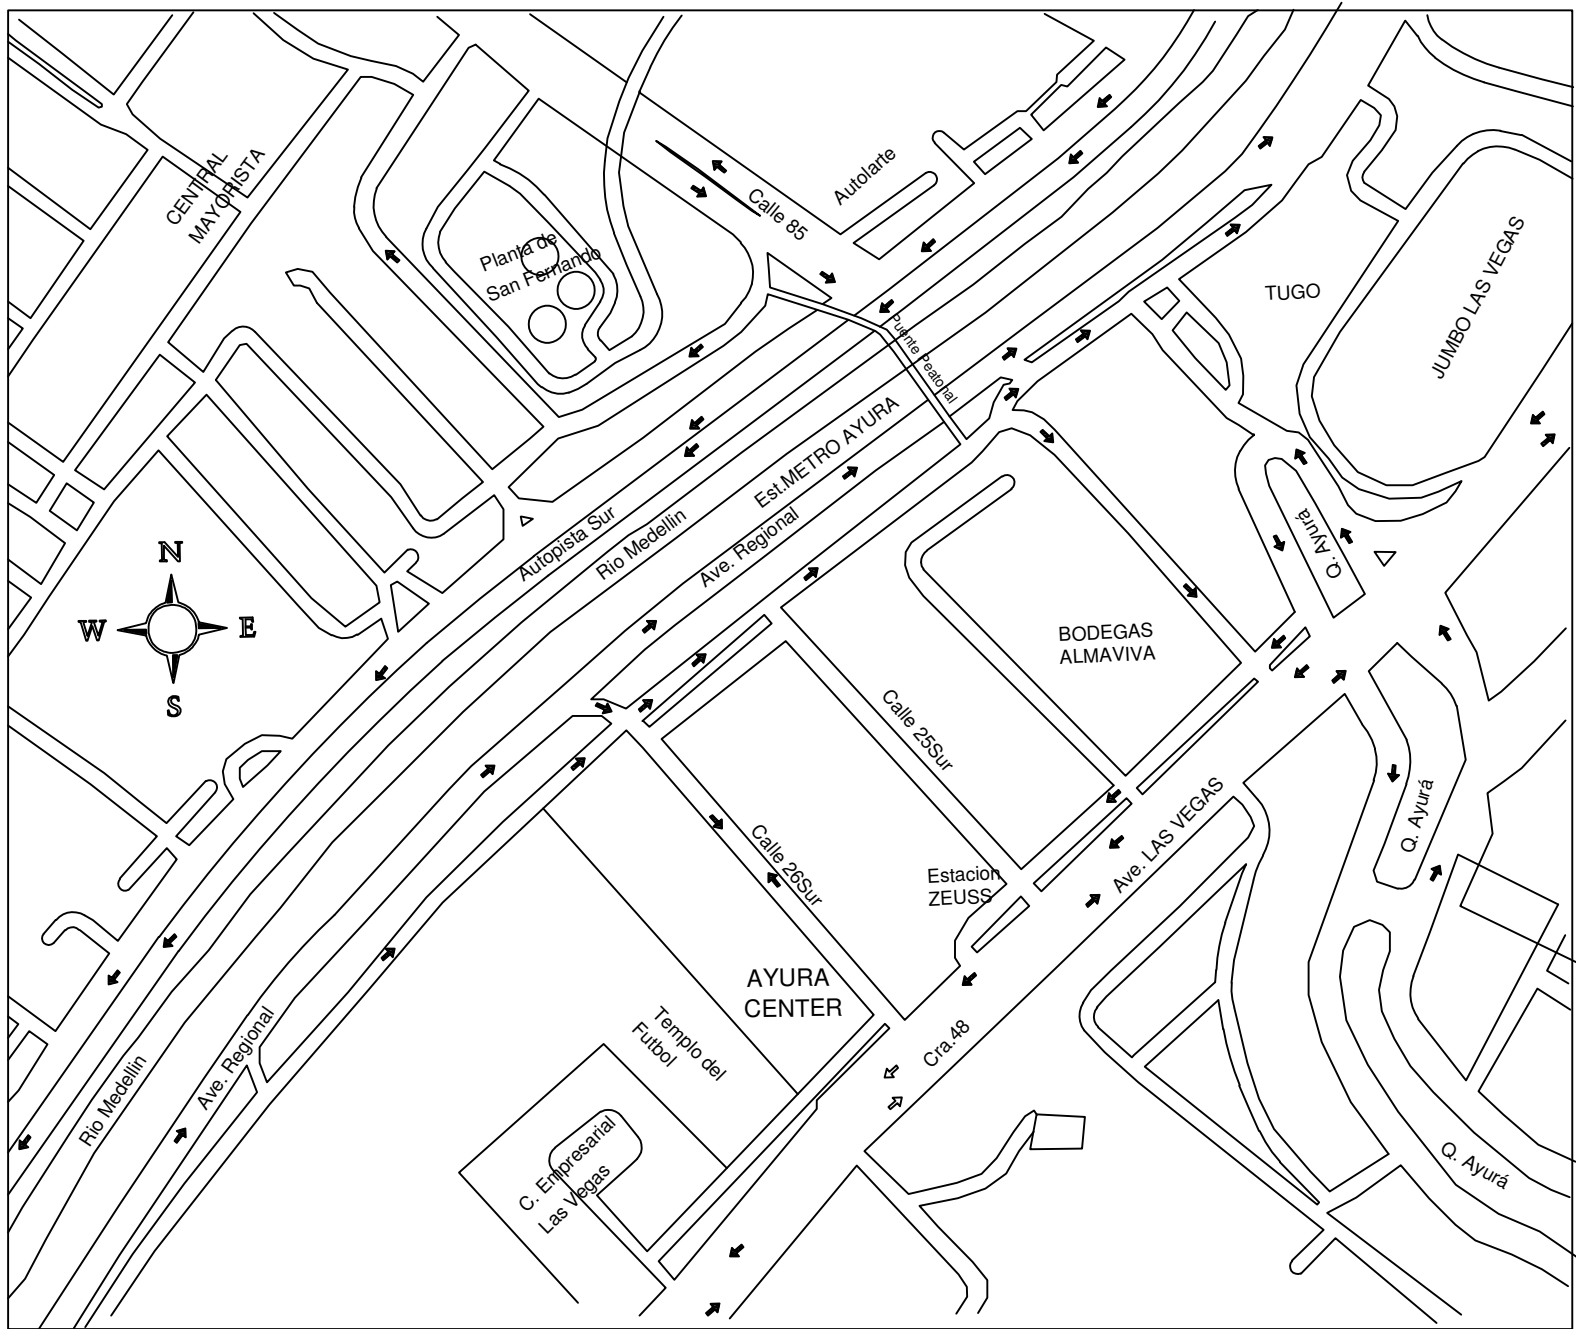

LOCALIZACIÓN GENERAL DEL PROYECTO

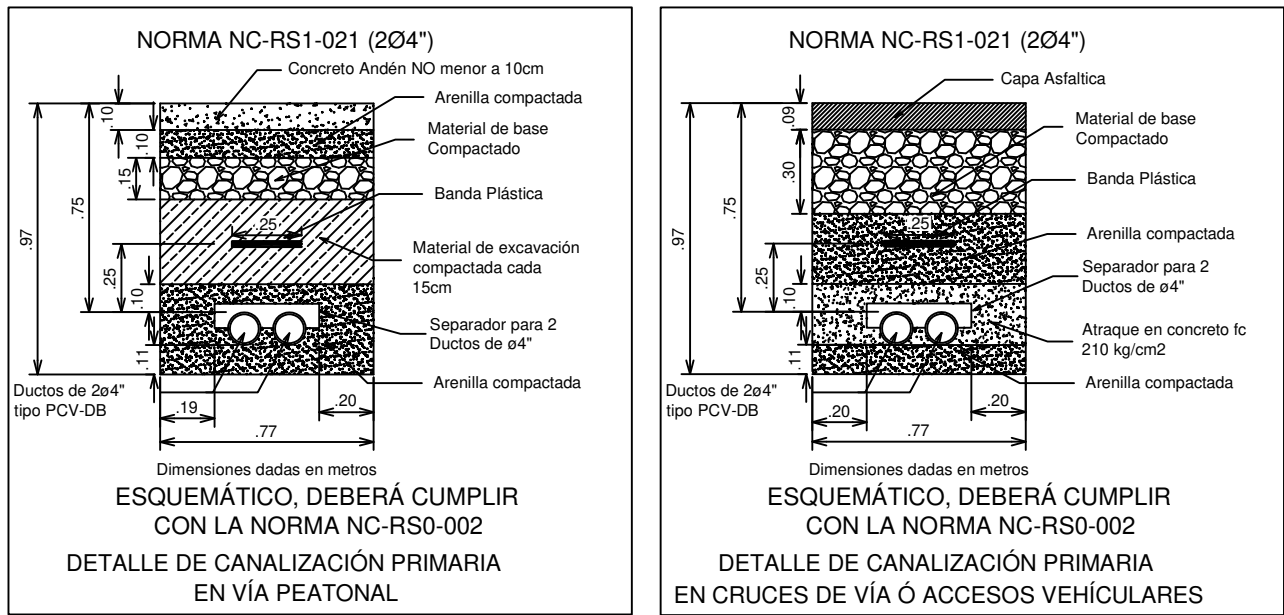

CONVENCIONES

EXISTENTE	PROYECTADO	DESCRIPCION
		LINEA PRIMARIA AREA DESGUDA
		CABLE PRIMARIO SUBTERRANEO
		CONDUCTOR SECUNDARIO SUBTERRANEO
		POSTO DE CONCRETO DE 12m
		CAJA DE DISTRIBUCION SELLADA Y MARCADA
		GABINETE SECUNDARIO - TABLERO ML
		TRANSFORMADOR TRIFASICO
		MEDIDOR ELECTRONICO MULTIFUNCIONAL 2.510A, 3x1/207.7V, 3F, 4H, de ENERGIA ACTIVA con indice de Clase 0.5S, y de ENERGIA REACTIVA con indice de Clase 2 con perfil de carga y medida de energia en cuatro cuadrantes
		MEDIDOR ELECTRONICO MULTIFUNCIONAL 2.510A, 3x1/207.7V, 3F, 4H, de ENERGIA ACTIVA con indice de Clase 1, y de ENERGIA REACTIVA con indice de Clase 2 con perfil de carga y medida de energia en cuatro cuadrantes
		MEDIDOR ELECTRONICO MULTIENERGIA 51/20A, 3x1/207.7V, 3F, 4H, de ENERGIA ACTIVA con indice de Clase 1, y de ENERGIA REACTIVA con indice de Clase 2
		SEÑAL QUE INDICA RETIRO
		SISTEMA DE PUESTA A TIERRA

**ESTE PROYECTO REQUIERE DE CERTIFICACION
PLENA DE ACUERDO CON EL RETIE**

AREA CONEXIÓN Y VINCULACIÓN
REVISADO

Le Te Gheer Gheer

Revisó: José Ivan Gutierrez Cardona
Vo. Bo. [Signature]

Fecha: Día 09 Mes 01 Año 2026

NOTA: CADUCIDAD DOS (2) AÑO
ANTES DE LA EJECUCION DE ESTE PROY
DEBE SOLICITARSE RECIBO TECNICO

PROYECTO:		AYURA CENTRA - AMPLIACIÓN Etapa 3	
		Calle 26 Sur No. 48 - 121141 - ENVIGADO	
		EYNER SAEZ GARCIA ING. ELECTRICISTA C/ 1.003.499.686: Whatsapp Y Cel: 323 457 59 72 C.A 63A No. 77-20207: e-mail:saenzsaez@hotmail.com - Bello-Colombia	
PROPIETARIO:		GOMURU Y CIA S. en C.A. NIT. 800.258.115 - Wh: 322 110.311 77 D.CE. 100.000.000 - Calle 68 Sur No. 121-1141 - ENVIGADO CONTACTO: JULIO MEJIA e-mail: juliojmeia@ketososa.com	
No. CONSECUTIVO:		1E 	
CONTENIDO: Tipo de: DR3			
SUBTITEN: Proyecto Interior con Medida			
Múltiple Conexión			
DISEÑO: ING. EYNER SAEZ			
DISEÑO: ING. EYNER SAEZ		MAT. AN205-162983	
SN: 23554751		ESCALA: 1/50 FECHA:ENE-2026 PLOTEO:ESCALA:1/50, HCUA:100x60cm	

PLOTEO: ESC.1:500. HOJA 100x64cm