
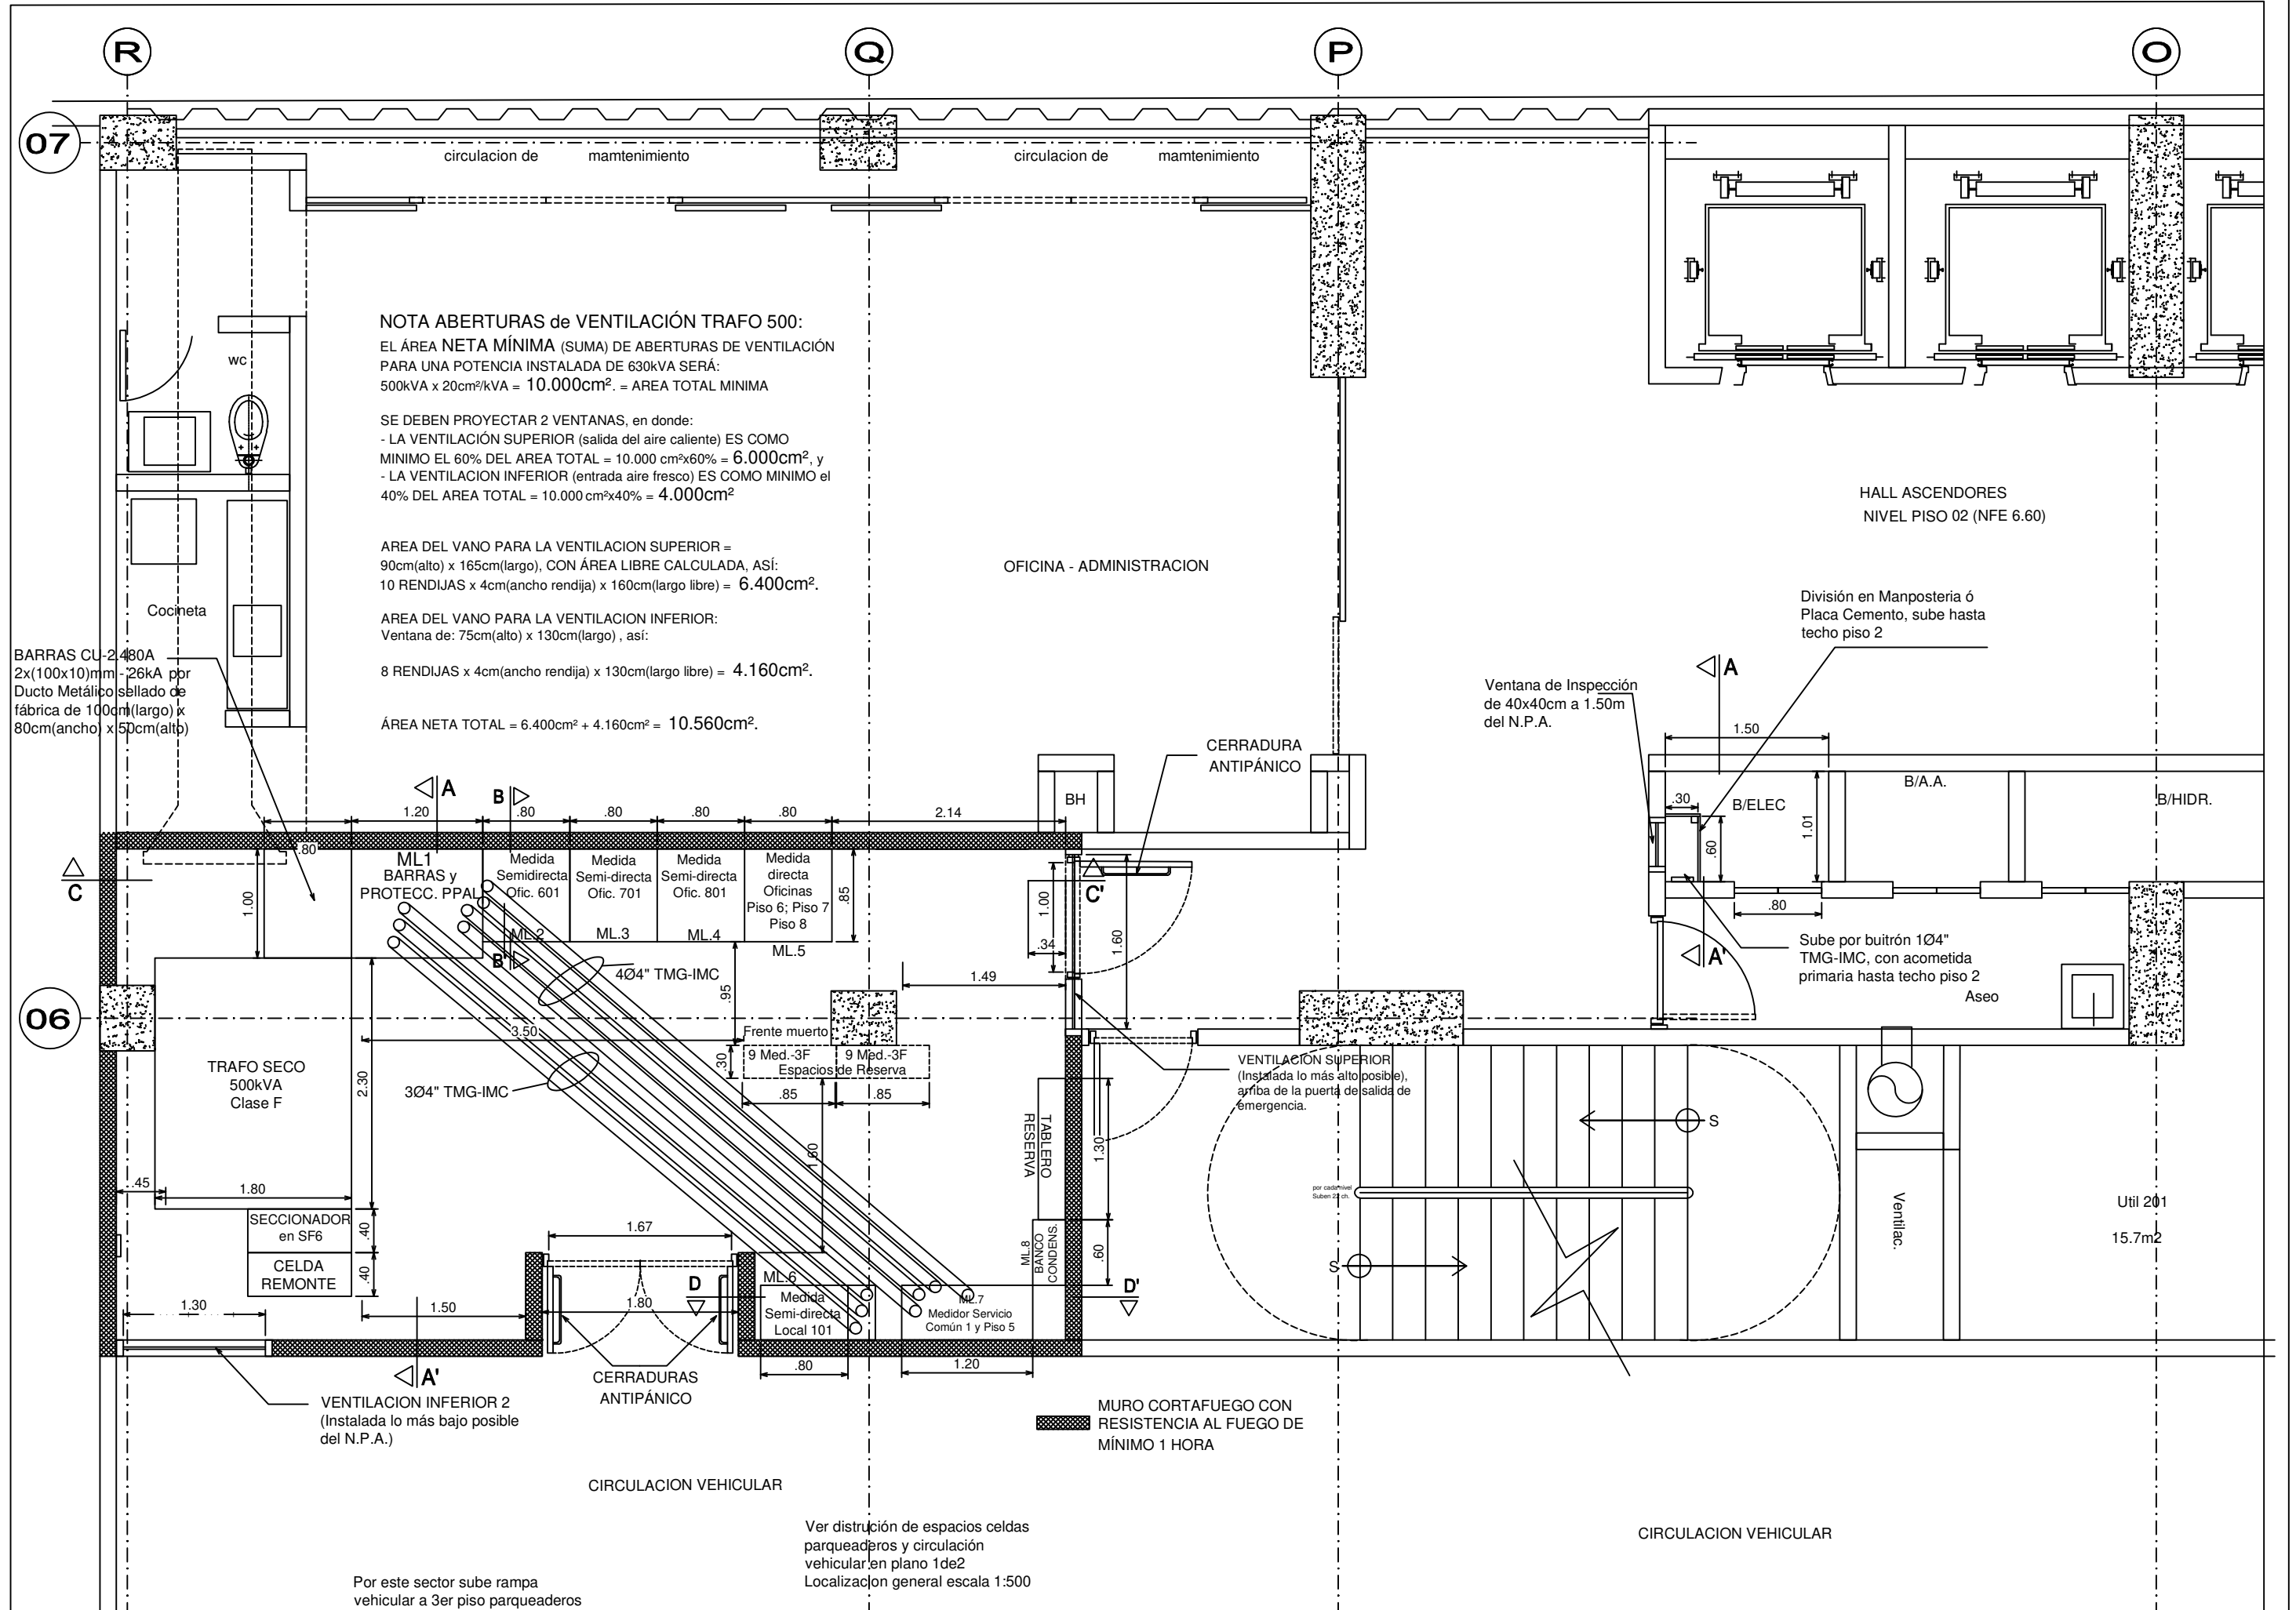
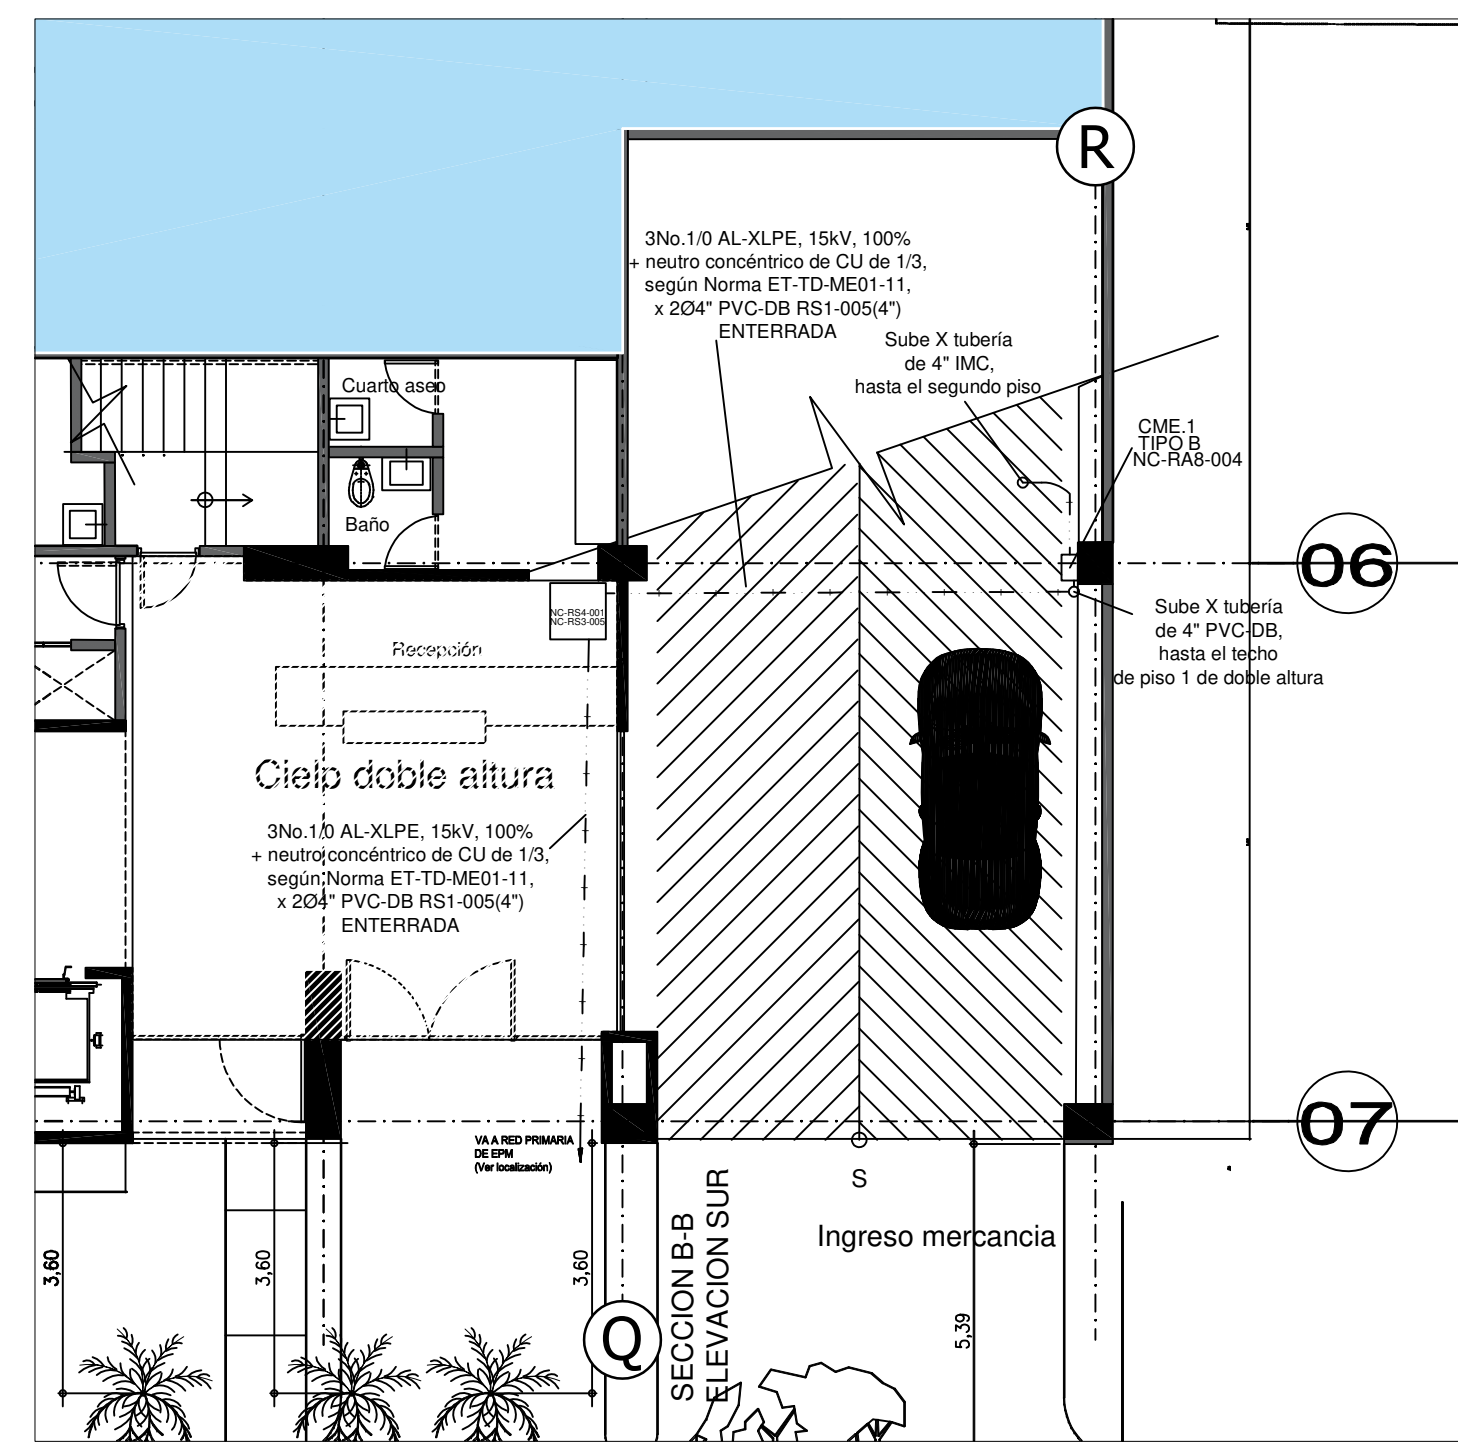
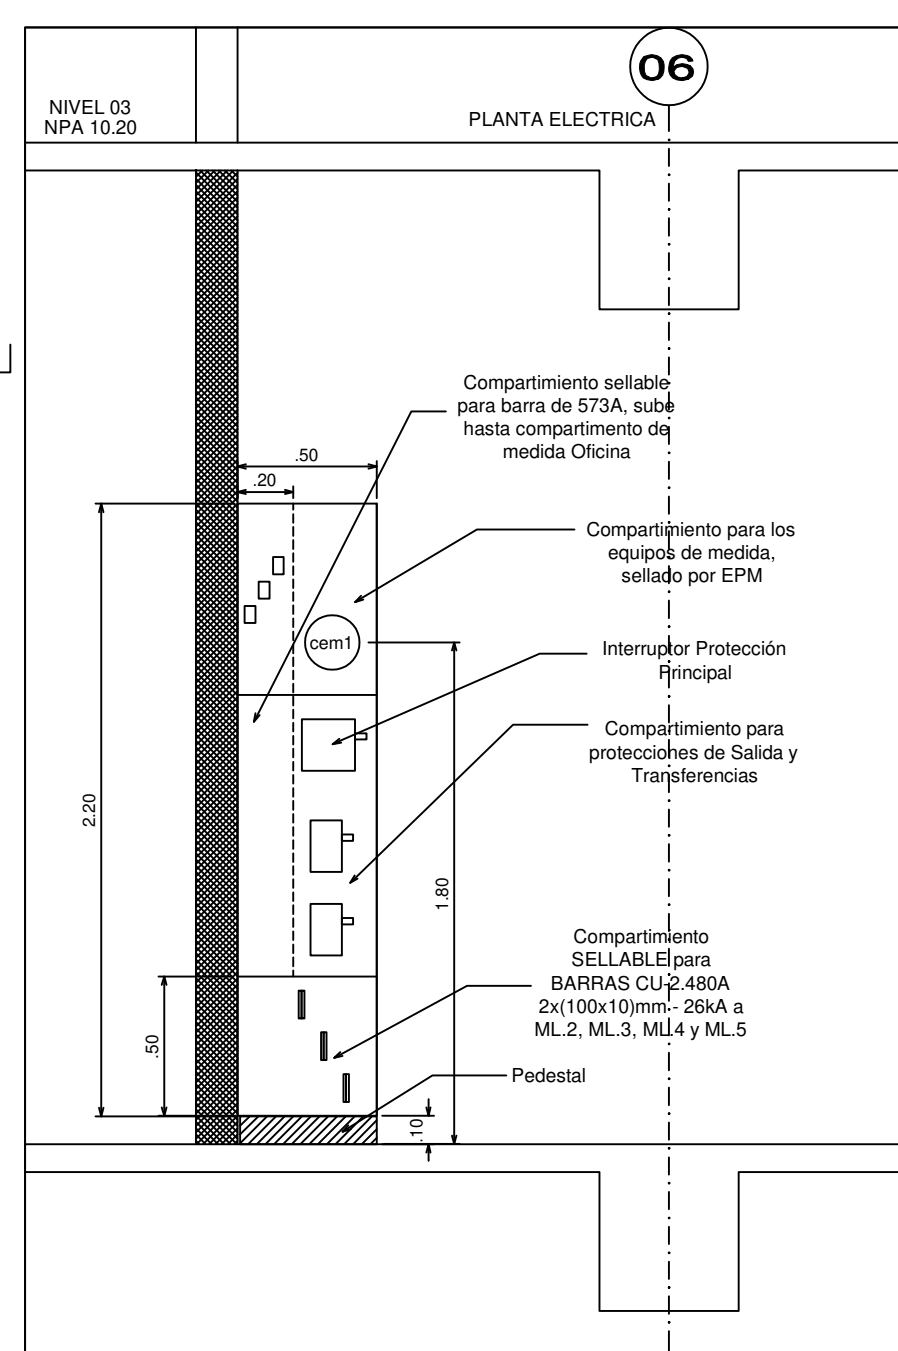
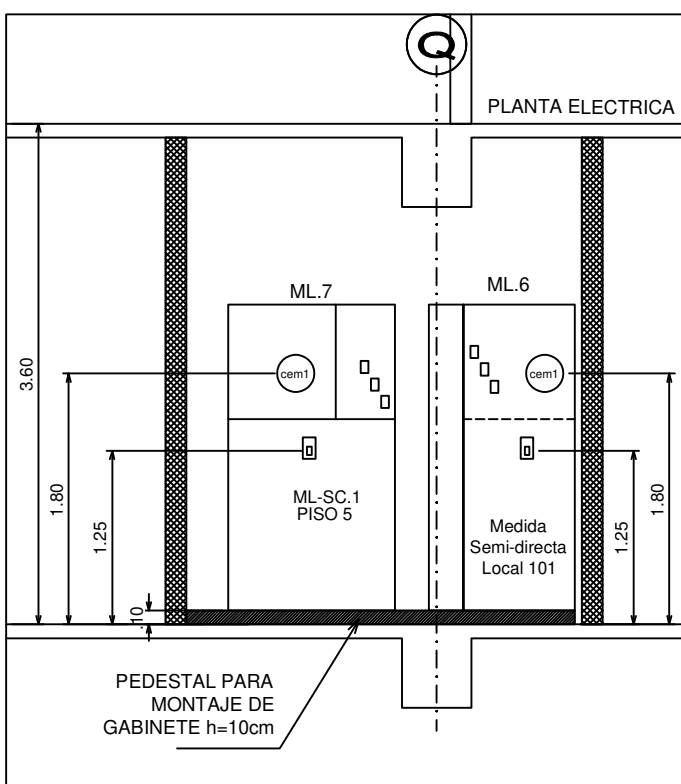
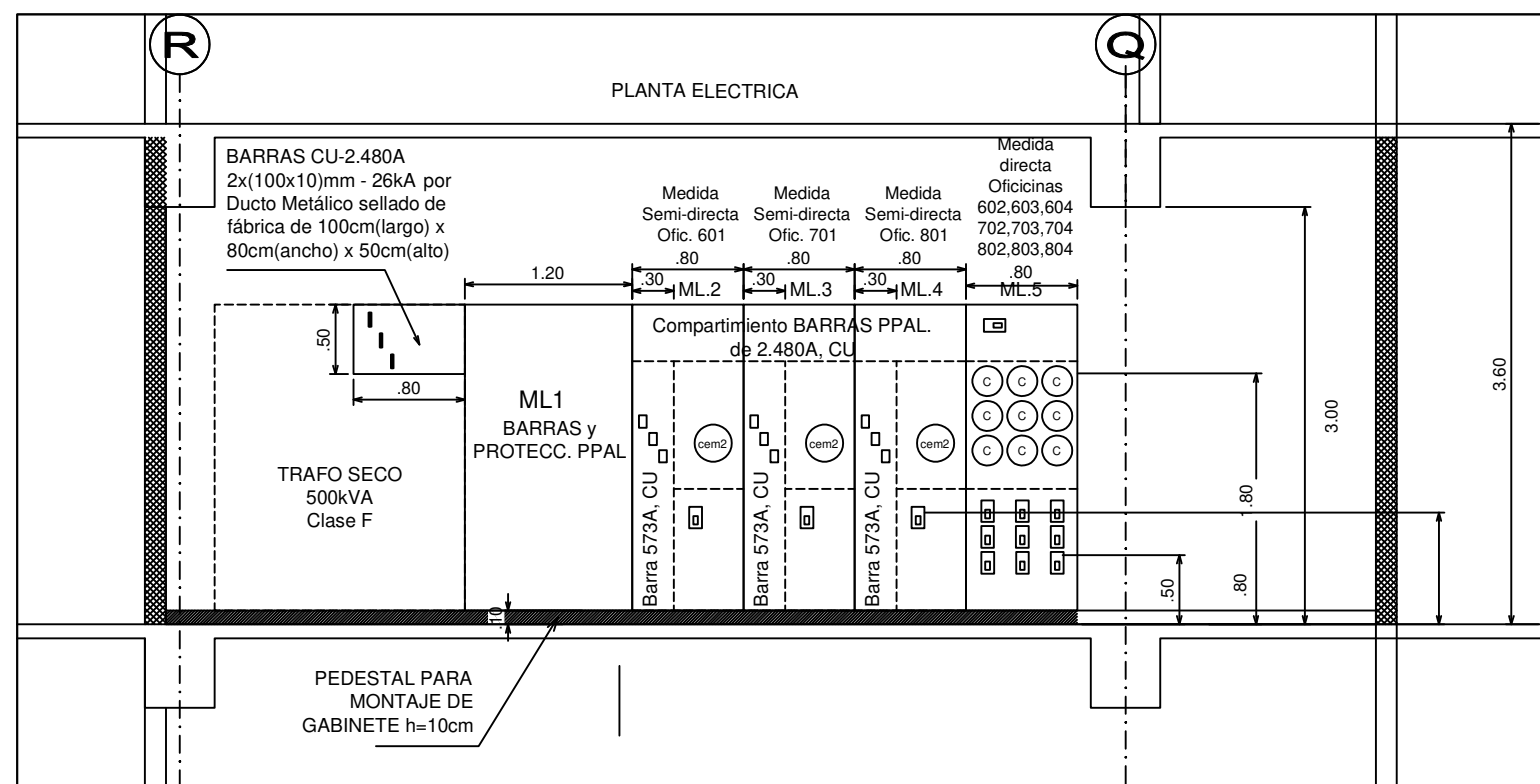
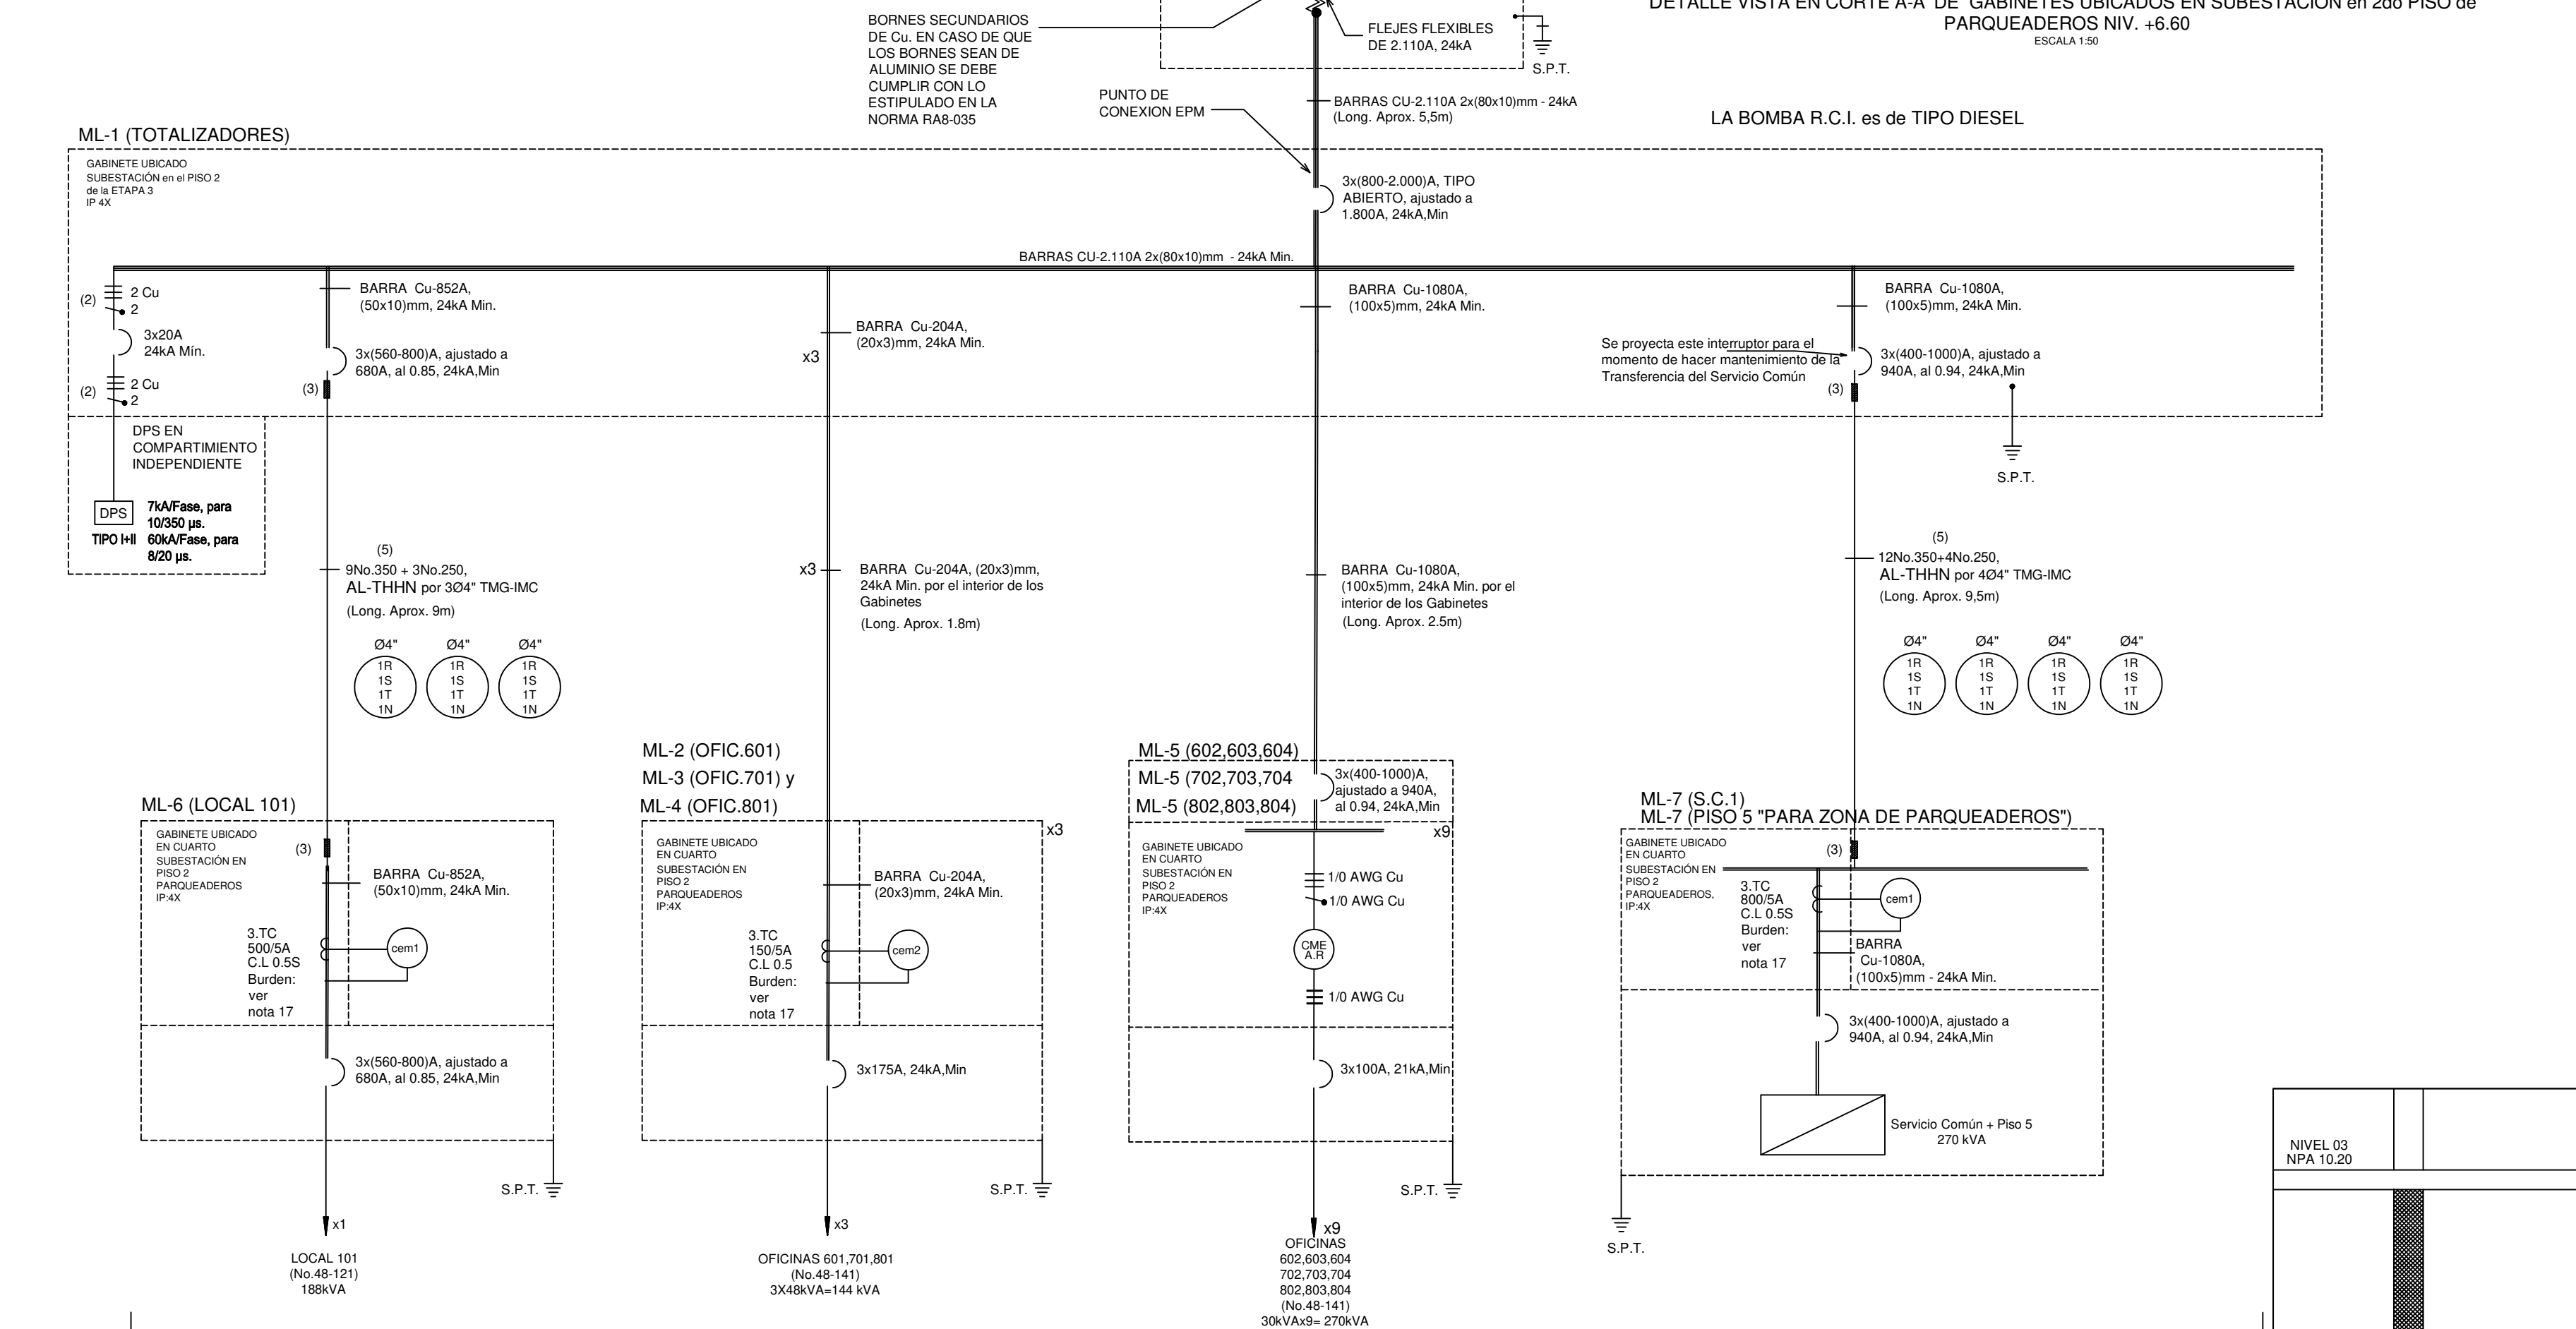


DIAGRAMA UNIFILAR TRAF0 No.1

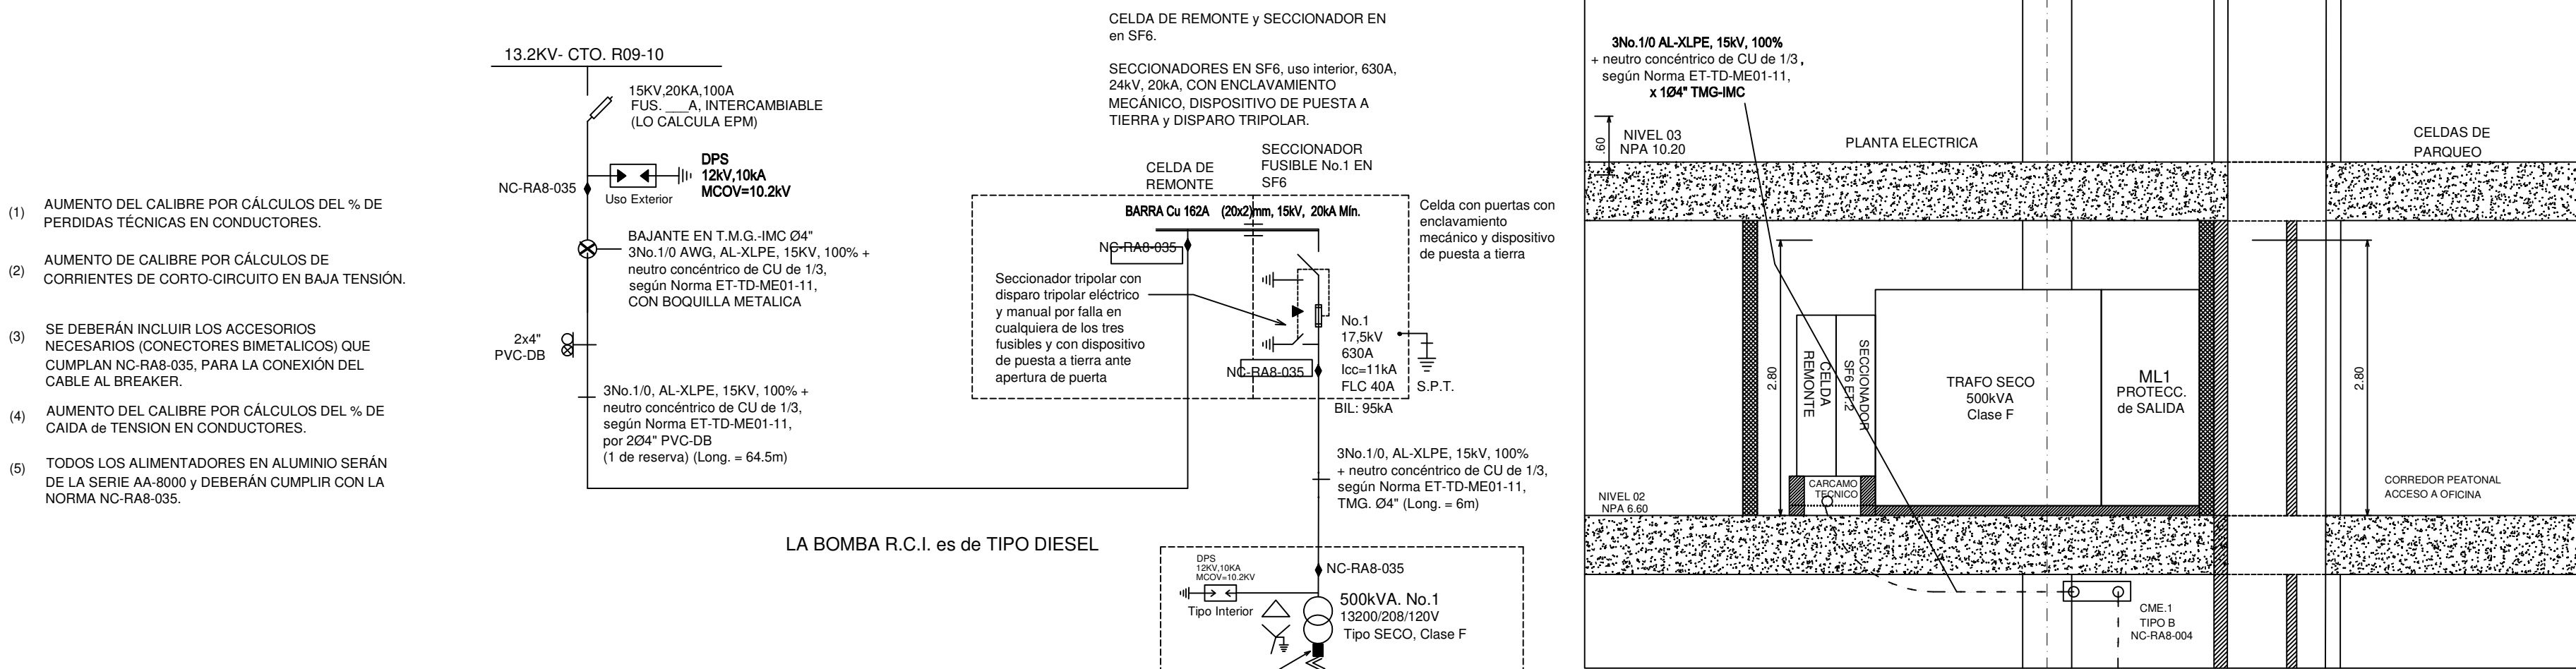

ESTE PROYECTO REQUIERE DE CERTIFICACION
PLENA DE ACUERDO CON EL RETIE

AREA CONEXION Y VINCULACION
Revisado por: **José Iván Gutiérrez Cardona**
Vo. Bo. *[Firma]*

Fecha: **Día 09 Mes 01 Año 2025**

NOTA: CADUCIDAD DOS (2) AÑO
ANTES DE LA EJECUCION DE ESTE PROYECTO
DEBE SOLICITARSE RECIBO TECNICO

PROYECTO:	AYURA CENTER - AMPLIACION Etapa 3		
	Calle 26 Sur No. 48 - 121141 - ENVIGADO		
EYNER SAENZ GARCIA			
ING. ELECTRICISTA CC 1.003.049.589, WhatsApp y Cel: 323 457 59 72			
Cra 63A No.77-20(207) e-mail:saenz1@hotmail.com Bello-Colombia			
PROPIETARIO:	GOMURI y CIA S. en C.A.		
	NIT. 900.325.475 - TEL. 332 1100 - 312 777 11 47		
	DIRECCION: Calle 26Sur No.48-121(141) - ENVIGADO		
	CONTACTO: JULIO MEJIA e-mail: julomeja@seotecosa.com		
No. CONSECUTIVO:	1E		
CONTIENE:	Proyecto Tipo: DR3		
	Subestación Tipo Interior con Medida		
	Múltiple Centralizada		
DISEÑO:	ING. EYNER SAENZ		
DIBUJO:	ING. EYNER SAENZ		
SN: 23554751	ESCALA: 1:500	FECHA: ENE-2025	MAT. AN205-162983
			2/2
PLOTEO: ESC: 1:500, HOJA: 100x64cm			