



1 VISTA EN ISOMETRICO RED REGULADA

SIN ESCALA

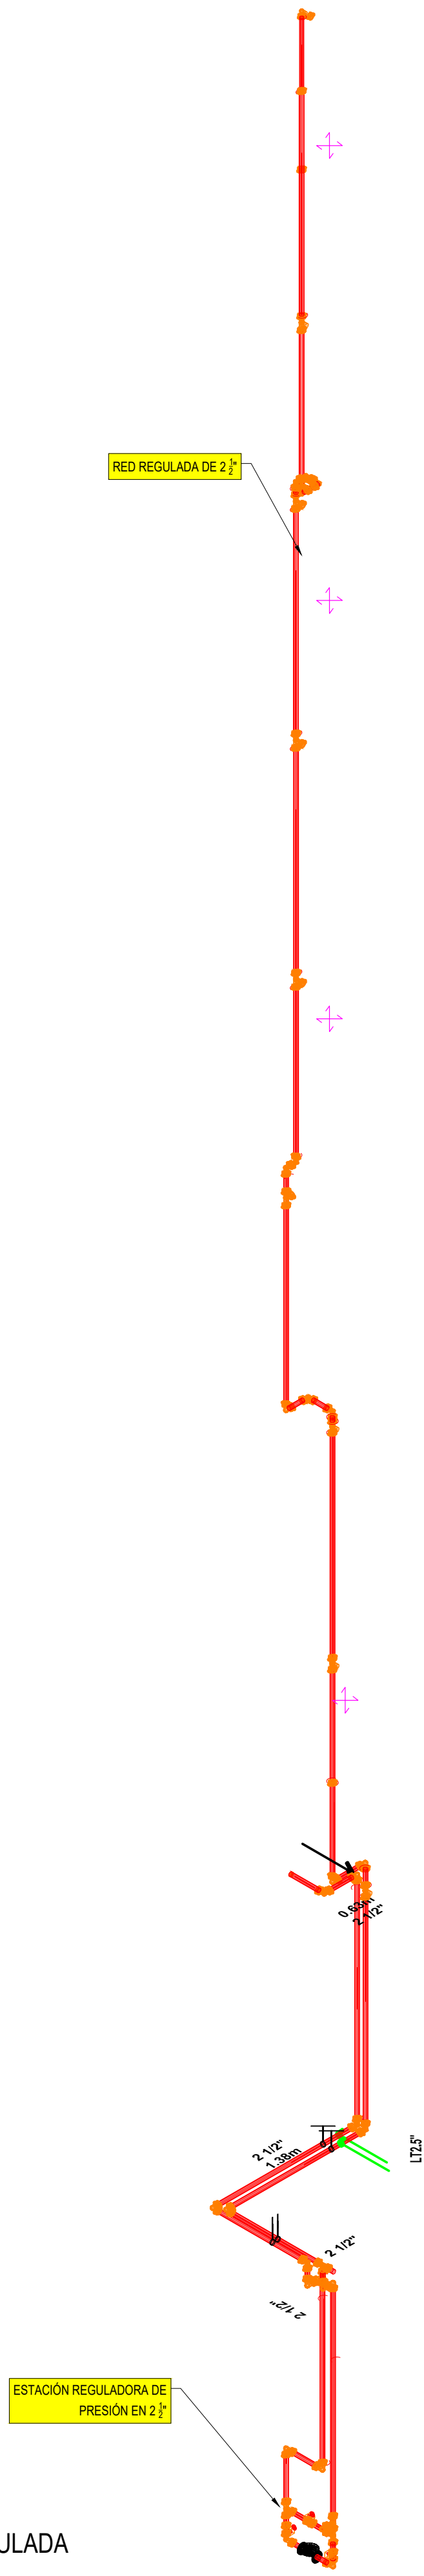


2 VISTA EN PLANTA RED REGULADA PISO 1

ESCALA 1:150

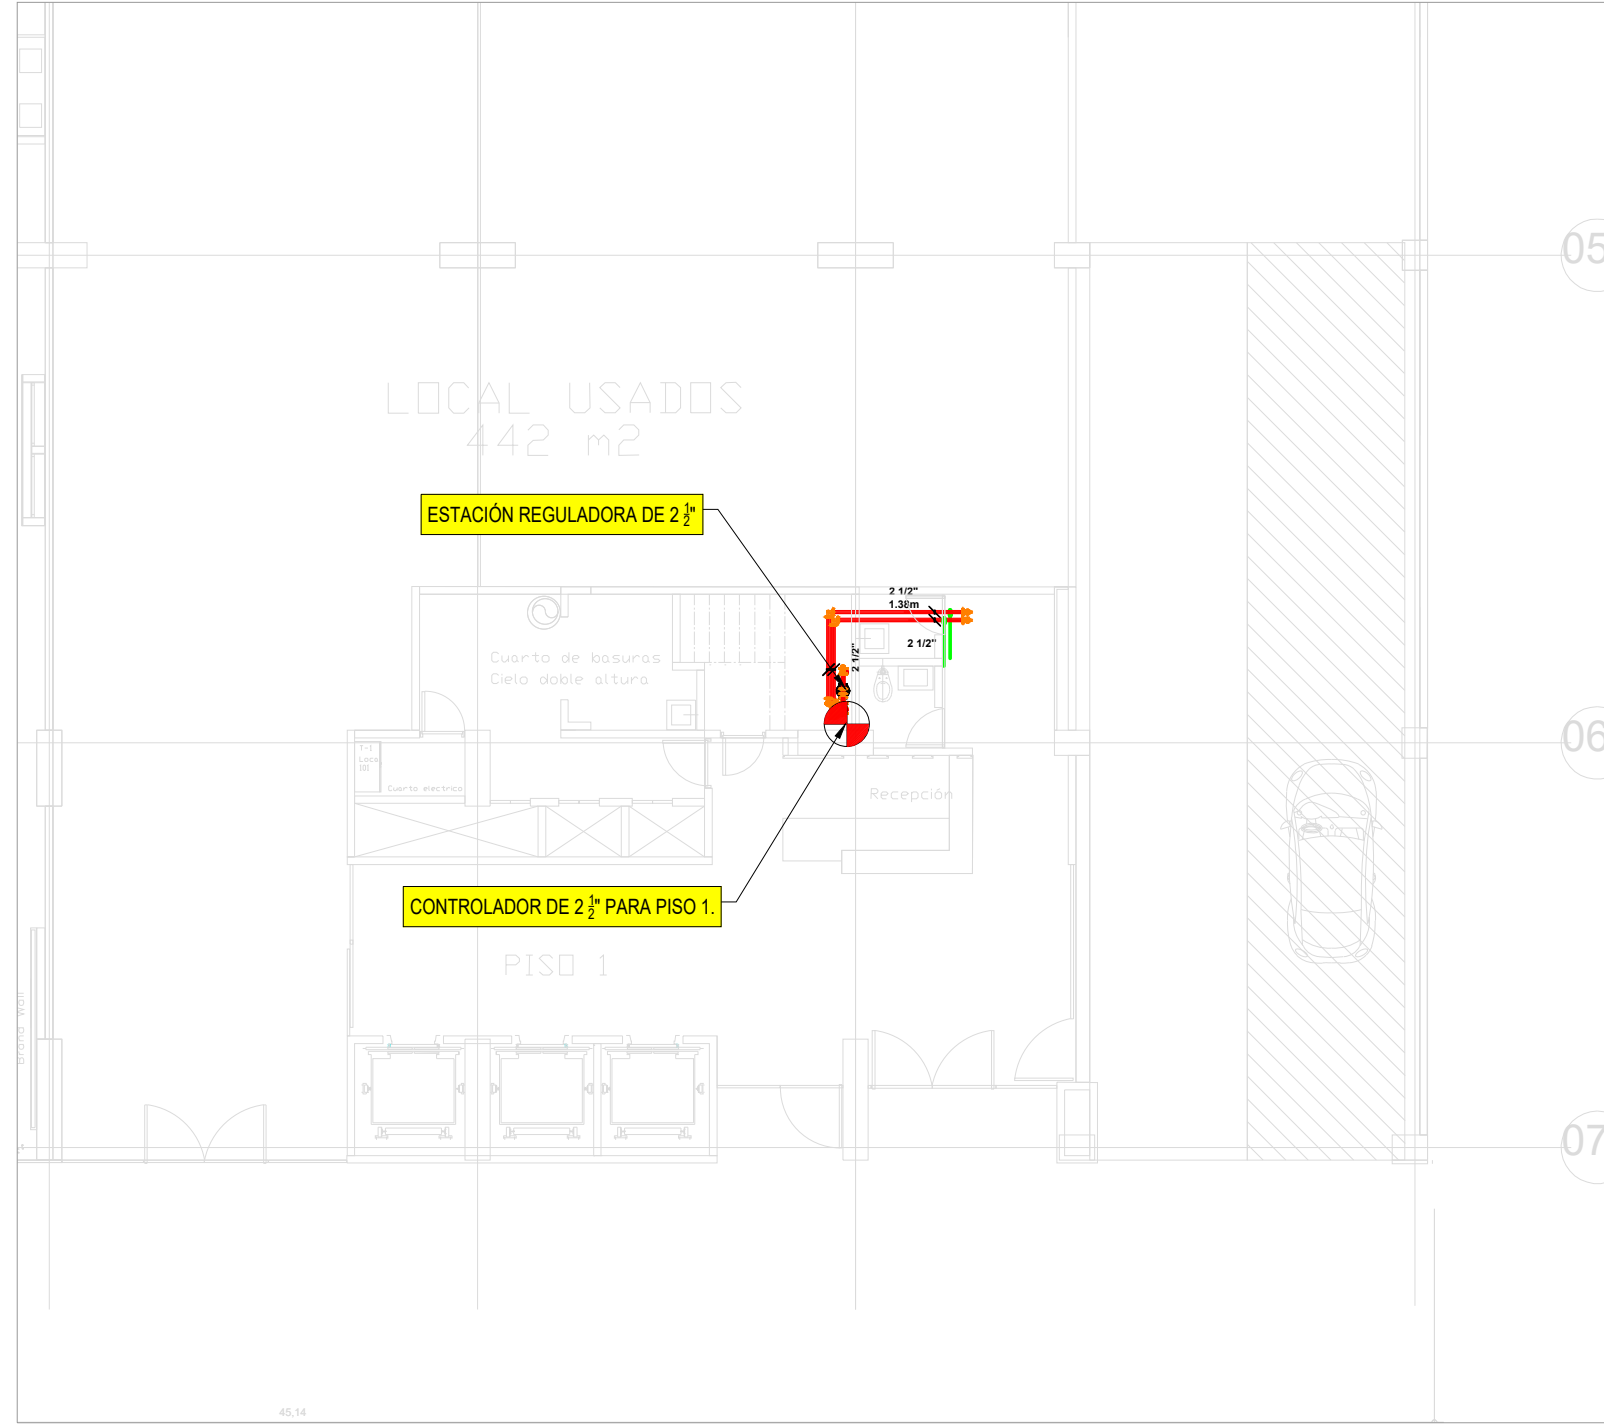


3 VISTA EN PLANTA PISO 2

ESCALA 1:150

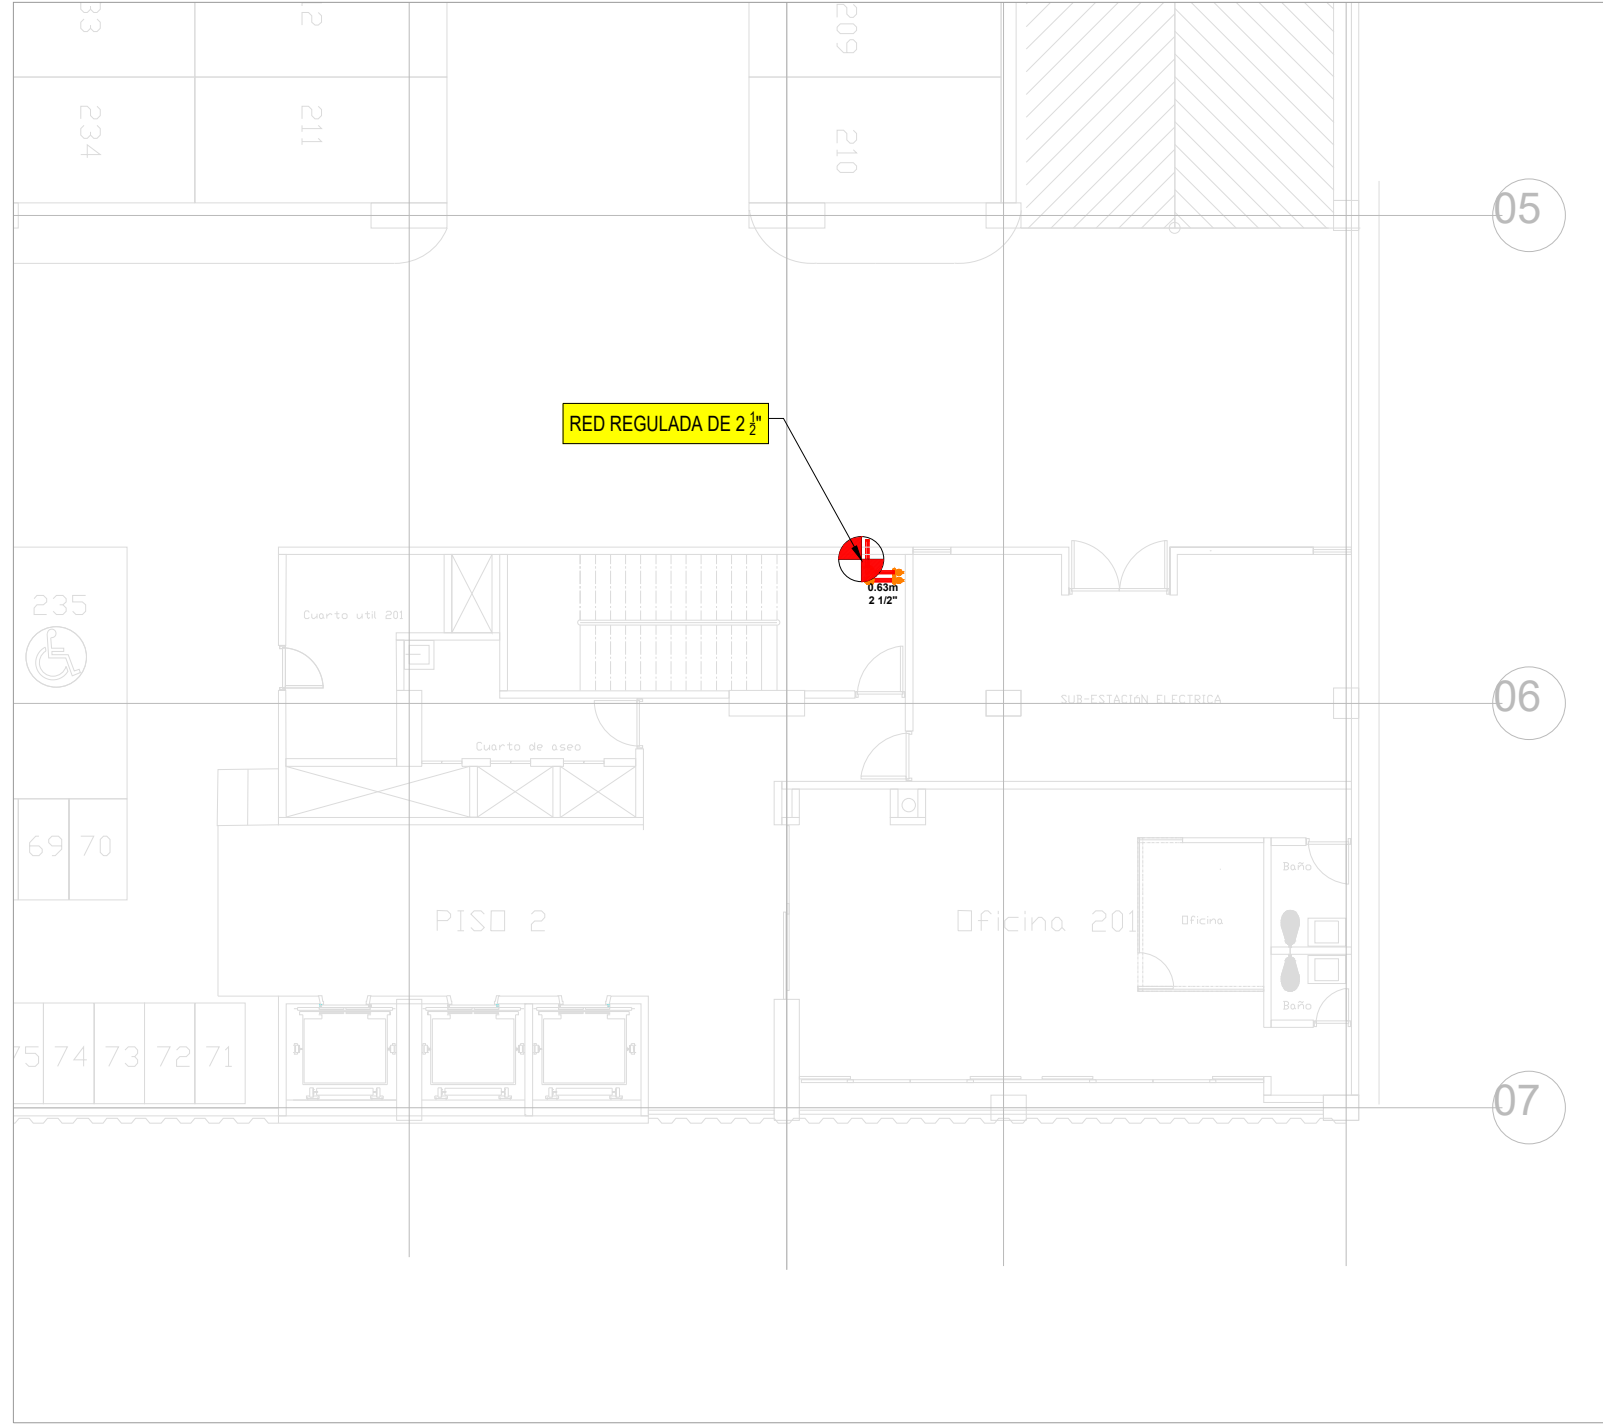



3 VISTA EN PLANTA PISO 4

ESCALA 1:150

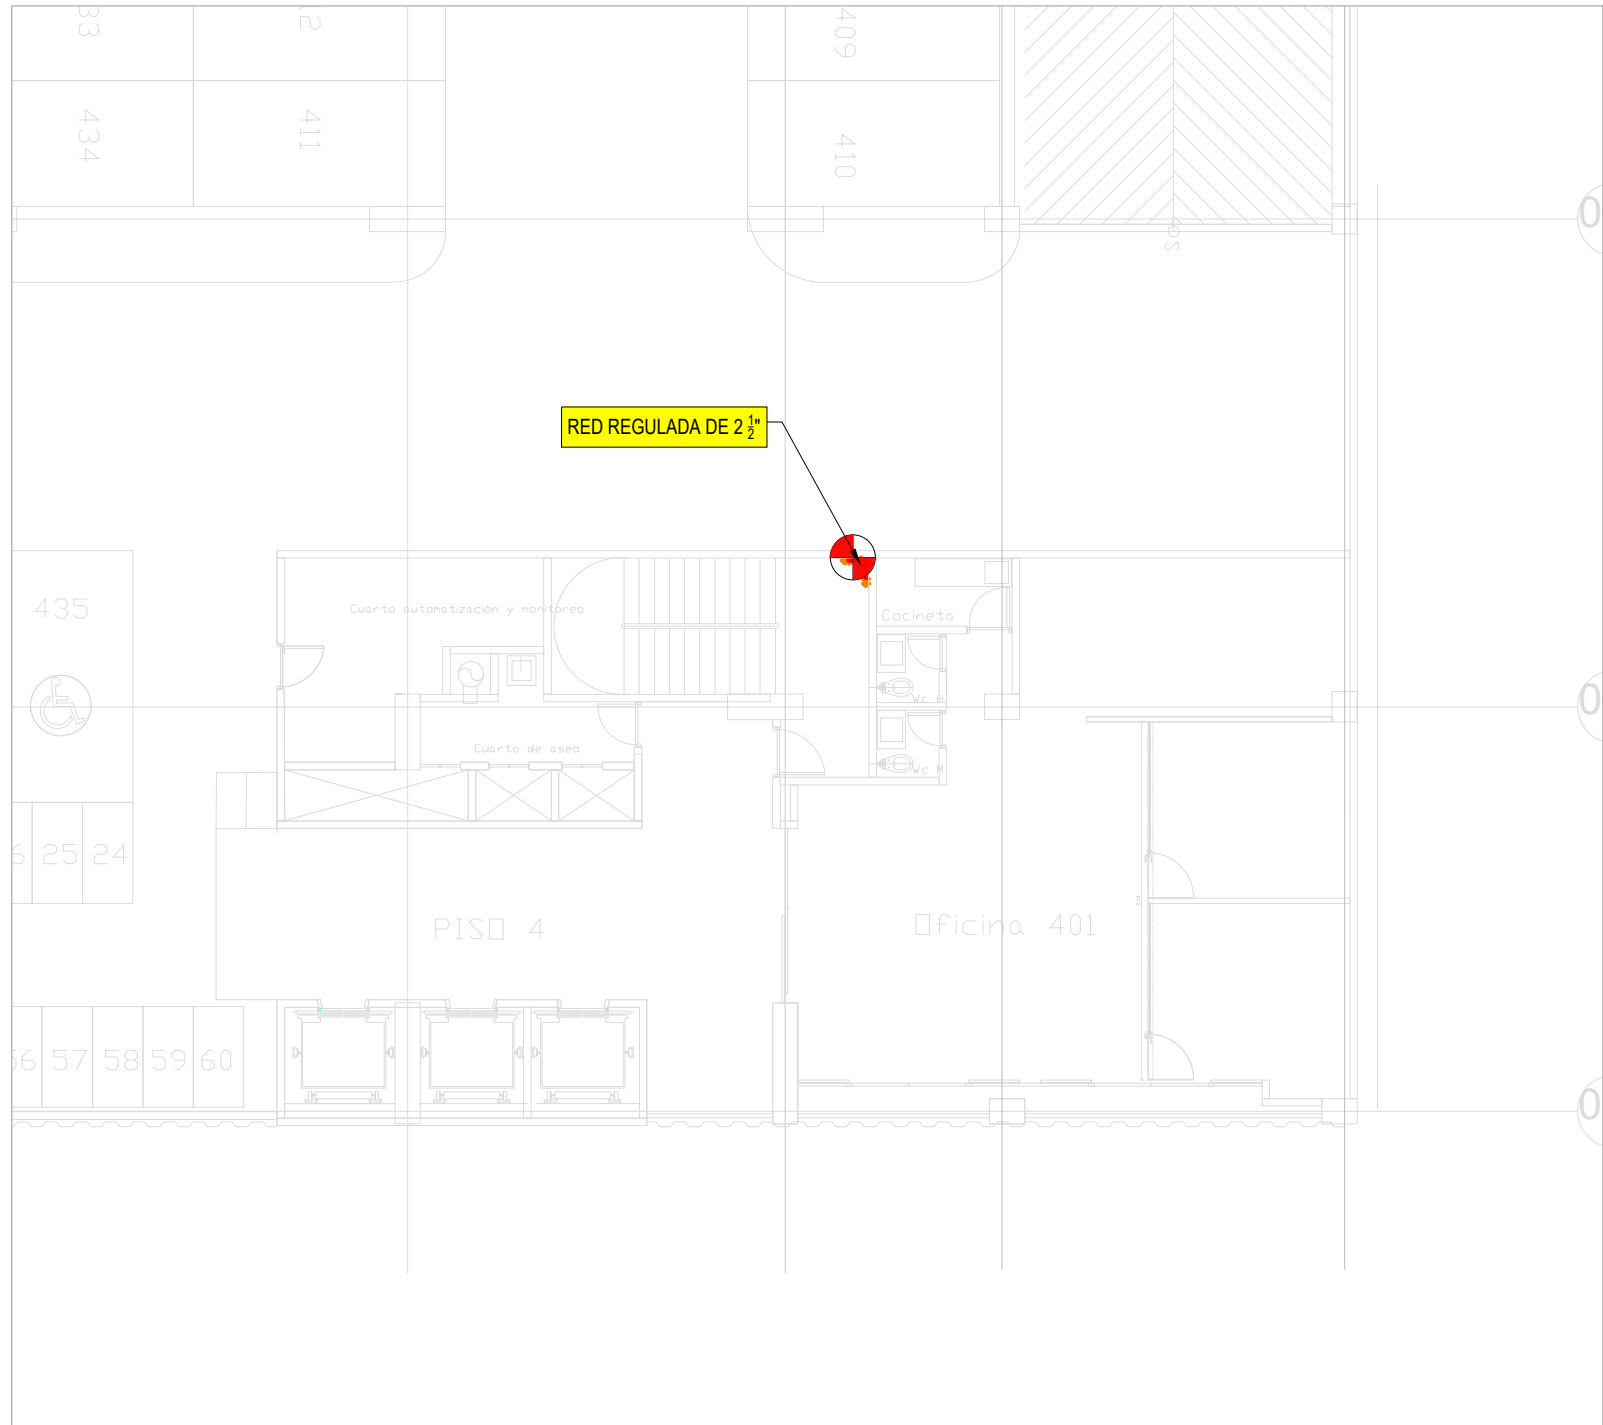

4 RED REGULADA PISO 6 A 8

ESCALA 1:150

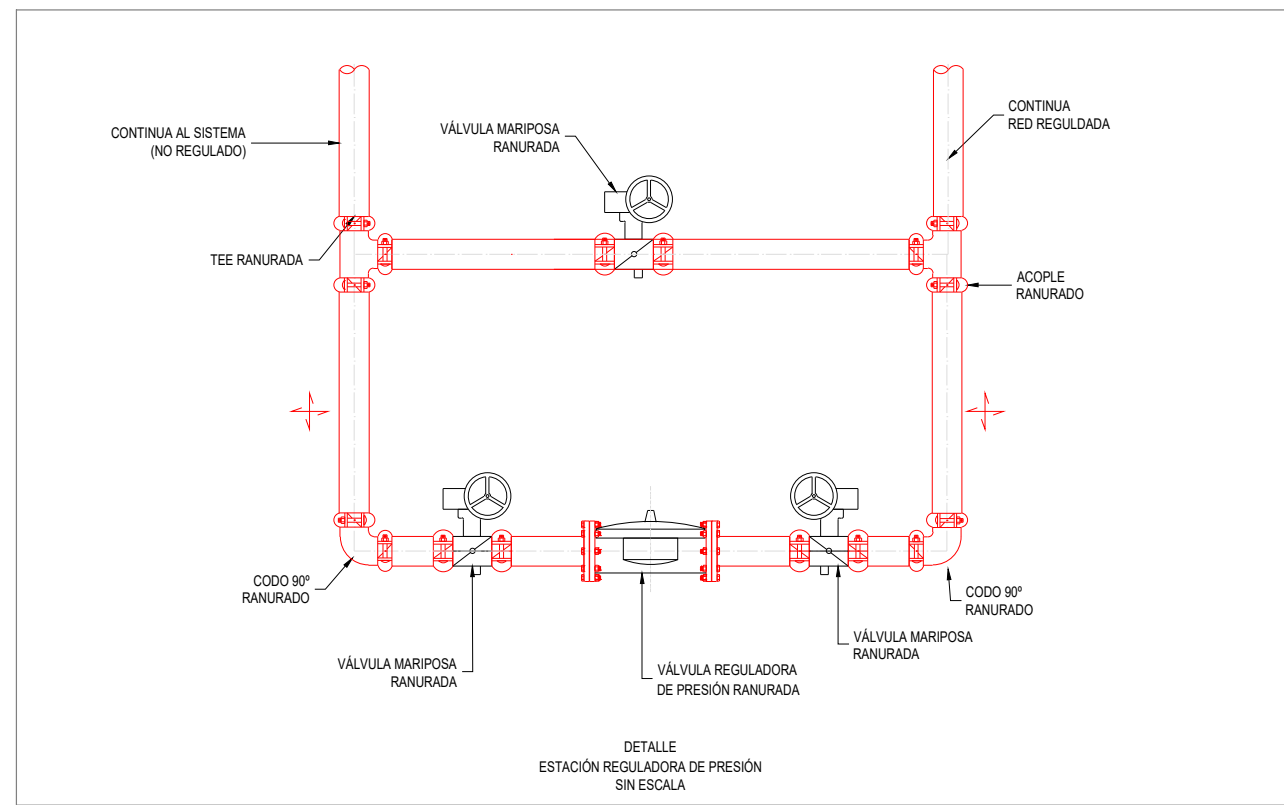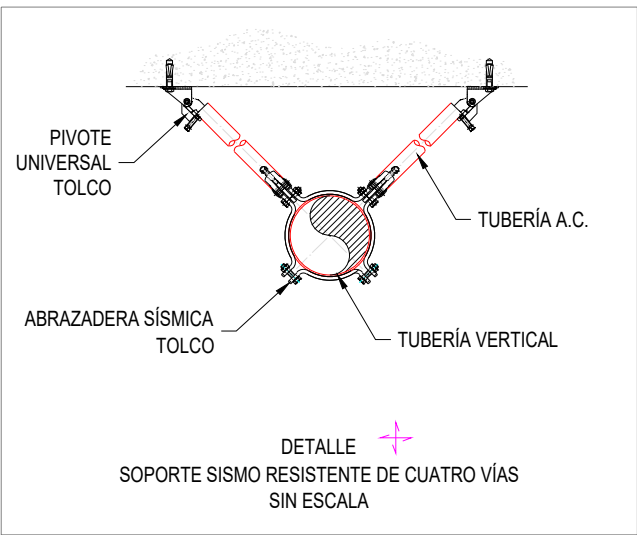

REGISTRO DE MODIFICACIONES		
MODIF.	FECHA	DESCRIPCIÓN
Δ	--	----
Δ	--	----
Δ	--	----
Δ	--	----
Δ	--	----

REGISTRO DE REVISIONES		
REV.	FECHA	EMITIDO PARA:
0	24-06-2024	ACTUALIZACION
1	18-02-2025	ACTUALIZACION
2	--	----
3	--	----
4	--	----
5	--	----
6	--	----

CONVENCIONES	
	TUBERÍA EXPUESTA
	TUBERÍA ENTERRADA
	TUBERÍA POR CÁRCAMO
	TUBERÍA CPVC
	UNIÓN RANURADA
	CODO 90° RANURADO
	TEE RANURADA
	HIDRANTE CONTRA INCENDIO
	ESTACION DE MANGUERA SISTEMA HUMEDO
	RISER (SISTEMA CONTROLADOR)
	SIAMESA CONEXION PARA BOMBEROS 4"x2 1/2"x2 1/2"
	NODO HIDRAULICO
	ÁREA DE DISEÑO
	SOPORTE COLGANTE
	SOPORTE SÍSMICO CUATRO VÍAS
	SOPORTE SÍSMO RESISTENTE LONGITUDINAL
	SOPORTE SÍSMO RESISTENTE LATERAL
	BLOQUEO DE EMPUJE
	VÁLVULA DE INSPECCIÓN, PRUEBA Y DRENAJE
	VÁLVULA DESAIREADORA
	FUTURA CONEXIÓN
	UNIÓN SÍSMICA
	ESTACION DE MANGUERA CLASE II

ELABORADO POR:

DyC Constructores S.A.S

ELABORADO PARA:

AYURA MOTORS ETAPA 3

ENIGADO-ANTIOQUIA

PROYECTO:

SISTEMA DE EXTINCIÓN DE INCENDIOS

CONTIENE:

RED REGULADA
ISOMETRICO Y VISTAS EN PLANTA

ELABORÓ:	REVISÓ:
MODELO:	UNIDADES: Metros
FECHA: 14-11-2025	ESCALA: INDICADAS
VERSIÓN: 05	VERS. MOD: 05
PROYECTO No: GL 706	FORMATO: A1
PLANO No. PLANO 12 de 12	

NOTAS:

- LAS LONGITUDES SE INDICAN EN METROS Y LOS DIÁMETROS EN PULGADAS
- ESTE DOCUMENTO CORRESPONDE A UN PLANO DE DISEÑO, LAS DIMENSIONES INDICADAS DEBEN SER VERIFICADAS EN OBRA