
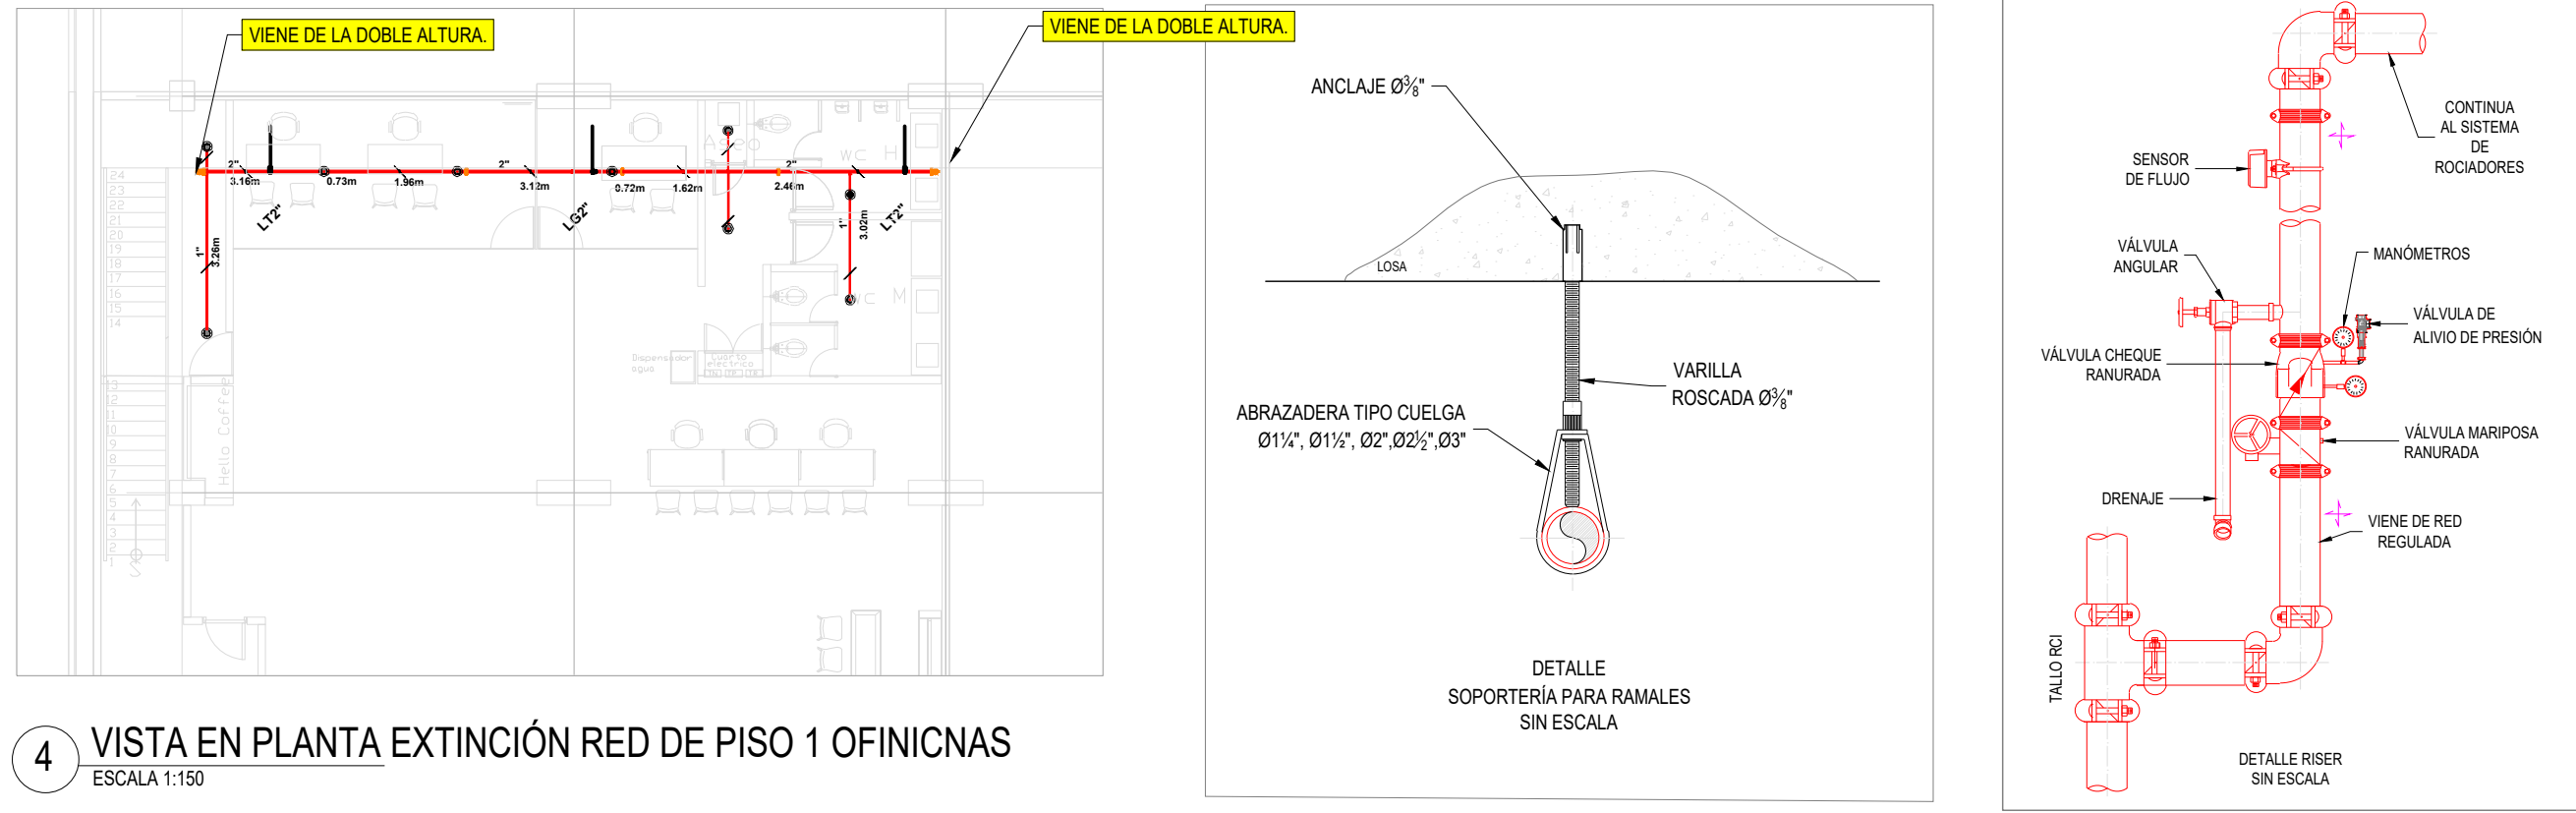
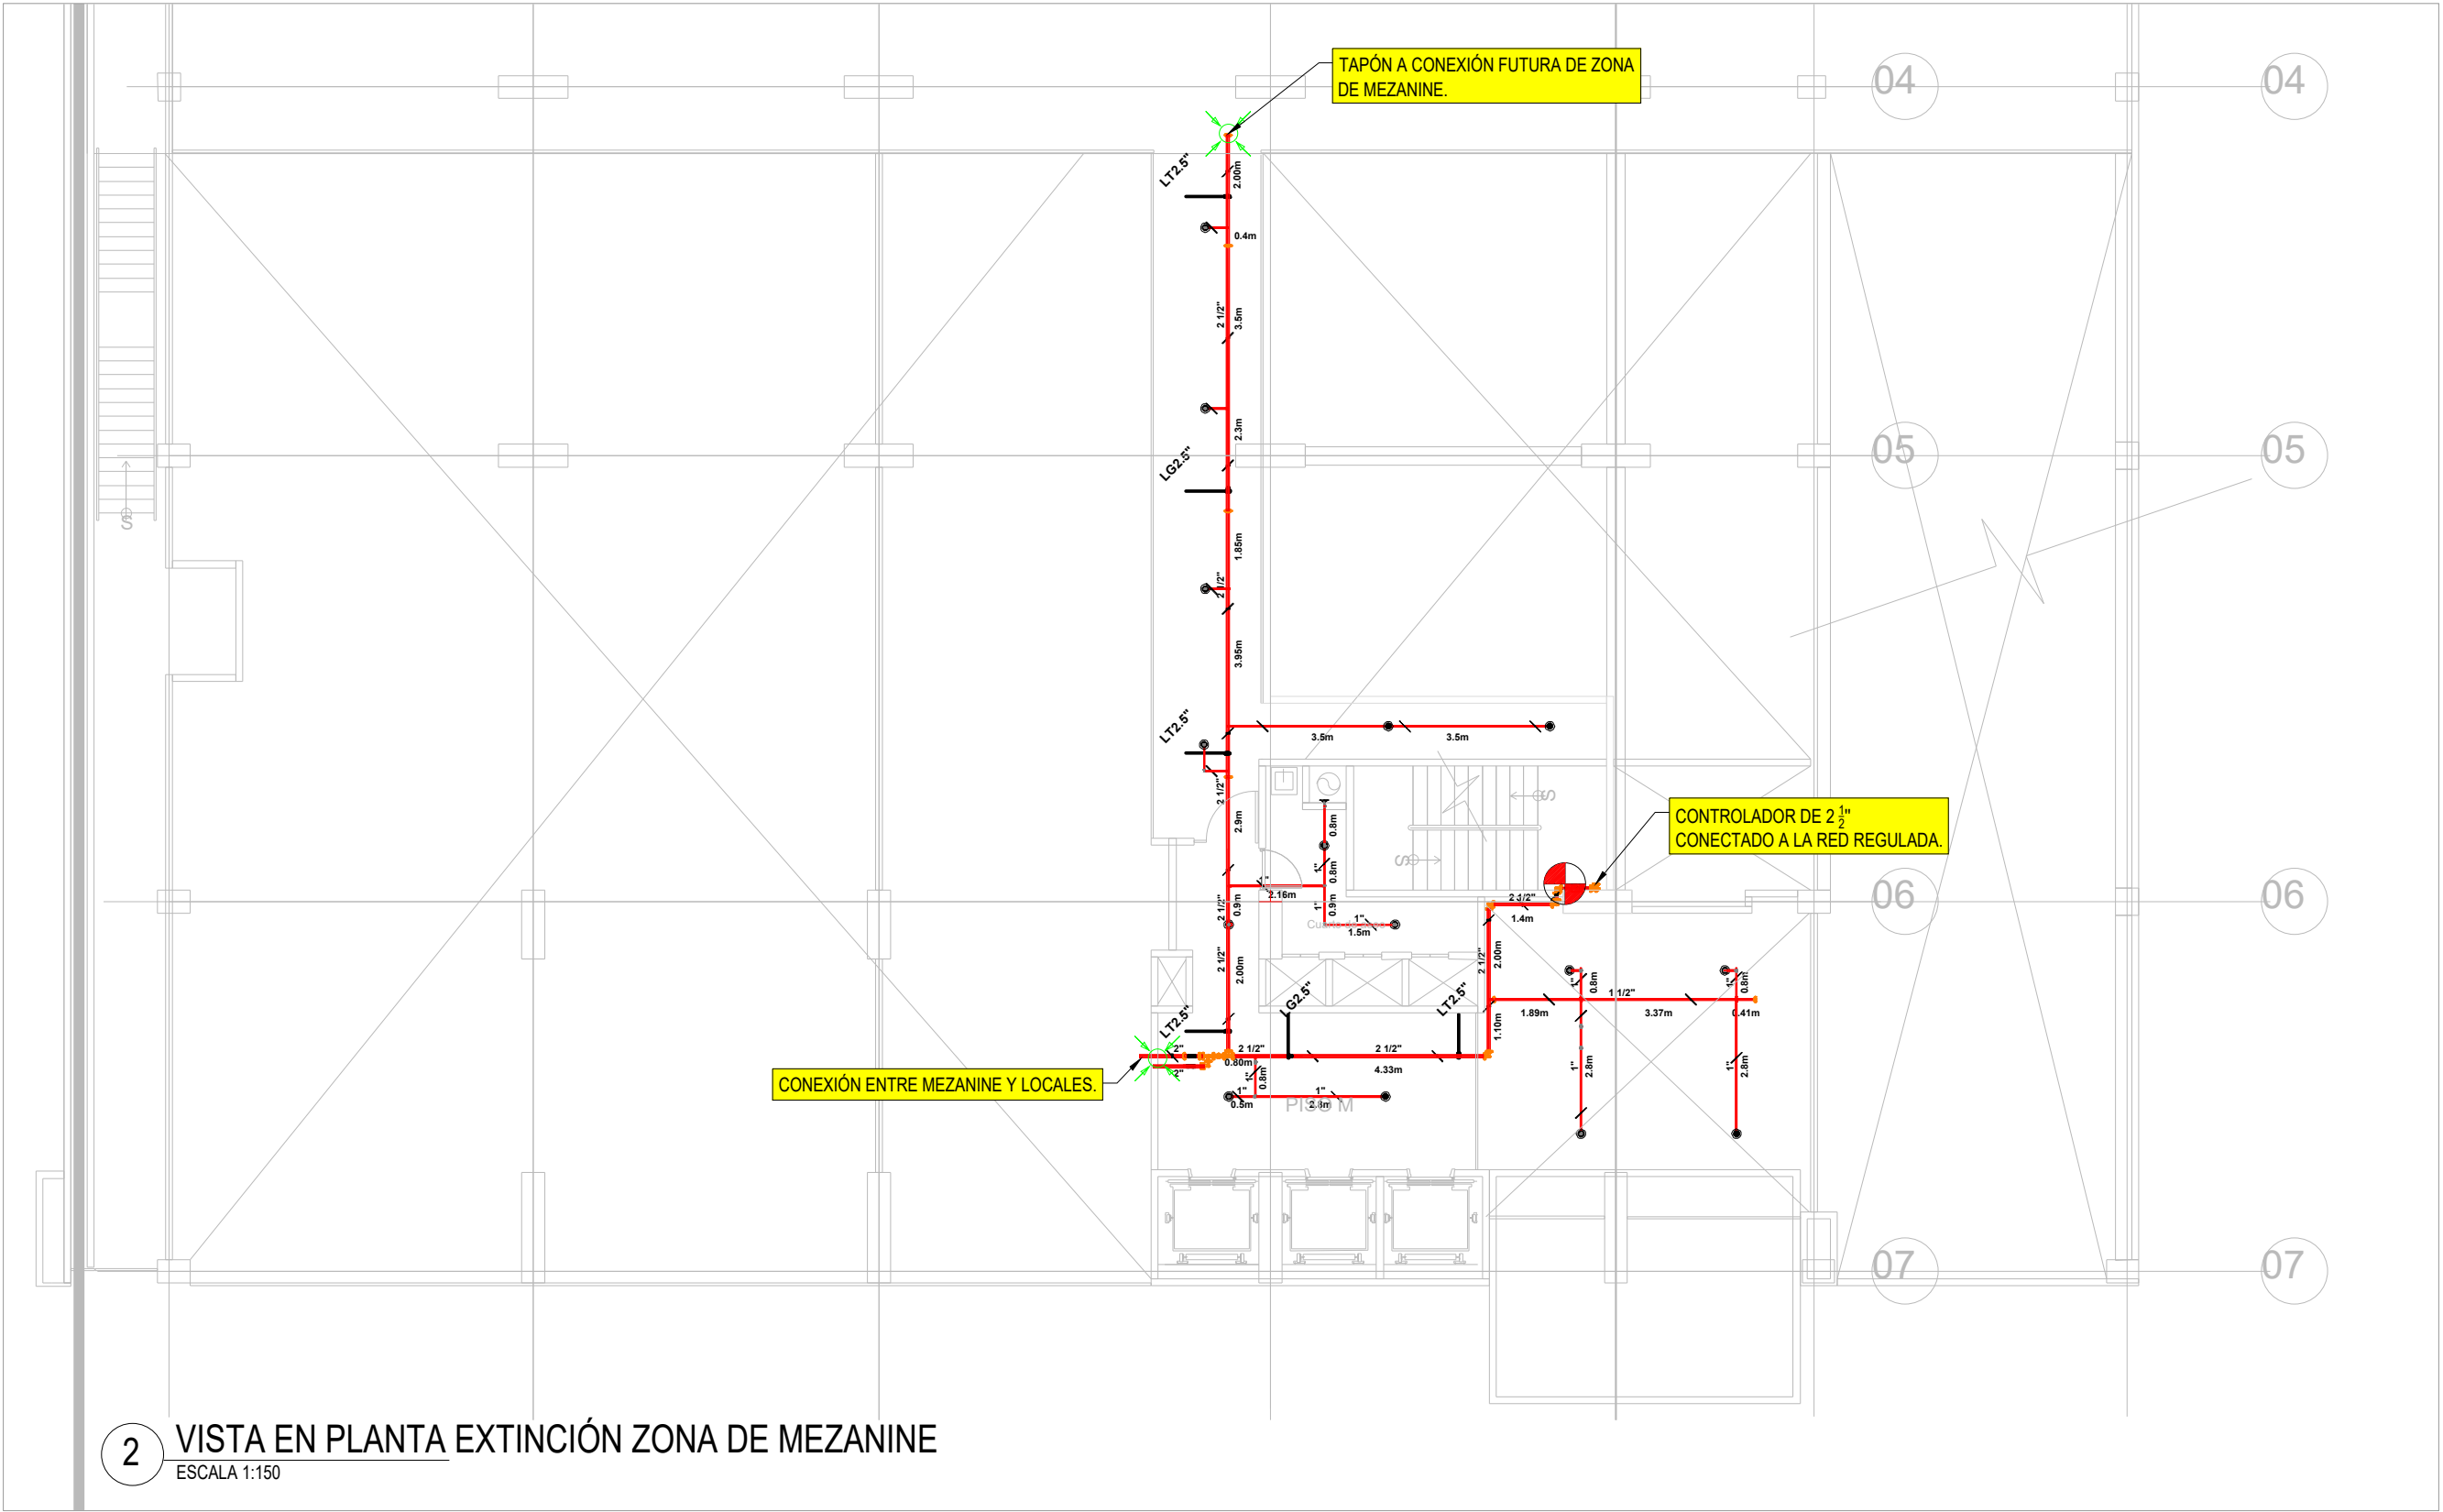


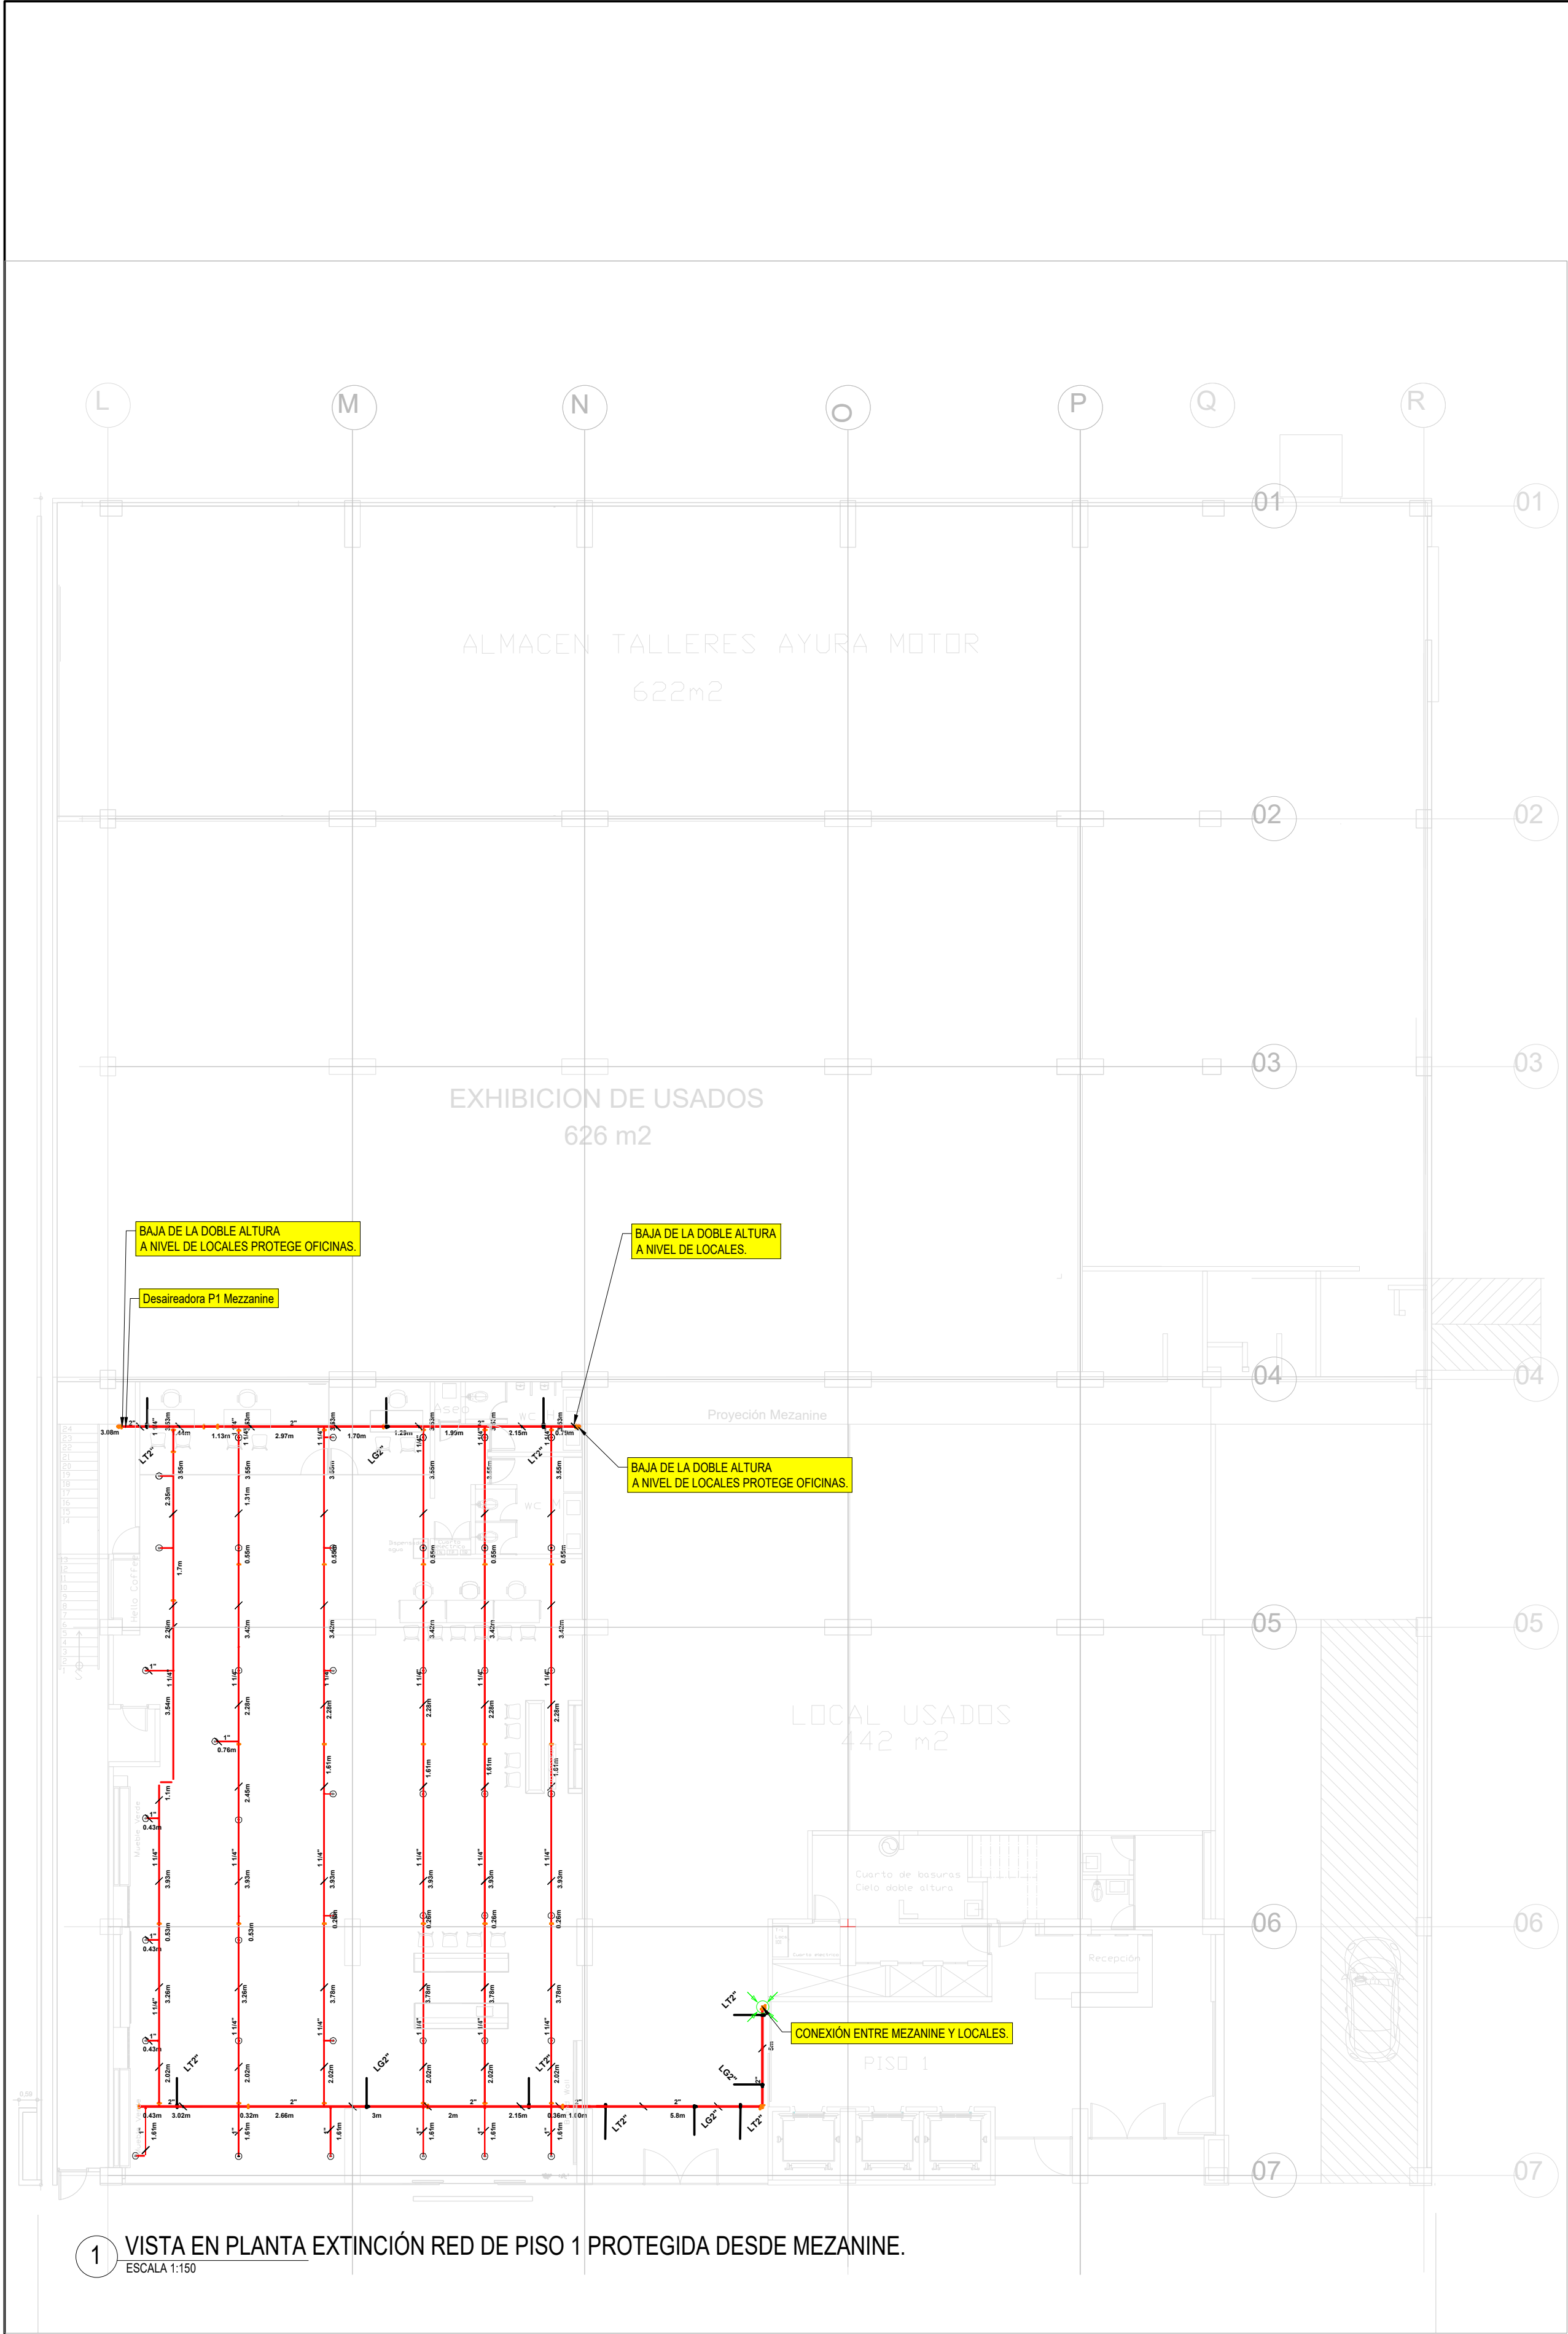


Sway Brace Zone Legend				
Diameter	Description	Unit Quantity	Quantity	Unit Weight
1.5"	Pipe, Schedule 40	(14.25m)	12.75m	2.77kg (6.15)
1.5"	Pipe, Schedule 40	(14.25m)	12.75m	2.77kg (6.15)
1.5"	Pipe, Schedule 40	(14.25m)	12.75m	2.77kg (6.15)
Total Load (x 1.15)				89.55kg

Sway Brace Tag				
Brace Type	Brace Pipe Size	Fastener Type	Fastener Orientation	
Longitudinal	1"	Anchor, HLT1 Hook Bolt T2 (CS)	MPFA Type "A"	
Brace Angle	30°	Attached To	Fastener Size	Maximum Fastener Load
30°	Normal Weight Concrete (2400psi)	240.5kg		
Code: MPFA #13 - 2007		Table: 3.3.5.5.1	Plan ID: LQ2.4"	Manufacturer: Talcot Inc.

Sway Brace Zone Legend				
Diameter	Description	Unit Quantity	Quantity	Unit Weight
1.5"	Pipe, Schedule 40	(14.25m)	12.75m	2.77kg (6.15)
1.5"	Pipe, Schedule 40	(14.25m)	12.75m	2.77kg (6.15)
1.5"	Pipe, Schedule 40	(14.25m)	12.75m	2.77kg (6.15)
Total Load (x 1.15)				89.55kg

Sway Brace Tag				
Brace Type	Brace Pipe Size	Fastener Type	Fastener Orientation	
Longitudinal	1"	Anchor, HLT1 Hook Bolt T2 (CS)	MPFA Type "A"	
Brace Angle	30°	Attached To	Fastener Size	Maximum Fastener Load
30°	Normal Weight Concrete (2400psi)	240.5kg		
Code: MPFA #13 - 2007		Table: 3.3.5.5.1	Plan ID: LQ2.4"	Manufacturer: Talcot Inc.

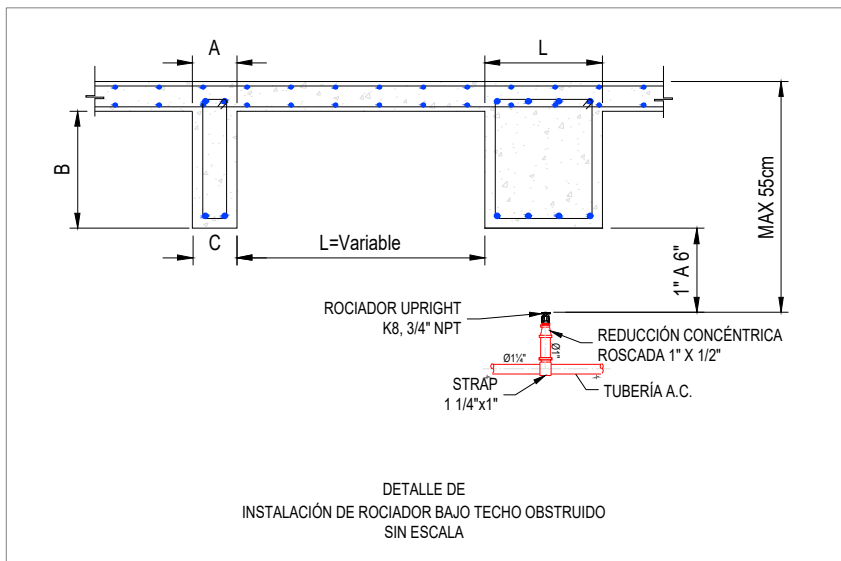

REGISTRO DE MODIFICACIONES		
MODIF.	FECHA	DESCRIPCIÓN
1	--	----
2	--	----
3	--	----
4	--	----
5	--	----
6	--	----

REGISTRO DE REVISIONES		
REV.	FECHA	EMITIDO PARA:
0	24-06-2024	ACTUALIZACION
1	18-02-2025	ACTUALIZACION
2	--	----
3	--	----
4	--	----
5	--	----
6	--	----

CARACTERÍSTICAS ROCIADORES			
ORIENTACIÓN	K	ROSCA TEMPERATURA RESPUESTA	COBERTURA
UPRIGHT	8	3/4"	68°C
PENDENT	8	3/4"	68°C
RAPIDA			
ESTANDAR			

CARACTERÍSTICAS ROCIADORES			
ORIENTACIÓN	K	ROSCA TEMPERATURA RESPUESTA	COBERTURA
UPRIGHT	8	3/4"	68°C
PENDENT	8	3/4"	68°C
RAPIDA			
ESTANDAR			

CONVENCIONES	
	TUBERÍA EXPUESTA
	TUBERÍA ENTERRADA
	TUBERÍA POR CÁRCAMO
	TUBERÍA CPVC
	UNIÓN RANURADA
	CODO 90° RANURADO
	TEE RANURADA
	HIDRANTE CONTRA INCENDIO
	ESTACION DE MANGUERA SISTEMA HUMEDO
	RISER (SISTEMA CONTROLADOR)
	SIAMESA CONEXION PARA BOMBEROS 4"x2 1/2"x 2 1/2"
	NODO HIDRAULICO
	ÁREA DE DISEÑO
	SOPORTE COLGANTE
	SOPORTE SÍSMICO CUATRO VÍAS
	SOPORTE SÍSMICO RESISTENTE LONGITUDINAL
	SOPORTE SÍSMICO RESISTENTE LATERAL
	BLOQUE DE EMPUJE
	ITC
	VÁLVULA DE INSPECCIÓN, PRUEBA Y DRENAJE
	VÁLVULA DESAIREADORA
	FUTURA CONEXIÓN
	UNIÓN SÍSMICA
	ESTACION DE MANGUERA CLASE II

ELABORADO POR:

DyC Constructores S.A.S

ELABORADO PARA:

AYURA MOTORS ETAPA 3

ENVIGADO-ANTIOQUIA

PROYECTO:

SISTEMA DE EXTINCIÓN DE INCENDIOS

CONTIENE:

ROCIADORES MEZANINE

ELABORÓ:

REVISÓ:

MODELO:

UNIDADES: Metros

FECHA:

14-11-2024

ESCALA: INDICADAS

VERSIÓN: 05

VERS. MOD: 05

FORMATO: A1

PROYECTO No: GL 706

PLANO No. PLANO 2 de 12

NOTAS:

- LAS LONGITUDES SE INDICAN EN METROS Y LOS DIÁMETROS EN PULGADAS

- ESTE DOCUMENTO CORRESPONDE A UN PLANO DE DISEÑO, LAS DIMENSIONES INDICADAS DEBEN SER VERIFICADAS EN OBRA