
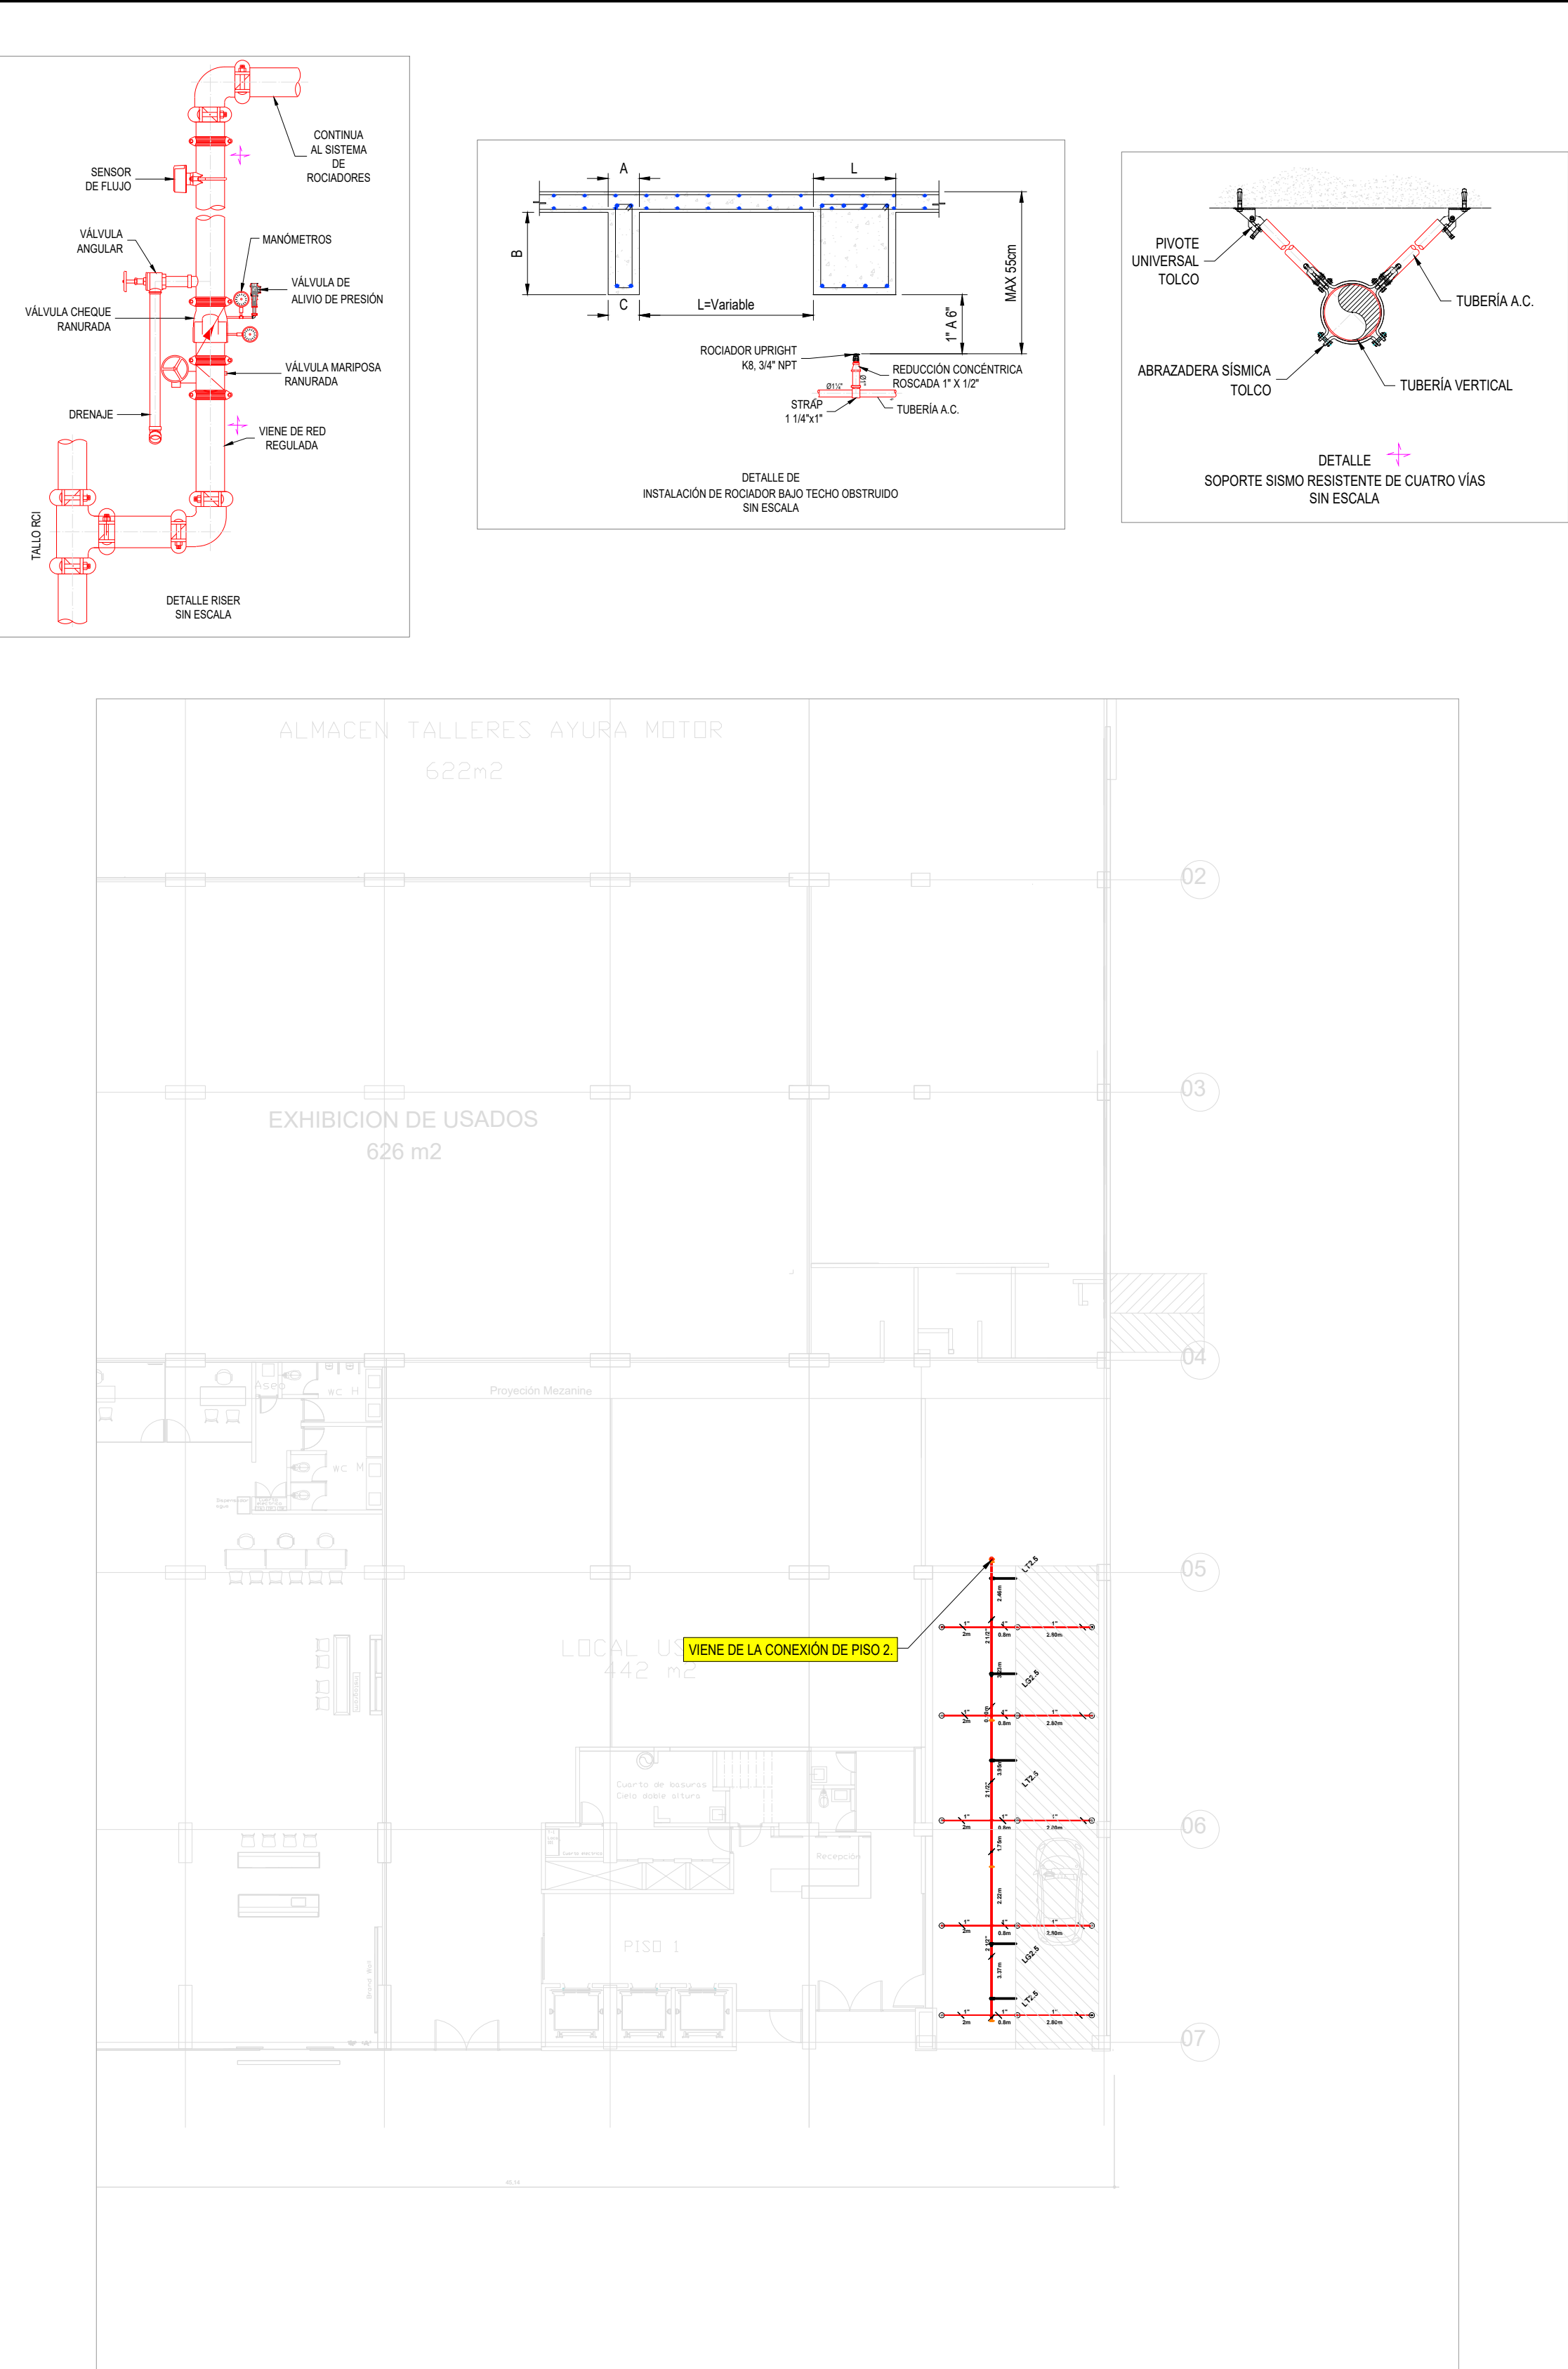


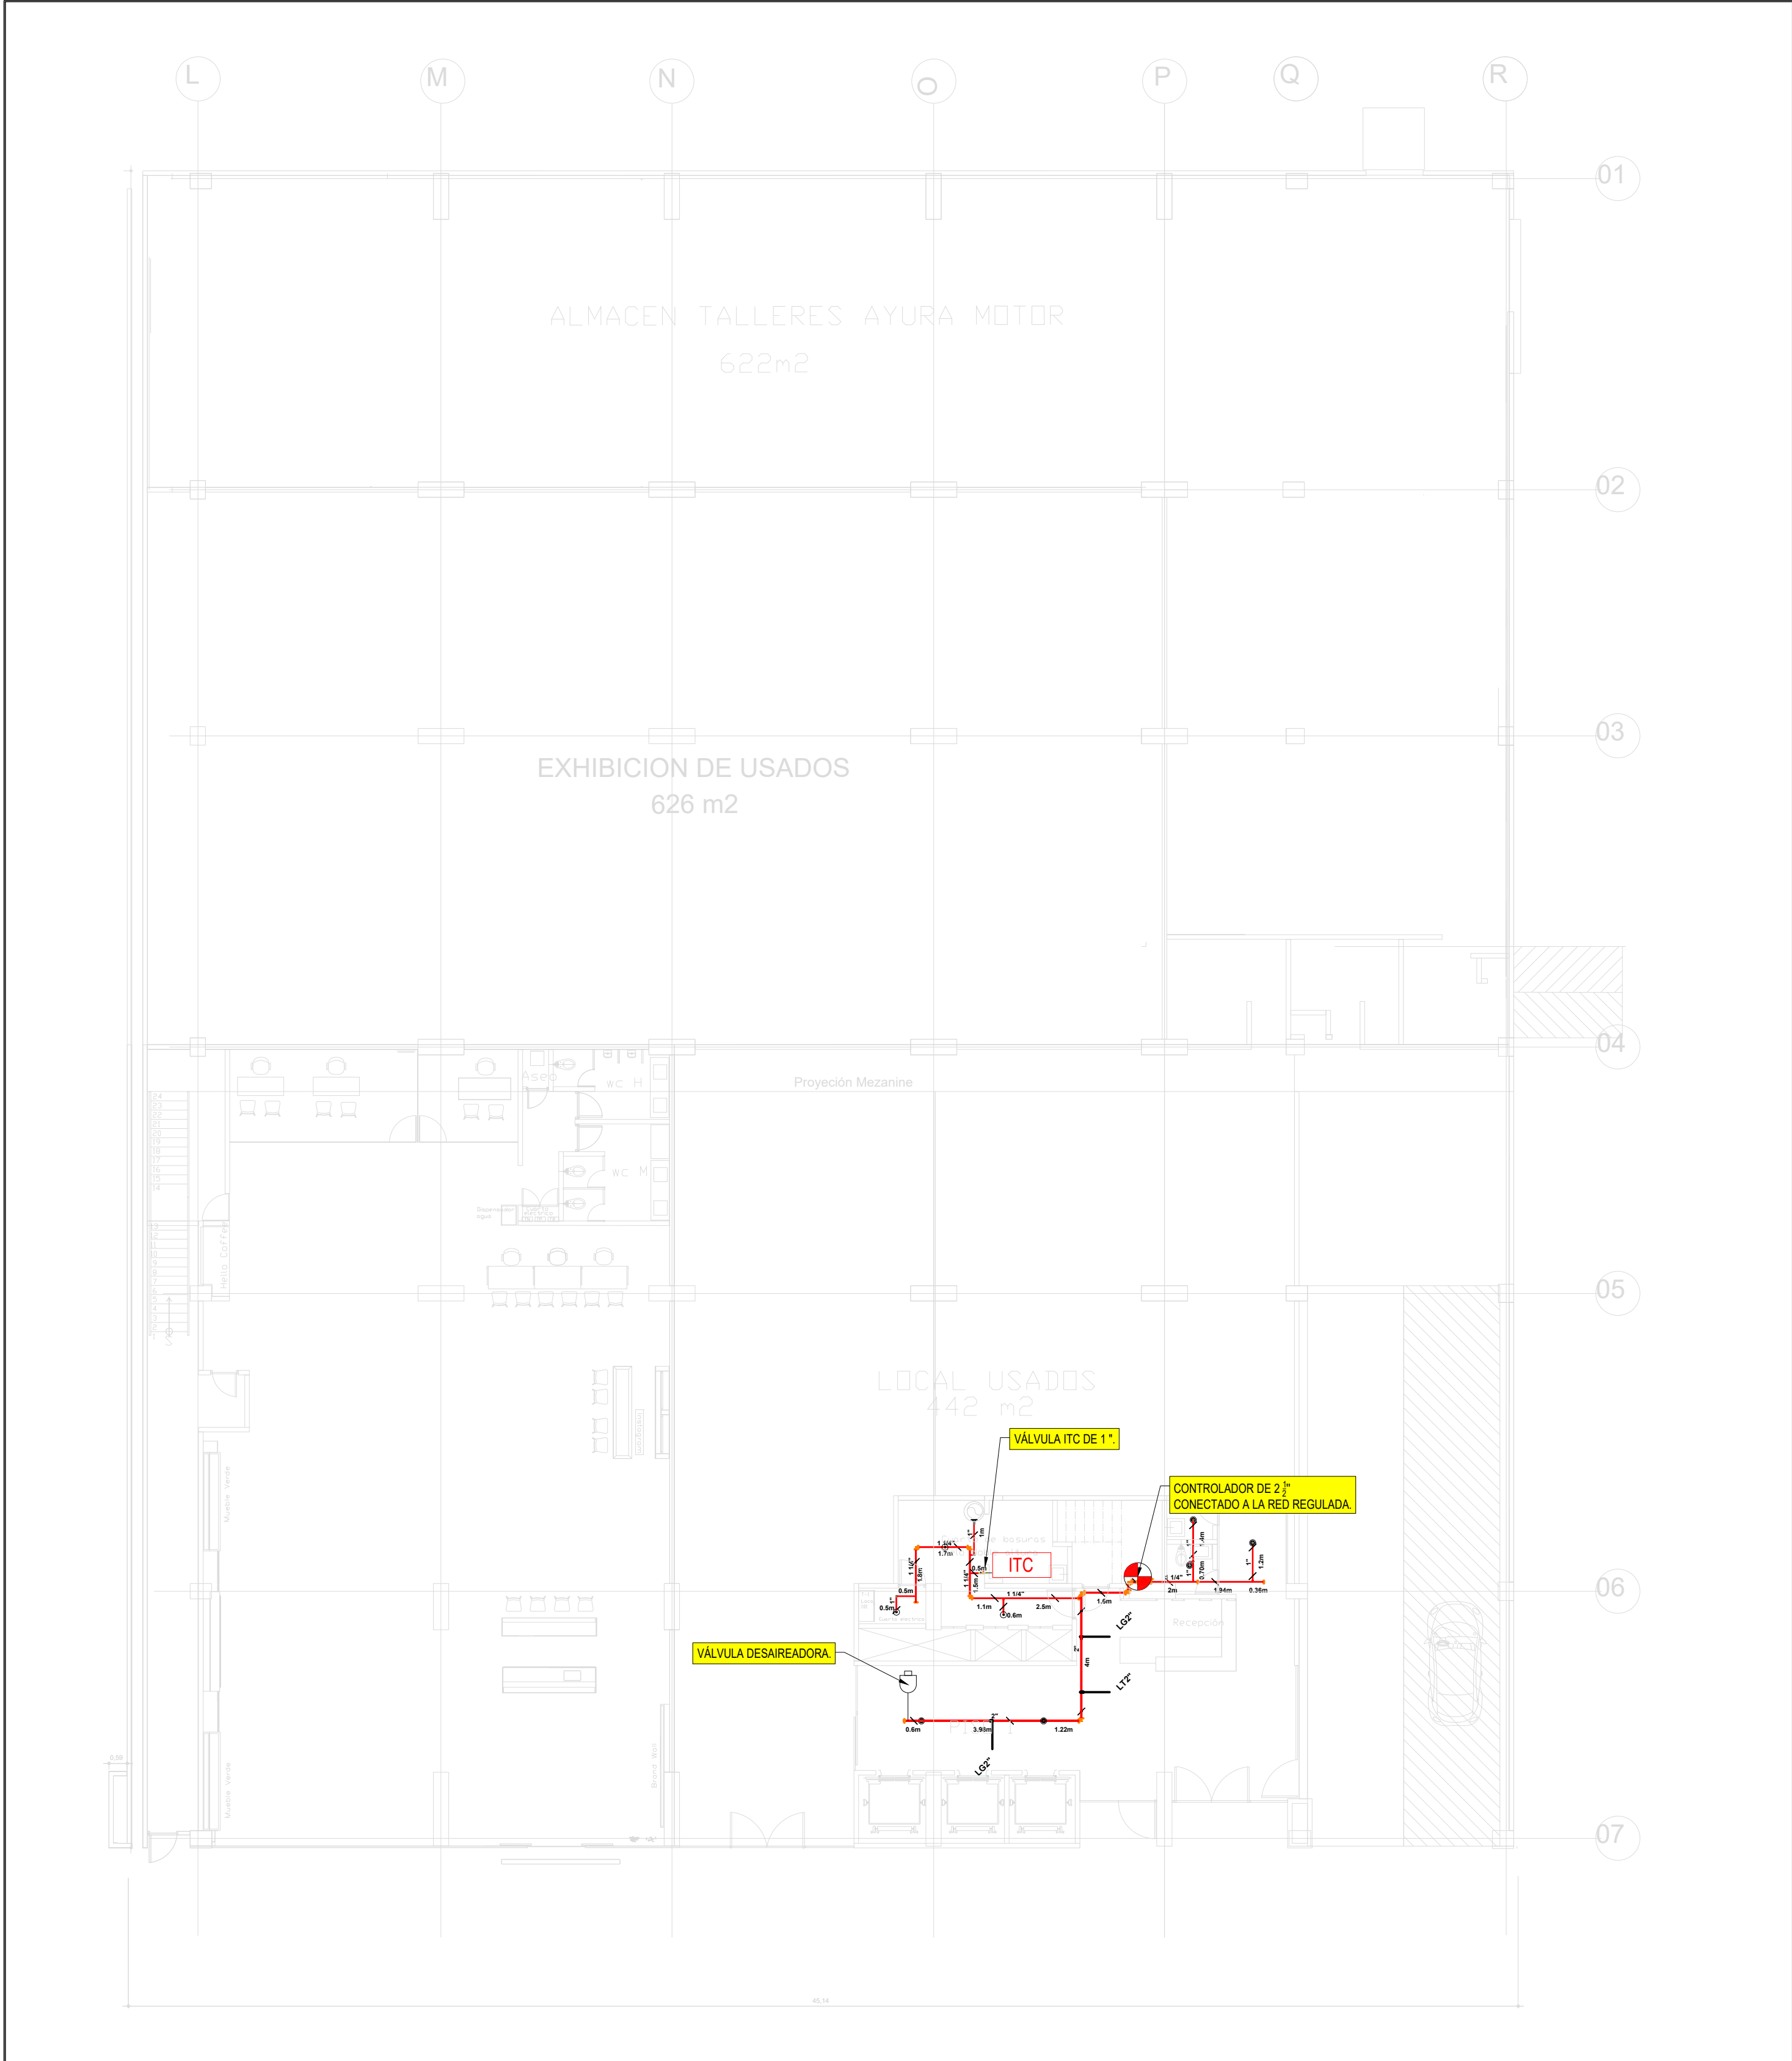

1 VISTA EN PLANTA EXTINCIÓN PISO 1
ESCALA 1:150

Sway Brace Zone Legend

Diameter	Description	Unit Quantity	Quantity	Unit Weight	Cp =	Net Weight
2 1/2"	Pipe, Schedule 40	1.000	1.000	5.77kg/1.25		5.77kg
				Total Net Weight		5.77kg
				Total Load (x 1.15)		6.63kg

Sway Brace Tag

Brace Type	Brace Pipe Size	Fastener Type	Fastener Orientation
Longitudinal	4"	Anchor (UL717) Hook Bolt 1/2 (C8)	WPA Type "A"
Brace Angle	Attached To	Fastener Size	Maximum Fastener Load
30	Normal Weight Concrete (2000psi)	3/8 x 3	248.5kg

Code: MPPA-B13-2007 Table: 9.3.5.8.1 Plan ID: 1.02.07 Manufacturer: Tolco Inc

DETALLE DE LA SOPORTERIA SISMO RESISTENTE.

Sway Brace Zone Legend					
Diameter	Description	Unit Quantity	Quantity	Unit Weight	Net Weight
2 1/2"	Pipe, Schedule 40	(20.000)	1.000	5.77kg/1	5.77kg
2 1/2"	Pipe, Schedule 40	(20.000)	1.000	5.77kg/1	5.77kg
1"	Pipe, Schedule 40	(20.048)	4.471	3.08kg/1	13.63kg
				Total Net Weight	25.17kg
				Total Load (x 1.15)	28.94kg

Sway Brace Tag					
Brace Type	Brace Pipe Size	Fastener Type	Fastener Orientation		
Longitudinal	4"	Anchor, (UL717) Hook Bolt 1/2 (C8)	WPA Type "A"		
Brace Angle	Attached To	Fastener Size	Maximum Fastener Load		
30	Normal Weight Concrete (2000psi)	3/8 x 3	248.5kg		

Code: MPPA-B13-2007 Table: 9.3.5.8.1 Plan ID: 1.02.07 Manufacturer: Tolco Inc

2 VISTA EN PLANTA EXTINCIÓN PISO 1 BAJO RAMPA
ESCALA 1:200

REGISTRO DE MODIFICACIONES		
MODIF	FECHA	DESCRIPCIÓN
1	--	----
2	--	----
3	--	----
4	--	----

REGISTRO DE REVISIONES		
REV.	FECHA	EMITIDO PARA:
0	24-06-2024	ACTUALIZACION
1	18-02-2025	ACTUALIZACION
2	--	----
3	--	----
4	--	----
5	--	----
6	--	----

CARACTERÍSTICAS ROCIADORES				
ORIENTACIÓN	K	ROSCA	TEMPERATURA RESPUESTA	COBERTURA
UPRIGHT	8	3/4"	68°C	RAPIDA Estandar

CARACTERÍSTICAS ROCIADORES				
ORIENTACIÓN	K	ROSCA	TEMPERATURA RESPUESTA	COBERTURA
PENDENT	5.6	1/2"	68°C	RAPIDA Estandar

CONVENCIONES	
	TUBERÍA EXPUESTA
	TUBERÍA ENTERRADA
	TUBERÍA POR CÁRCAMO
	TUBERÍA CPVC
	UNIÓN RANURADA
	CODO 90° RANURADO
	TEE RANURADA
	HIDRANTE CONTRA INCENDIO
	ESTACION DE MANGUERA SISTEMA HUMEDO
	RISER (SISTEMA CONTROLADOR)
	SIAMESA CONEXION PARA BOMBEROS 4"x2 1/2"x2 1/2"
	NODO HIDRAULICO
	ÁREA DE DISEÑO
	SOPORTE COLGANTE
	SOPORTE SISMICO CUATRO VÍAS
	SOPORTE SISMO RESISTENTE LONGITUDINAL
	SOPORTE SISMO RESISTENTE LATERAL
	BLOQUE DE EMPUJE
	VÁLVULA DE INSPECCIÓN, PRUEBA Y DRENAJE
	VÁLVULA DESAIREADORA
	FUTURA CONEXIÓN
	UNIÓN SISMICA
	ESTACION DE MANGUERA CLASE II

ELABORADO POR:

ELABORADO PARA:

AYURA MOTORS ETAPA 3

ENVIGADO-ANTIOQUIA

PROYECTO:

SISTEMA DE EXTINCIÓN DE INCENDIOS

CONTIENE:

ROCIADORES PISO 1

ELABORÓ:	DAVID ORTIZ	REVISÓ:	
MODELO:	DAVID ORTIZ	UNIDADES:	Metros
FECHA:	01-03-2024	ESCALA:	INDICADAS
VERSIÓN:	04	VERS. MOD:	04
FORMATO:	A1		

PROYECTO No: GL 706

PLANO No. PLANO 1 de 12

NOTAS:

- LAS LONGITUDES SE INDICAN EN METROS Y LOS DIÁMETROS EN PULGADAS
ESTE DOCUMENTO CORRESPONDE A UN PLANO DE DISEÑO, LAS DIMENSIONES INDICADAS DEBEN SER VERIFICADAS EN OBRA