

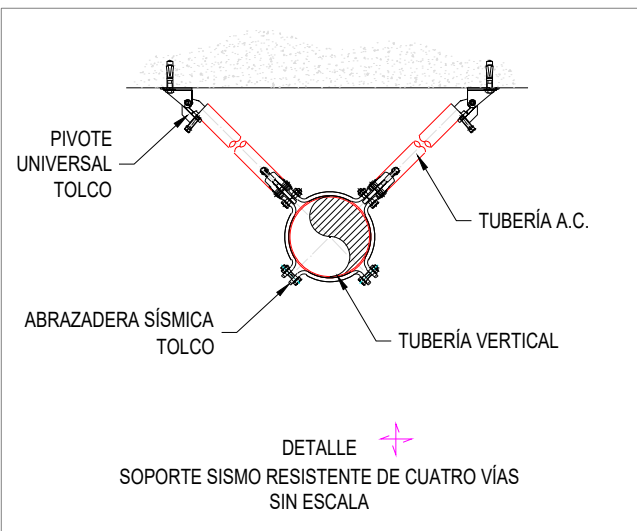
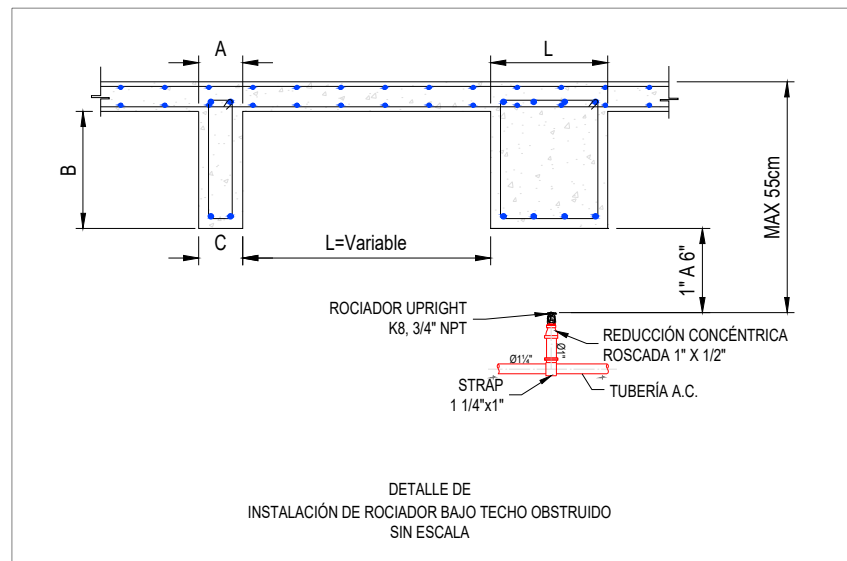
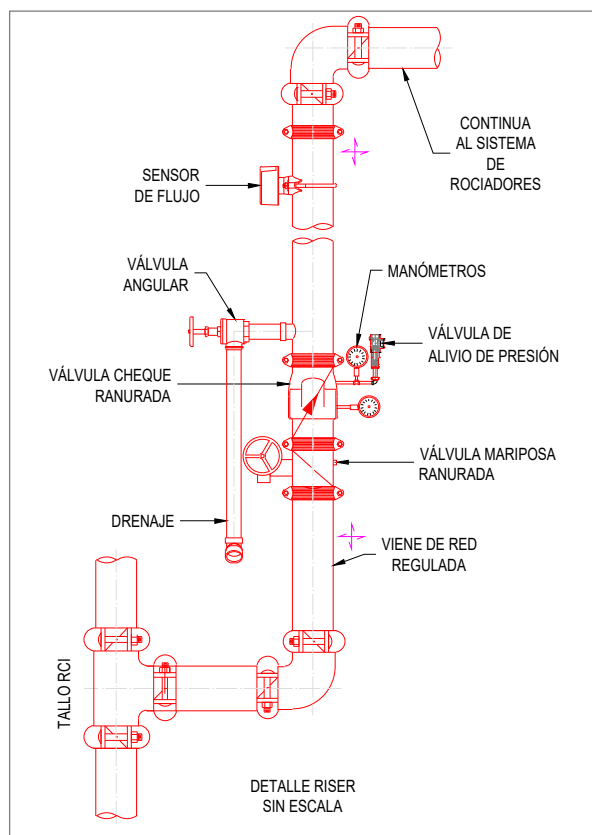
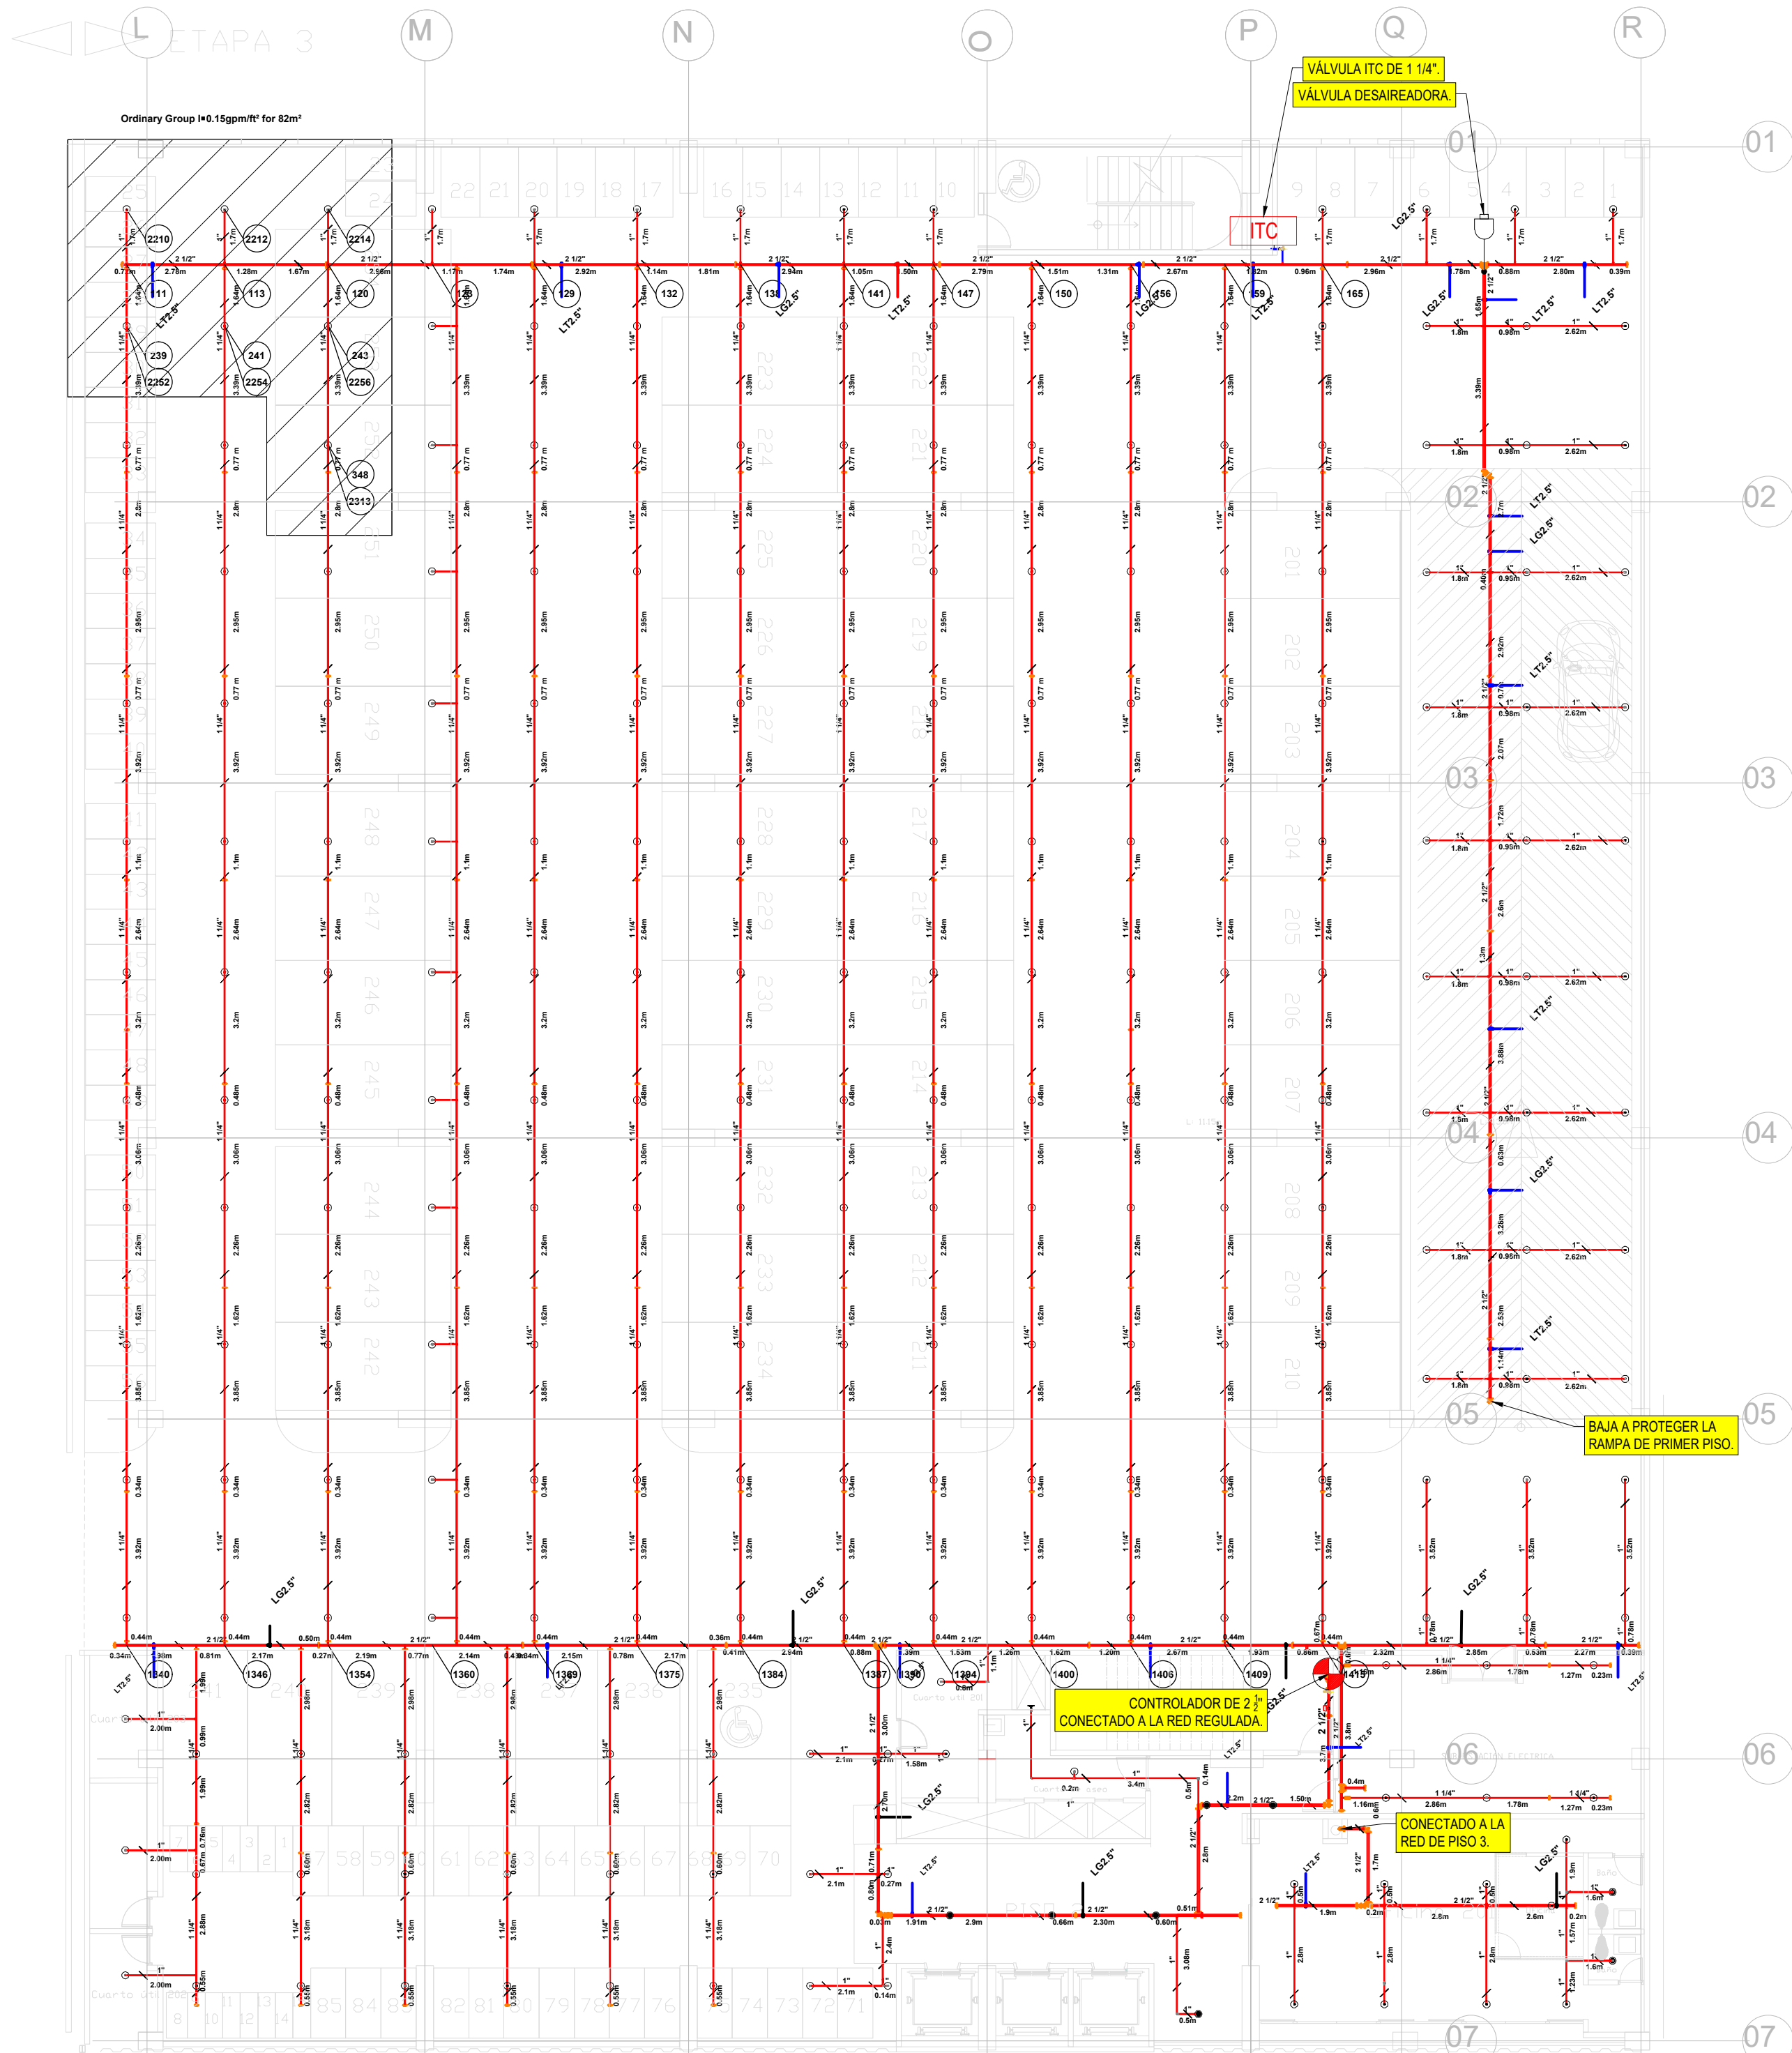
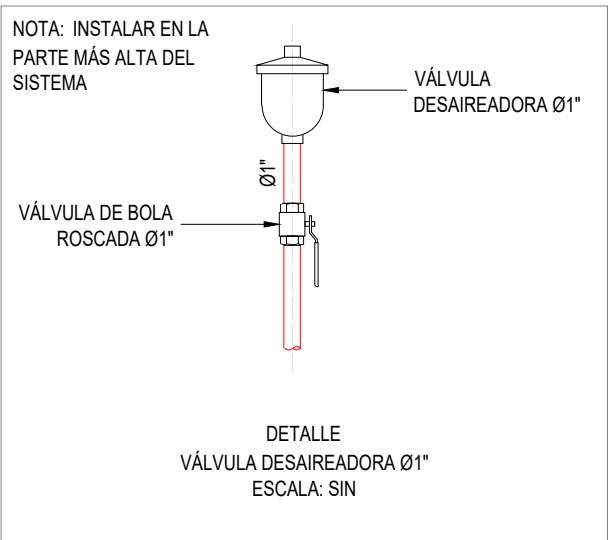


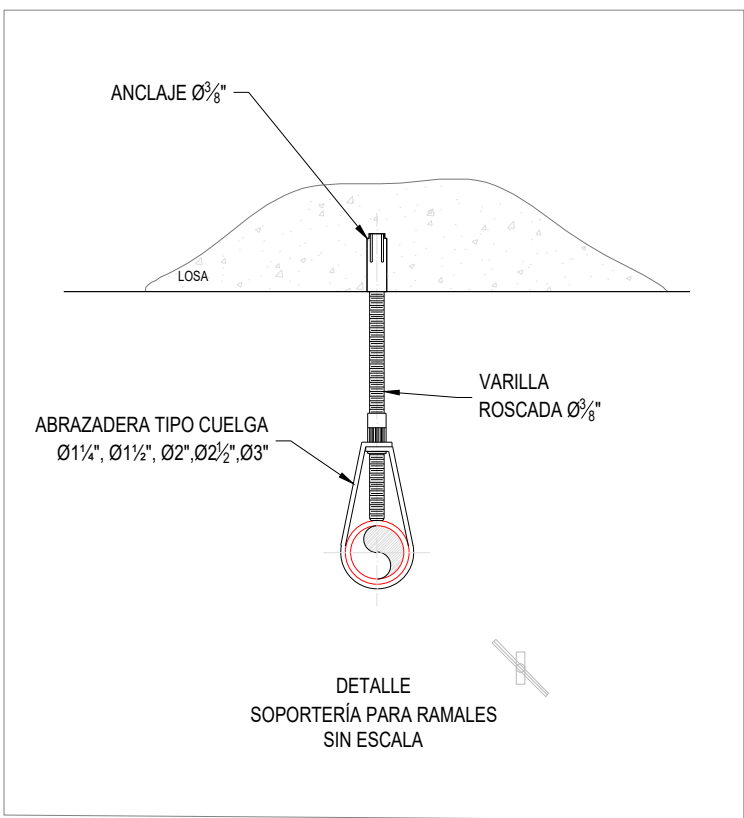

Riser Tag	
Design Basis	Ordinary Group I
Occupancy	847
Total Sprinklers	7
Number of Sprinklers Calculated	8
K-Factor	8
Orifice Size	0.631"
Design Density	0.15 gpm/ft ²
Average Density	0.17 gpm/ft ²
Area of Application	139m ² (Actual 82m ²)
Demand at Base of Riser at Point Of Connection	
Total Demand Flow(gpm)	152.33
Pressure(gpi)	24.76
Water Supply Information At Time Of Design	
Static Pressure(gpi)	228.000
Residual Pressure(gpi)	216.000
Supply Flow(gpm)	788.50
Total Demand Flow(gpm)	282.33
Total Demand Pressure(gpi)	61.799
Safety Margin(gpi)	187.244

Hydraulic Information	
OCCUPANCY CLASSIFICATION	Ordinary Group I
DENSITY (gpm/ft ²)	0.15 for 139m ² (Actual 82m ²)
TOTAL ROSE STREAMS	8
DRY CAPACITY	0.09gal
TOTAL DEMAND FLOWING	17
K-FACTOR	8
TOTAL WATER REQUIRED	282.33
TOTAL PRESSURE REQUIRED	61.799
BASE OF RISER (gpi)	282.33
SAFETY MARGIN (gpi)	187.244 (71.8%)

RESUMEN DEL CALCULO HIDRAULICO

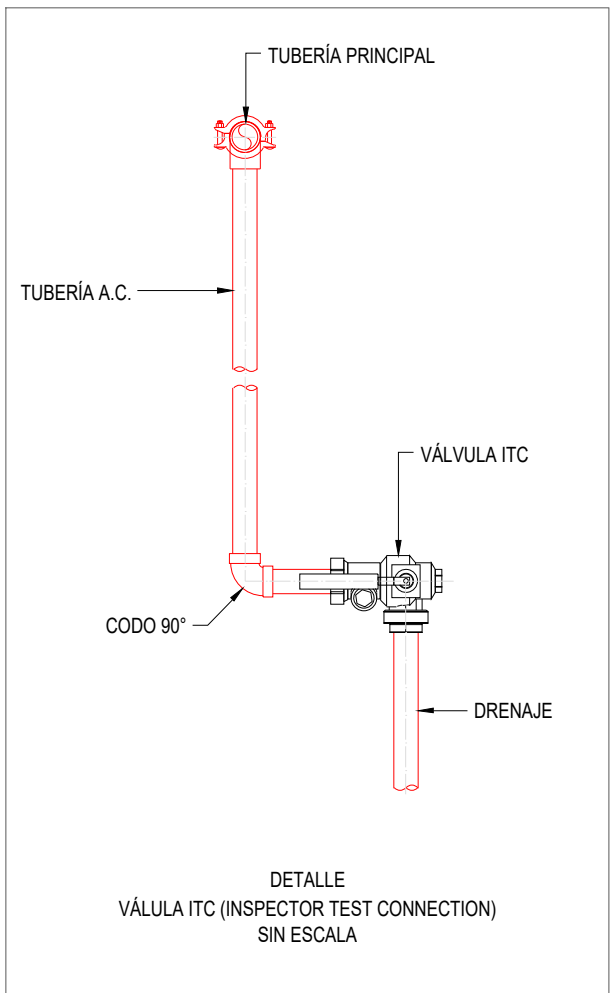

3 VISTA EN PLANTA EXTINCIÓN PISO 2

ESCALA 1:150

Sway Brace Zone Legend					
Diameter	Description	Unit Quantity	Quantity	Unit Weight	Net Weight
1.6	Pipe, Schedule 10	(218.800)	12.000	3.76kg/m	53.16kg
2.0	Pipe, Schedule 10	(218.800)	11.000	6.77kg/m	148.07kg
2.5	Pipe, Schedule 40	(218.800)	4.000	23.66kg/m	94.64kg
Total Net Weight					295.87kg
Total Load (x 1.15)					340.25kg

Sway Brace Zone Legend					
Diameter	Description	Unit Quantity	Quantity	Unit Weight	Net Weight
1.6	Pipe, Schedule 10	(218.800)	11.000	3.76kg/m	53.16kg
2.0	Pipe, Schedule 10	(218.800)	11.000	6.77kg/m	148.07kg
2.5	Pipe, Schedule 40	(218.800)	4.000	23.66kg/m	94.64kg
Total Net Weight					295.87kg
Total Load (x 1.15)					340.25kg


DETALLE DE LA SOPORTERIA SISMO RESISTENTE.

REGISTRO DE MODIFICACIONES		
MODIF.	FECHA	DESCRIPCIÓN
1	--	----
2	--	----
3	--	----
4	--	----

REGISTRO DE REVISIONES		
REV.	FECHA	EMITIDO PARA:
0	24-06-2024	ACTUALIZACION
1	18-02-2025	ACTUALIZACION
2	--	----
3	--	----
4	--	----
5	--	----
6	--	----

CARACTERÍSTICAS ROCIADORES				
ORIENTACIÓN	K	ROSCA	TEMPERATURA RESPUESTA	COBERTURA
UPRIGHT	8	3/4"	68°C	RAPIDA
PENDENT	8	3/4"	68°C	RAPIDA

CONVENCIONES	
	TUBERÍA EXPUESTA
	TUBERÍA ENTERRADA
	TUBERÍA POR CÁRCAMO
	TUBERÍA CPVC
	UNIÓN RANURADA
	CODO 90° RANURADO
	TEE RANURADA
	HIDRANTE CONTRA INCENDIO
	ESTACION DE MANGUERA SISTEMA HUMEDO
	RISER (SISTEMA CONTROLADOR)
	SIEMESA CONEXION PARA BOMBEROS 4"x2 1/2"x2 1/2"
	NODO HIDRAULICO
	ÁREA DE DISEÑO
	SOPORTE COLGANTE
	SOPORTE SISMICO CUATRO VIAS
	SOPORTE SISMO RESISTENTE LONGITUDINAL
	SOPORTE SISMO RESISTENTE LATERAL
	BLOQUE DE EMPUJE
	VÁLVULA DE INSPECCIÓN, PRUEBA Y DRENAJE
	VÁLVULA DESAIREADORA
	FUTURA CONEXIÓN
	UNIÓN SISMICA
	ESTACION DE MANGUERA CLASE II

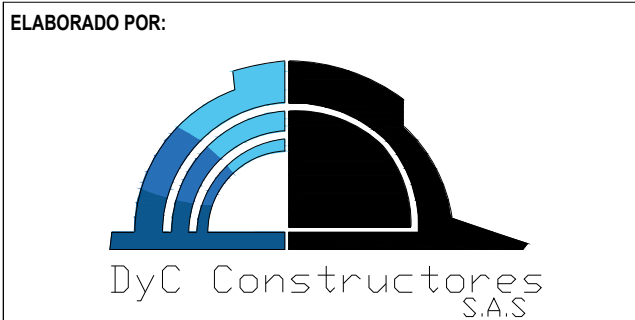

ELABORADO PARA:
AYURA MOTORS ETAPA 3
ENVIADO-ANTIOQUIA

PROYECTO:
SISTEMA DE EXTINCIÓN DE INCENDIOS
CONTIENE:
ROCIADORES
PISO 2
ELABORÓ:
MODELO:
FECHA: 14-11-2025
VERSIÓN: 05
PLANO No. 3 de 12
REVISÓ:
UNIDADES: Metros
ESCALA: INDICADAS
FORMATO: A1

NOTAS:
- LAS LONGITUDES SE INDICAN EN METROS Y LOS DIÁMETROS EN PULGADAS
ESTE DOCUMENTO CORRESPONDE A UN PLANO DE DISEÑO. LAS DIMENSIONES INDICADAS DEBEN SER VERIFICADAS EN OBRA.