

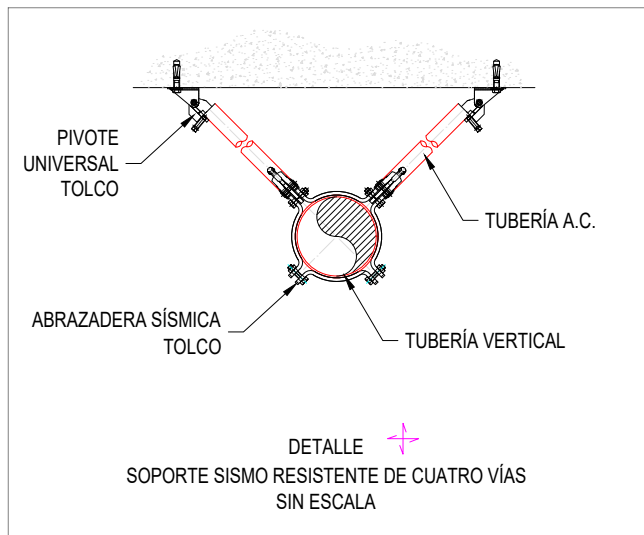
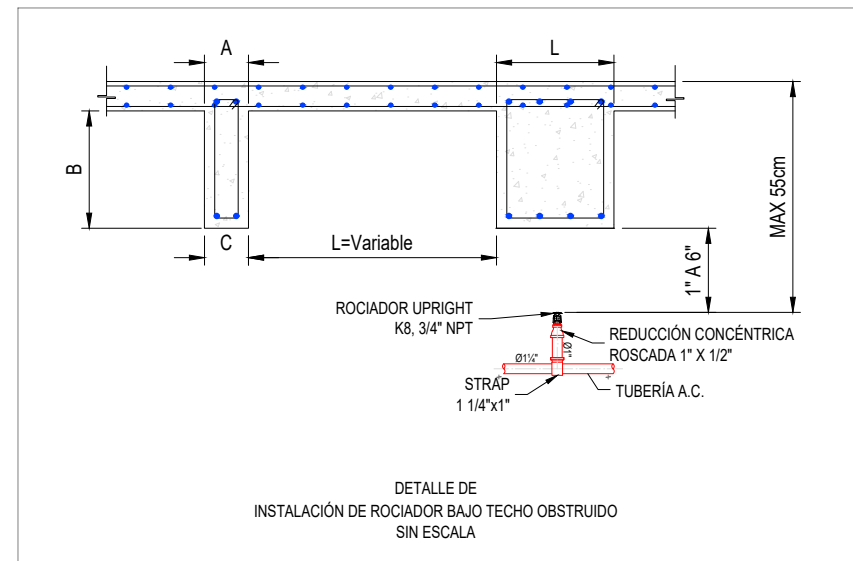
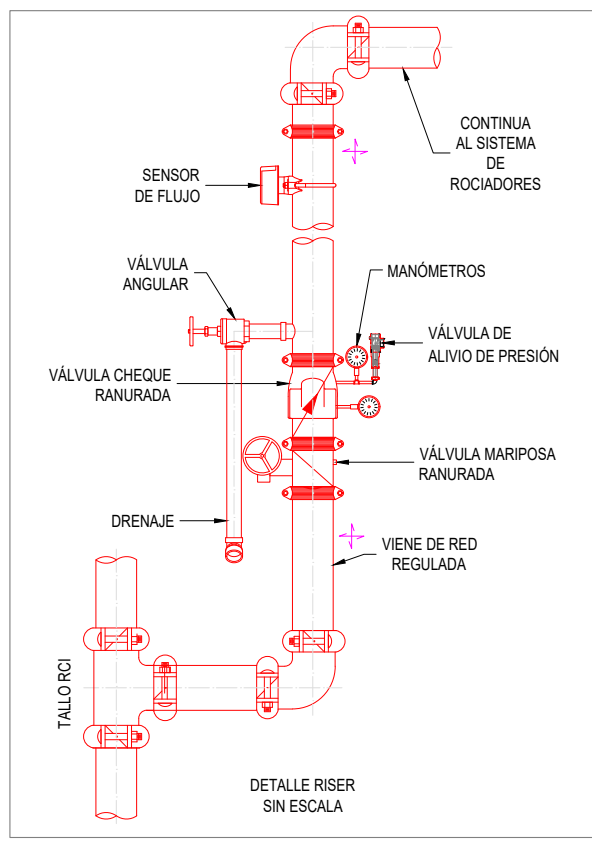
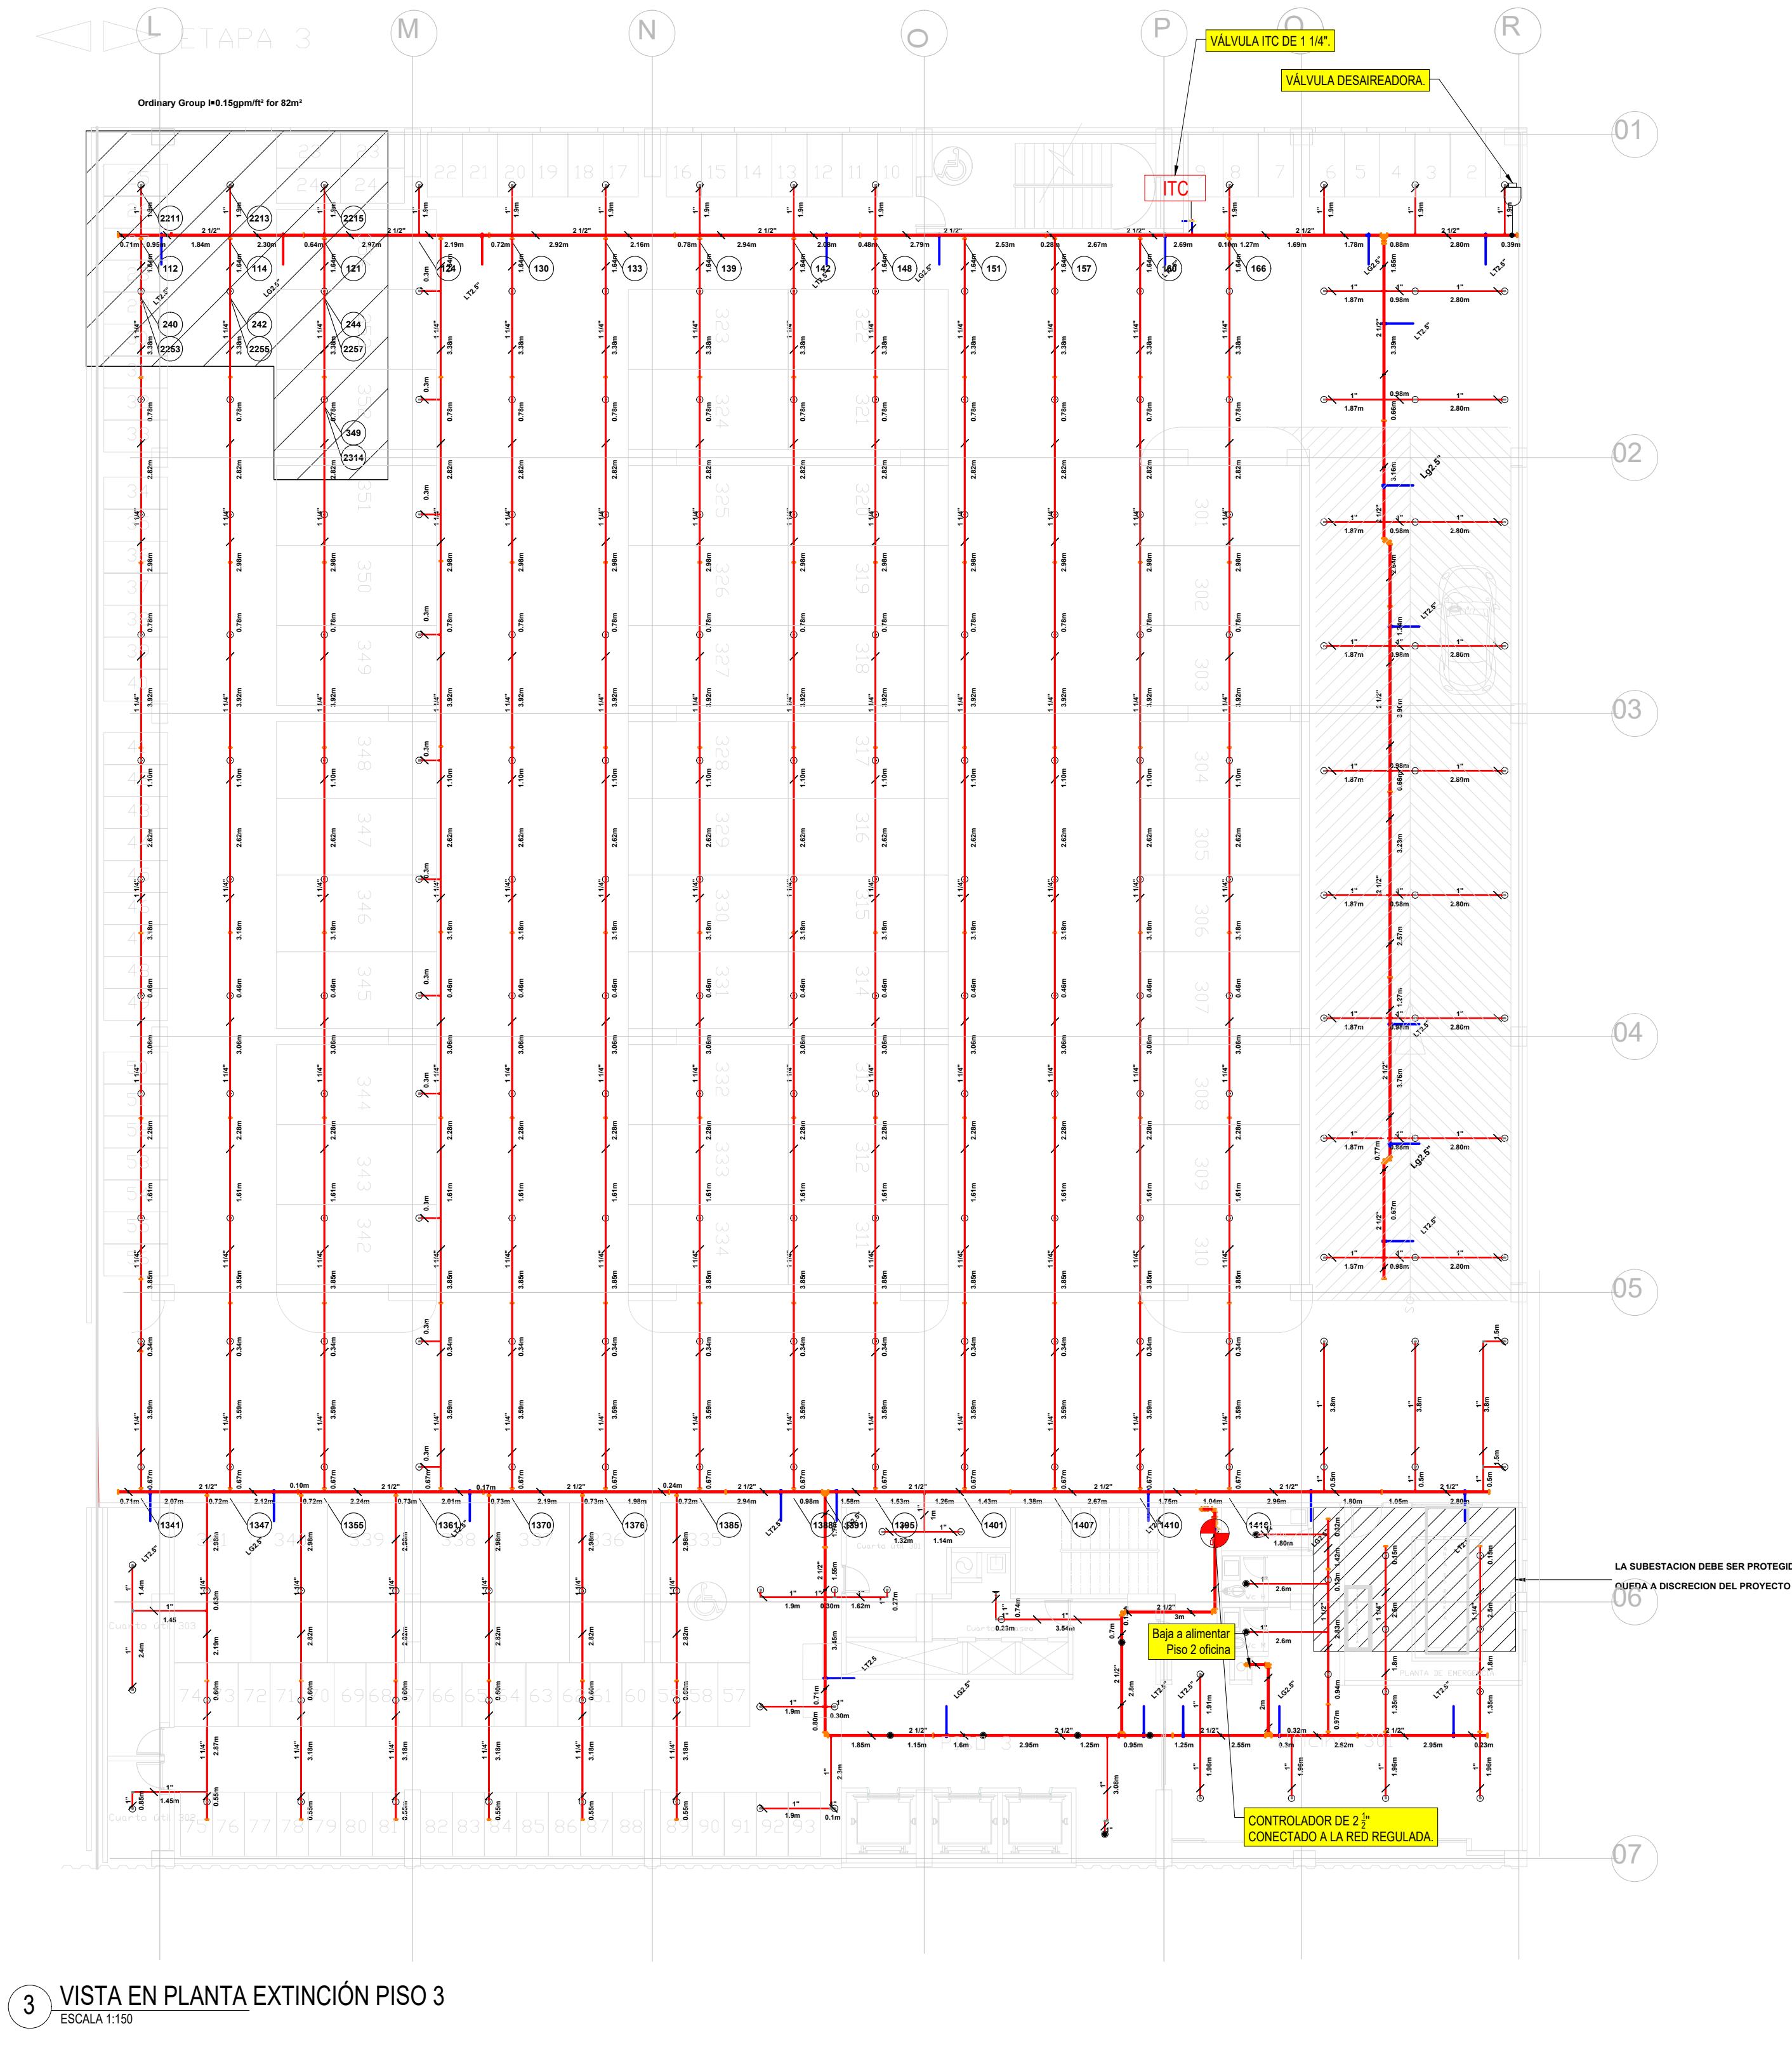
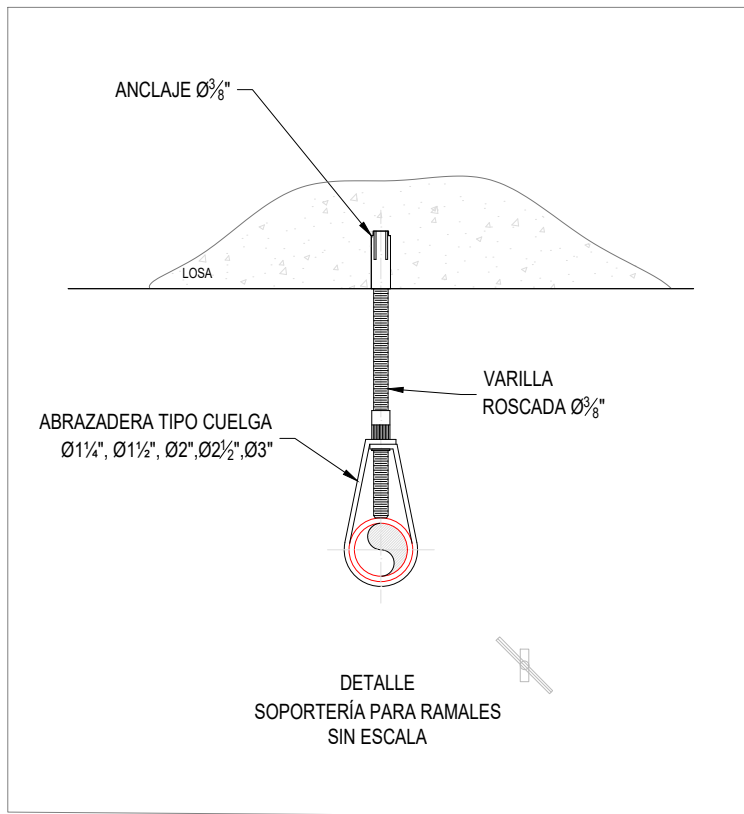
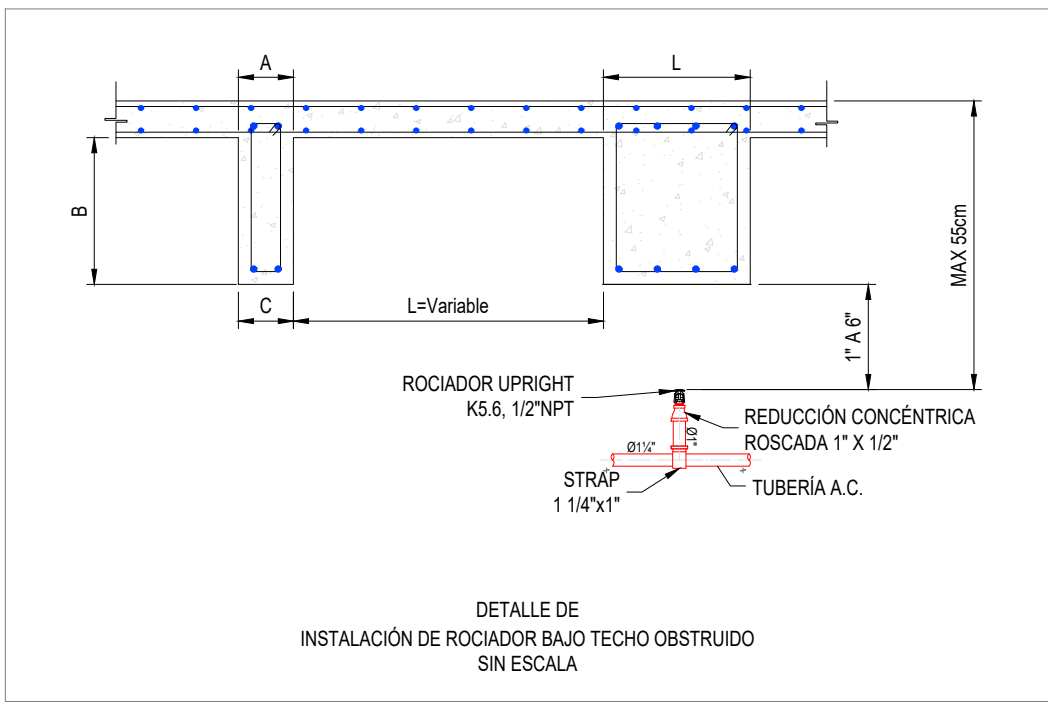


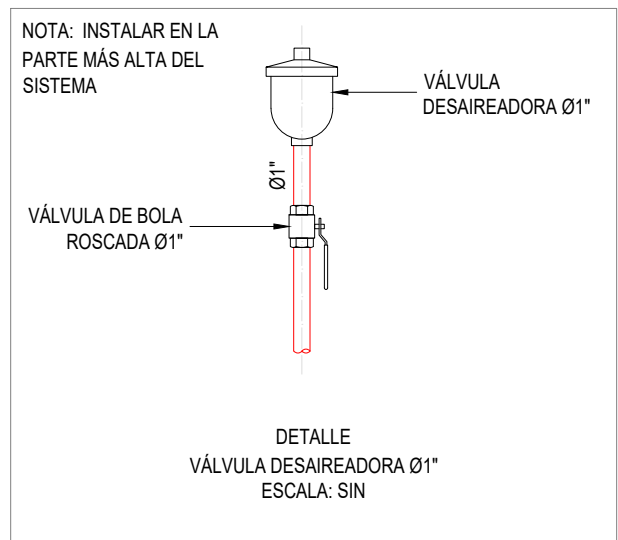

RESUMEN DEL CALCULO HIDRAULICO

Riser Tag	
Design Basis	Ordinary Group I
Occupancy:	947
Total Sprinklers:	7
Number Of Sprinklers Calculated:	8
K-Factor:	6
Orifice Size:	0.631"
Design Density:	0.15gpm/ft ²
Average Density:	0.17gpm/ft ²
Area of Application:	139m ² (Actual 82m ²)
Demand at Base Of Riser or Point Of Connection	
Total Demand Flow(gpm):	162.33
Pressure(psi):	24.478
Water Supply Information At Time Of Design	
Static Pressure(psi):	220.000
Residual Pressure(psi):	210.000
Supply Flow(gpm):	750.00
Total Demand Flow(gpm):	202.33
Total Demand Pressure(psi):	61.790
Safety Margin(psi):	157.324

Hydraulic Information	
OCCUPANCY CLASSIFICATION	Ordinary Group I
DENSITY (gpm/ft ²)	0.15 for 139m ² (Actual 82m ²)
TOTAL HOSE STREAMS	60.00
DRY CAPACITY	6.00gal
TOTAL HEADS FLOWING	7
K-FACTOR	6
TOTAL WATER REQUIRED	202.33
TOTAL PRESSURE REQUIRED	61.790
BASE OF RISER (gpm)	202.33
BASE OF RISER (psi)	61.790
SAFETY MARGIN (psi)	+157.324 (11.8%)

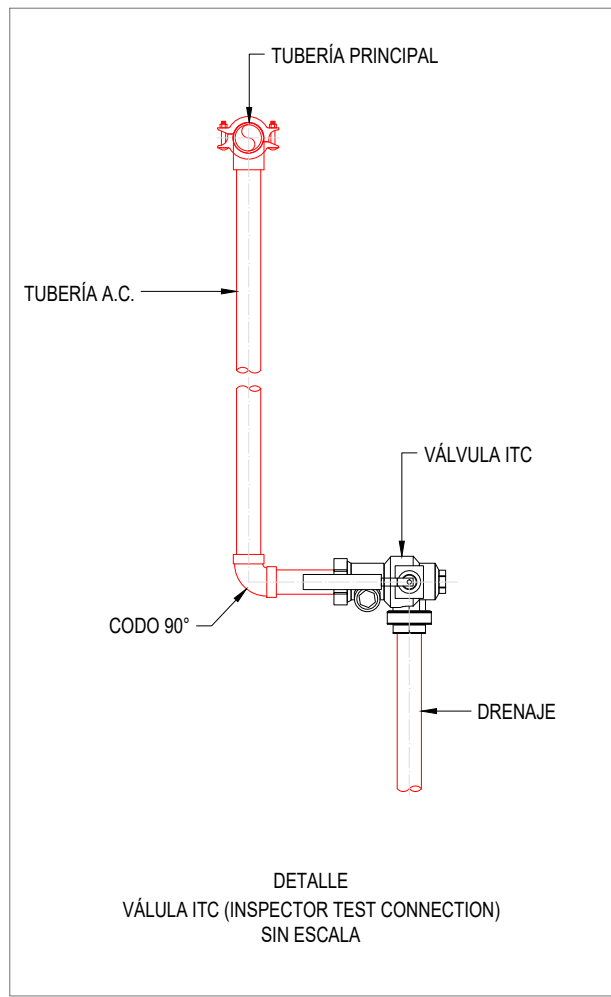

REGISTRO DE MODIFICACIONES		
MODIF.	FECHA	DESCRIPCIÓN
Δ	--	----
Δ	--	----
Δ	--	----
Δ	--	----

REGISTRO DE REVISIONES		
REV.	FECHA	EMITIDO PARA:
0	24-06-2024	ACTUALIZACION
1	18-02-2025	ACTUALIZACION
2	--	----
3	--	----
4	--	----
5	--	----
6	--	----

CARACTERÍSTICAS ROCIADORES			
ORIENTACIÓN	K	ROSCA TEMPERATURA RESPUESTA	COBERTURA
UPRIGHT	8	3/4"	68°C
		RAPIDA	ESTANDAR

CARACTERÍSTICAS ROCIADORES			
ORIENTACIÓN	K	ROSCA TEMPERATURA RESPUESTA	COBERTURA
PENDENT	8	3/4"	68°C
		RAPIDA	ESTANDAR

CONVENCIONES	
	TUBERÍA EXPUESTA
	TUBERÍA ENTERRADA
	TUBERÍA POR CÁRCAMO
	TUBERÍA CPVC
	UNIÓN RANURADA
	CODO 90° RANURADO
	TEE RANURADA
	HIDRANTE CONTRA INCENDIO
	ESTACION DE MANGUERA SISTEMA HUMEDO
	RISER (SISTEMA CONTROLADOR)
	SIAMESA CONEXION PARA BOMBEROS 4"x2 1/2"x2 1/2"
	NODO HIDRAULICO
	ÁREA DE DISEÑO
	SOPORTE COLGANTE
	SOPORTE SÍSMICO CUATRO VÍAS
	SOPORTE SISMO RESISTENTE LONGITUDINAL
	SOPORTE SISMO RESISTENTE LATERAL
	BLOQUE DE EMPUJE
	VÁLVULA DE INSPECCIÓN, PRUEBA Y DRENAJE
	VÁLVULA DESAIREADORA
	FUTURA CONEXIÓN
	UNIÓN SÍSMICA
	ESTACION DE MANGUERA CLASE II

ELABORADO POR:

ELABORADO PARA:

AYURA MOTORS ETAPA 3

ENVIGADO-ANTIOQUIA

PROYECTO:

SISTEMA DE EXTINCIÓN DE INCENDIOS

CONTIENE:

ROCIADORES PISO 3

ELABORÓ:

REVISÓ:

MODELO:

UNIDADES: Metros

FECHA:

14-11-2025

ESCALA: INDICADAS

VERSIÓN: 05

VERS. MOD: 05

FORMATO: A1

PROYECTO No: GL 706

PLANO No. PLANO 4 de 12

NOTAS:

- LAS LONGITUDES SE INDICAN EN METROS Y LOS DIÁMETROS EN PULGADAS

- ESTE DOCUMENTO CORRESPONDE A UN PLANO DE DISEÑO. LAS DIMENSIONES INDICADAS DEBEN SER VERIFICADAS EN OBRA