

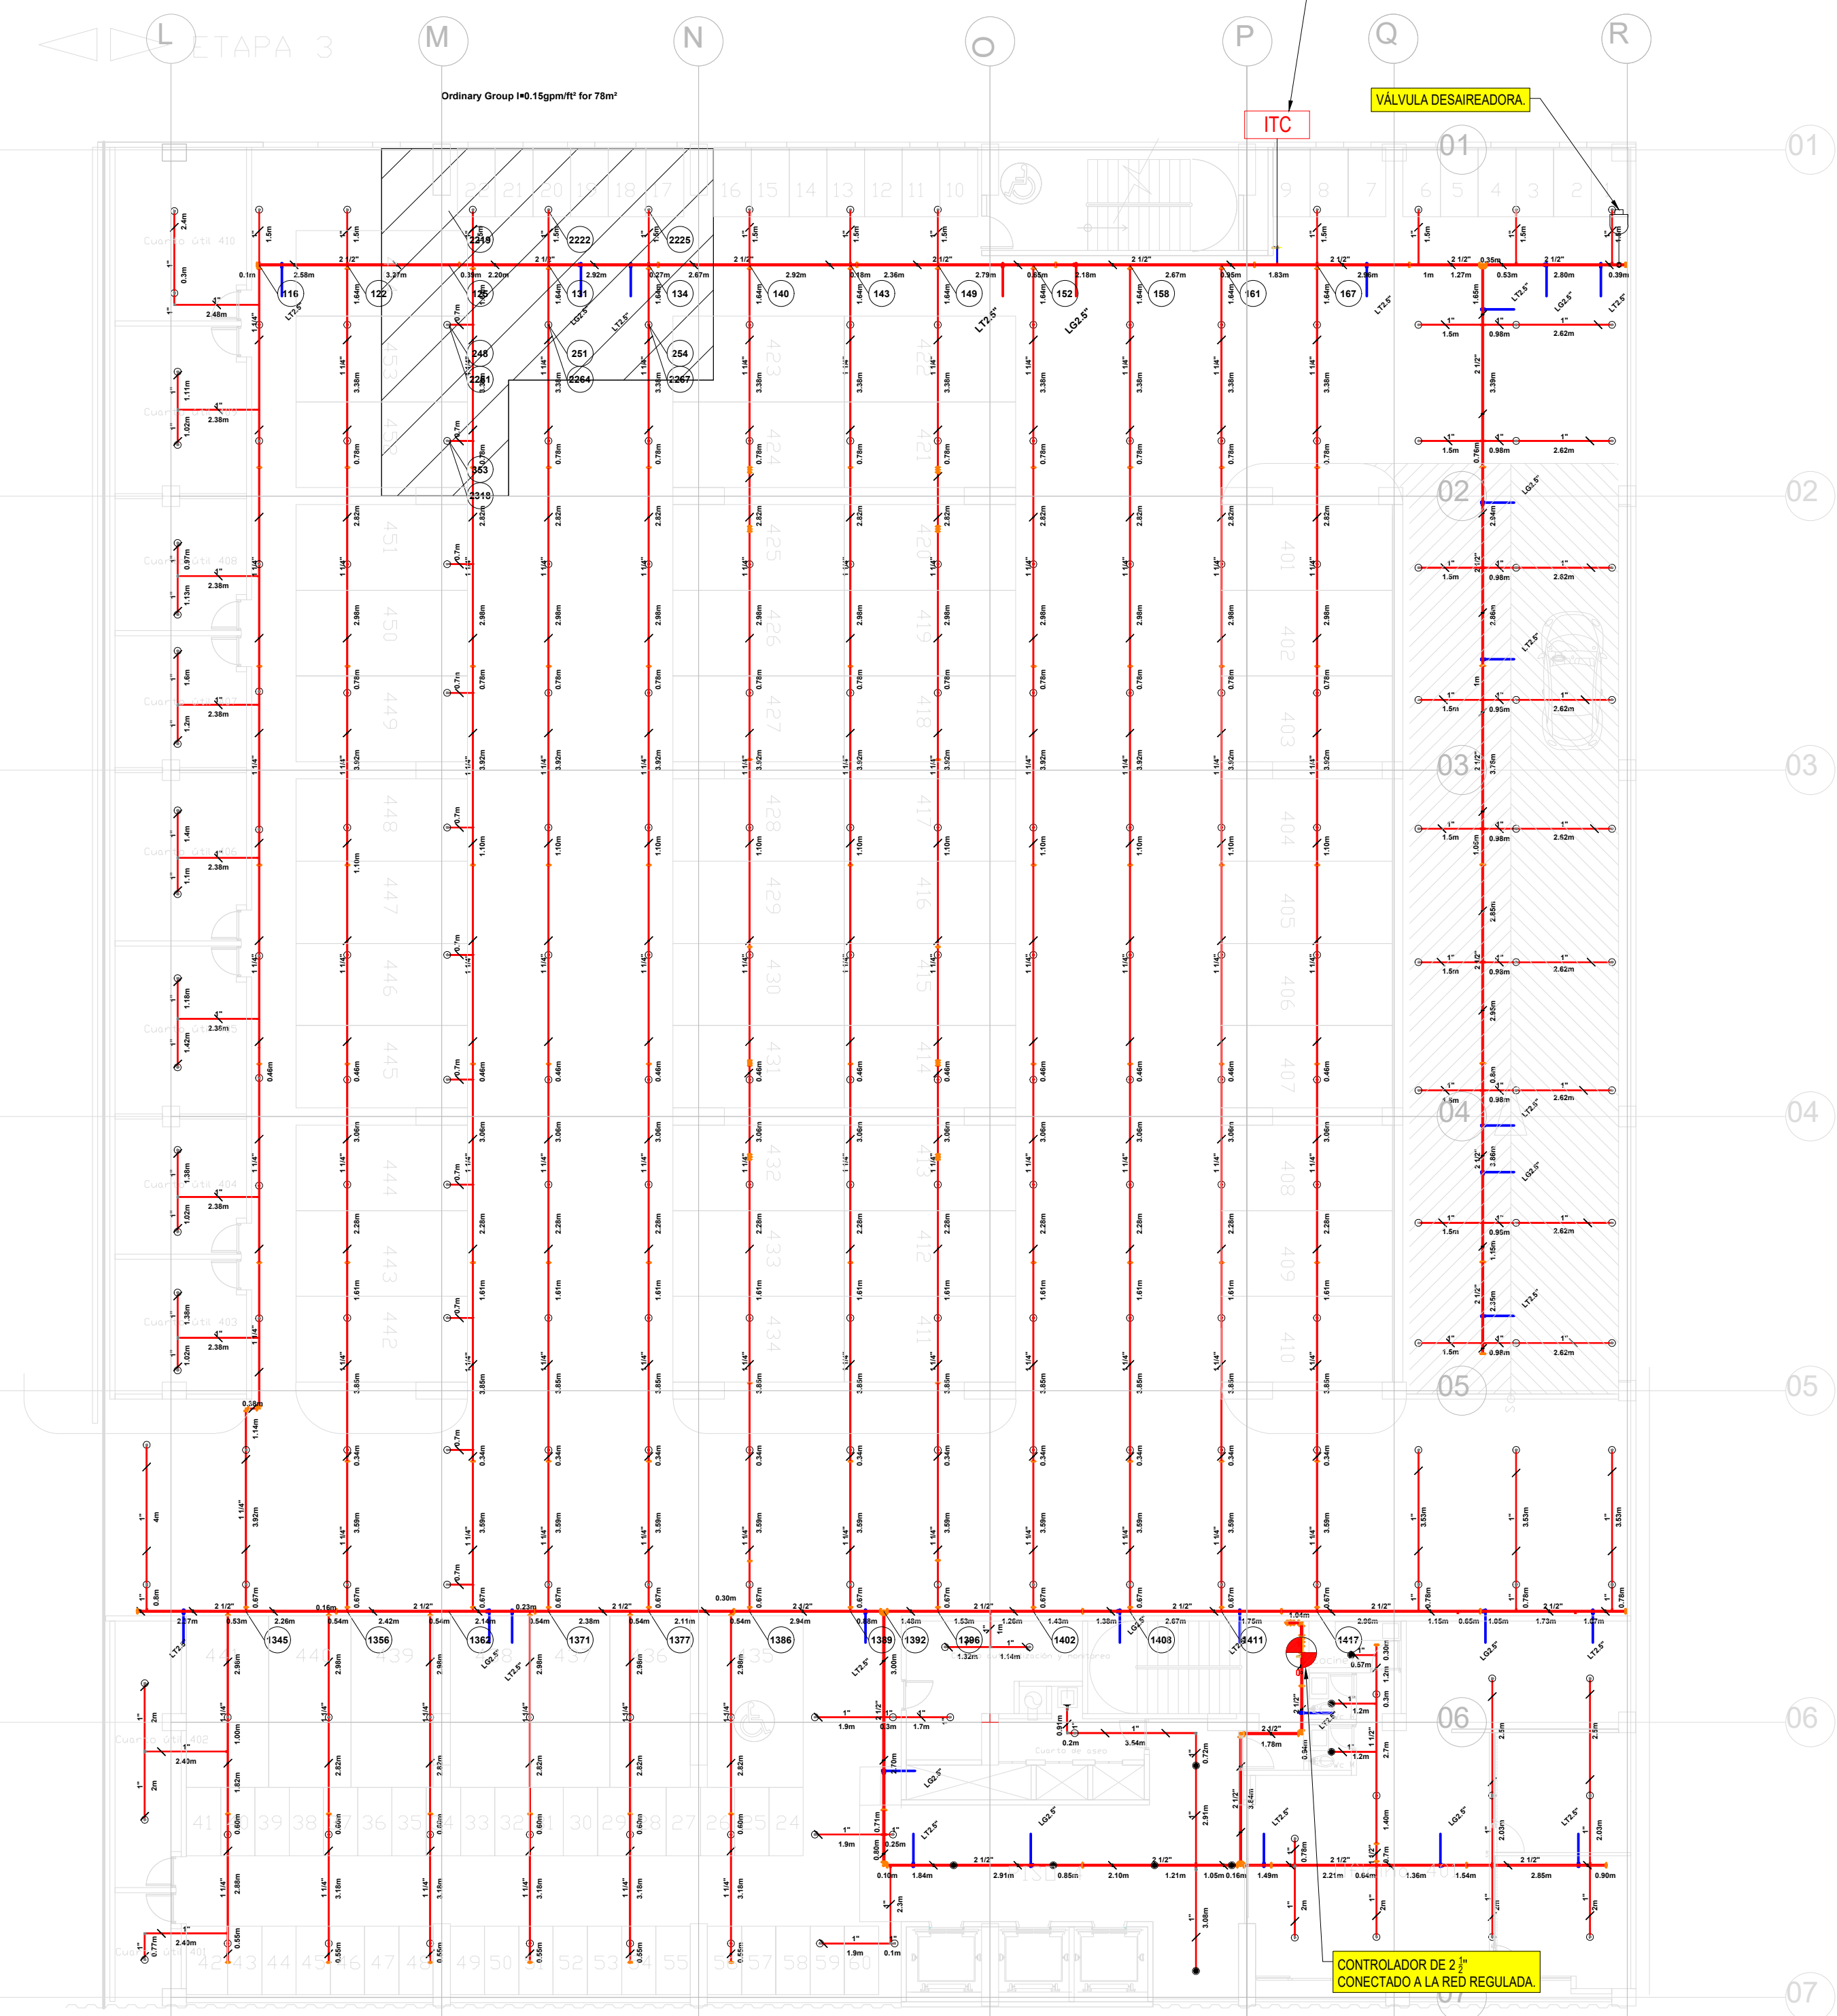
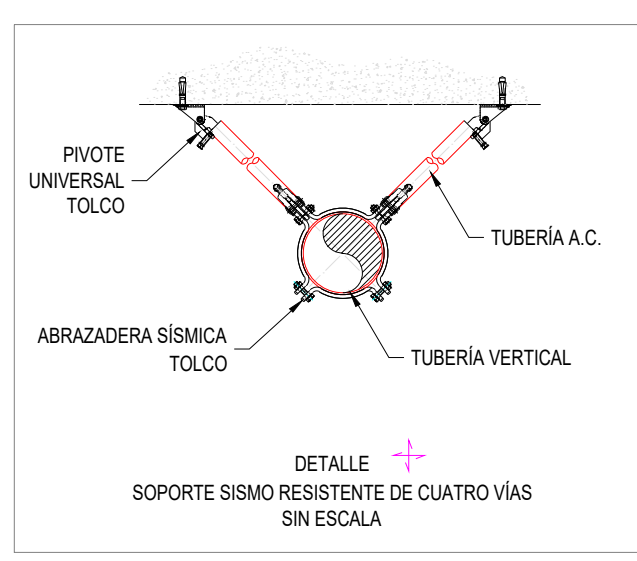


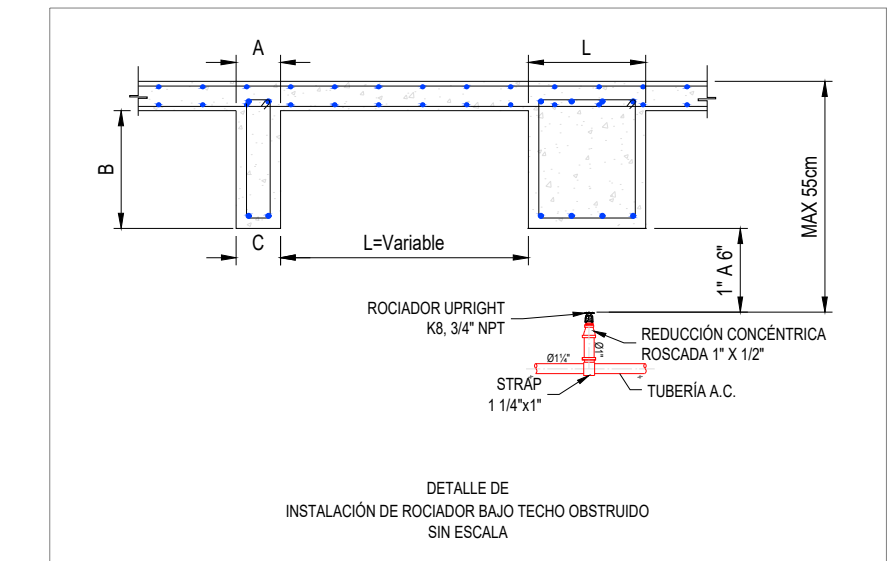





1 VISTA EN PLANTA EXTINCIÓN PISO 4
ESCALA 1:150

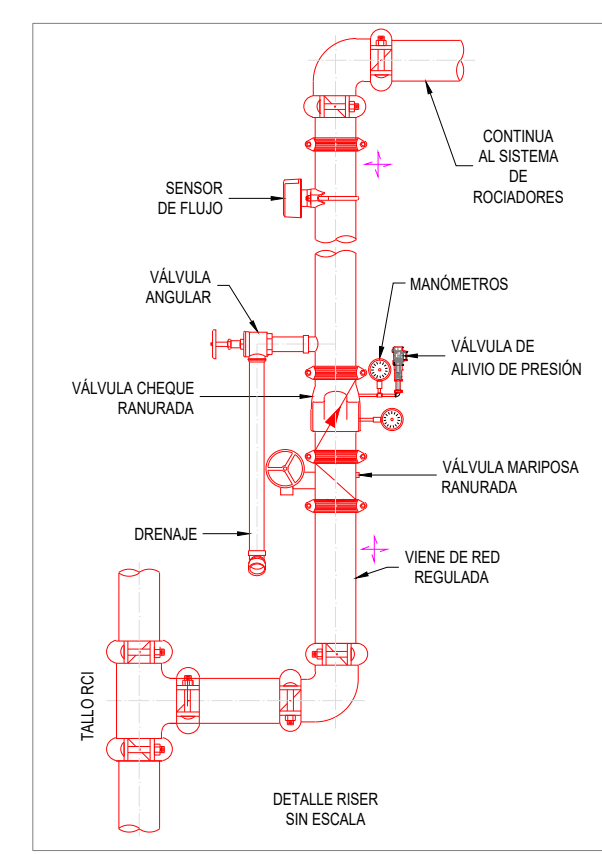

RESUMEN DEL CALCULO HIDRAULICO

Riser Tag	
Design Basis:	Ordinary Group I
Occupancy:	Ordinary Group I
Total Sprinklers:	947
Number Of Sprinklers Calculated:	7
Number Of Nozzles Calculated:	9
K-Factor:	8
Orifice Size:	0.531"
Design Density:	0.16gpm/ft²
Average Density:	0.16gpm/ft²
Area of Application:	139m² (Actual 78m²)
Demand at Base Of Riser or Point Of Connection	
Total Demand Flow(gpm):	152.65
Pressure(psi):	24.908
Water Supply Information At Time Of Design	
Static Pressure(psi):	220.000
Residual Pressure(psi):	202.06
Supply Flow(gpm):	750.00
Total Demand Flow(gpm):	302.65
Total Demand Pressure(psi):	67.267
Safety Margins(psi):	151.530

Hydraulic Information	
OCCUPANCY CLASSIFICATION	Ordinary Group I
DENSITY (gpm/ft²)	0.16 for 139m² (Actual 78m²)
TOTAL HOSE STREAMS	50.00
DRY CAPACITY	0.00gpm
TOTAL HEADS FLOWING	7
K-FACTOR	8
TOTAL WATER REQUIRED	152.65
TOTAL PRESSURE REQUIRED	67.567
BASE OF RISER (gpm)	202.06
BASE OF RISER (psi)	67.567
SAFETY MARGIN (psi)	+151.530 (69.2%)

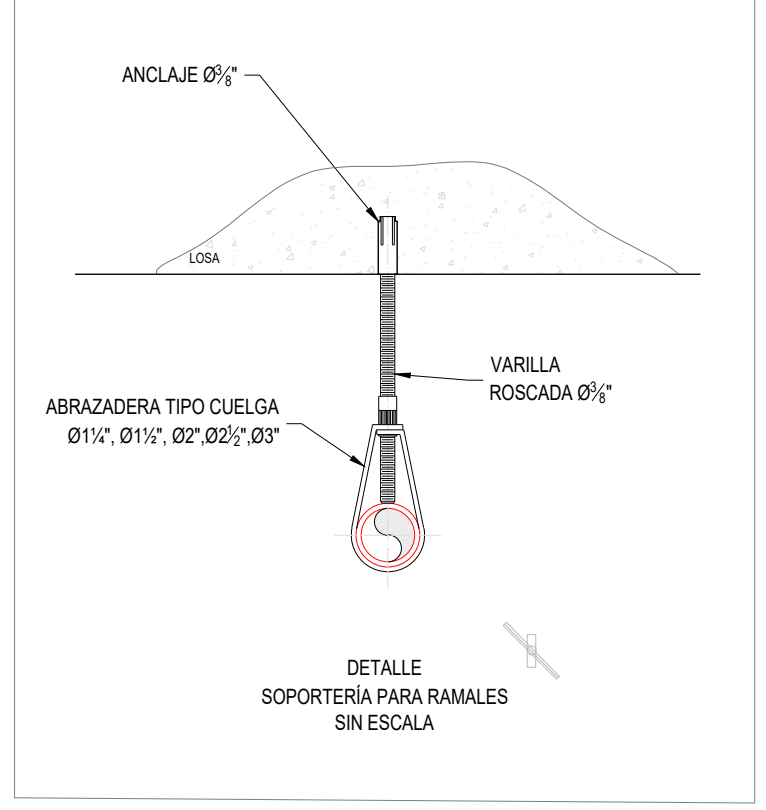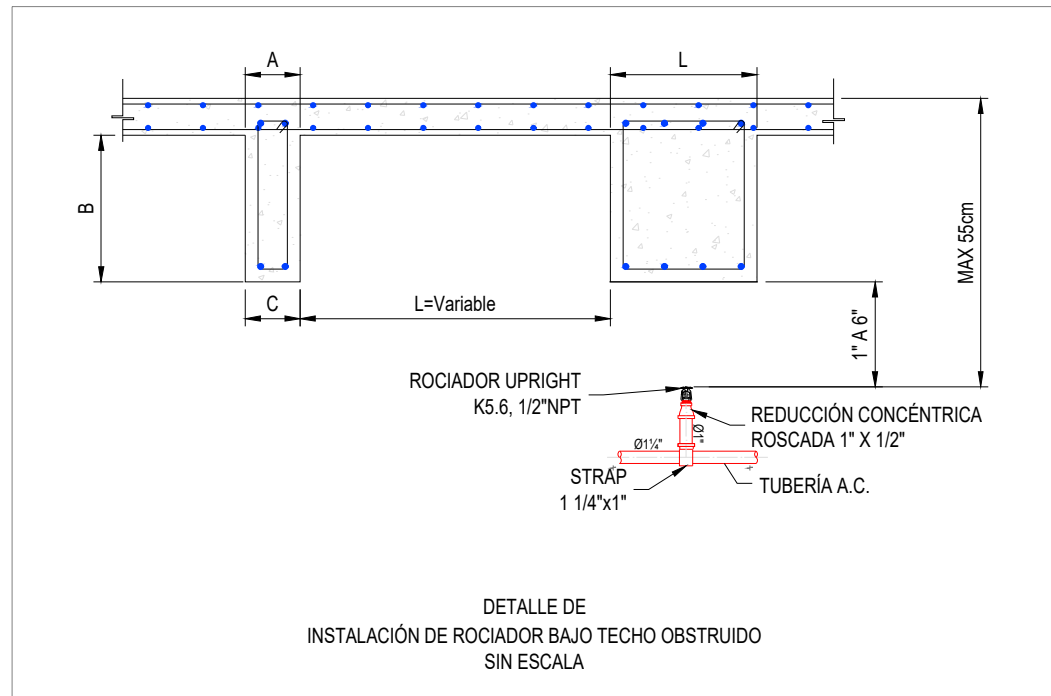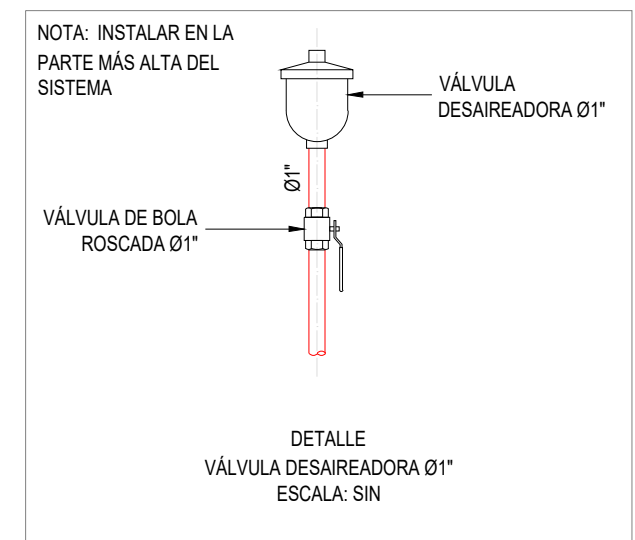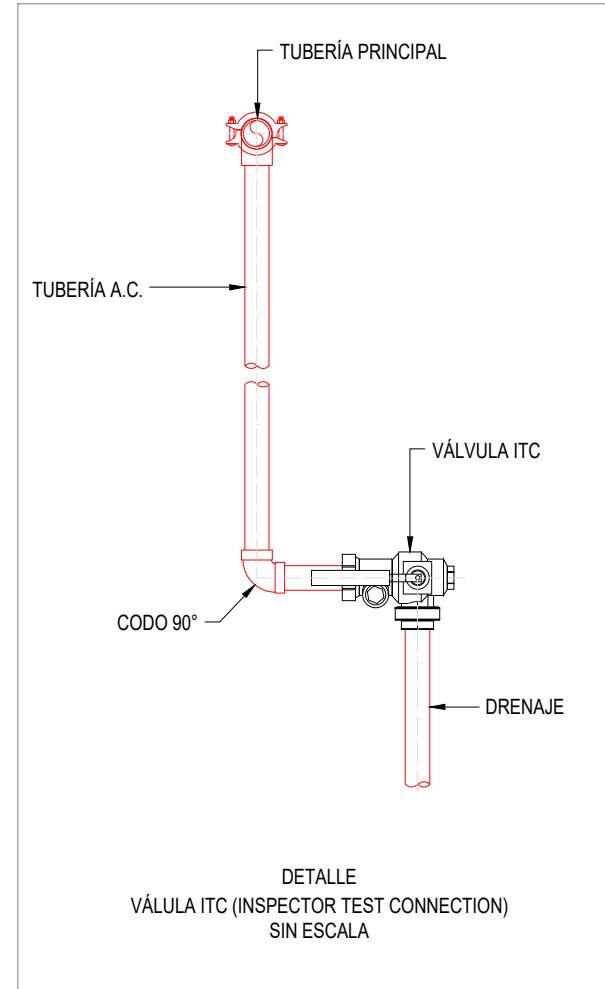

Sway Brace Zone Legend					
Diameter	Description	Unit Quantity	Quantity	Unit Weight	Net Weight
1.50	Pipe, Schedule 40	11.000	11.000	3.77gpm/ft	41.54kg
2.00	Pipe, Schedule 40	11.000	11.000	6.77gpm/ft	74.46kg
2.50	Pipe, Schedule 40	11.000	11.000	11.00gpm/ft	121.00kg
				Total Net Weight	237.00kg
				Total Load (x 1.15)	272.55kg

Sway Brace Tag			
Brace Type	Brace Pipe Size	Fastener Type	Fastener Orientation
Longitudinal	1"	WPA Type 30	WPA Type 30
Brace Angle	Attached To	Fastener Size	Maximum Fastener Load
30	Normal Weight Concrete (2000psi)	3/8 x 3	248.50kg
Code: NFPA 913 - 2007		Table: 9.3.5.5.1	Plan ID: L12.0"

Sway Brace Zone Legend					
Diameter	Description	Unit Quantity	Quantity	Unit Weight	Net Weight
1.50	Pipe, Schedule 40	11.000	11.000	3.77gpm/ft	41.54kg
2.00	Pipe, Schedule 40	11.000	11.000	6.77gpm/ft	74.46kg
2.50	Pipe, Schedule 40	11.000	11.000	11.00gpm/ft	121.00kg
				Total Net Weight	237.00kg
				Total Load (x 1.15)	272.55kg

Sway Brace Tag			
Brace Type	Brace Pipe Size	Fastener Type	Fastener Orientation
Longitudinal	1"	WPA Type 30	WPA Type 30
Brace Angle	Attached To	Fastener Size	Maximum Fastener Load
30	Normal Weight Concrete (2000psi)	3/8 x 3	248.50kg
Code: NFPA 913 - 2007		Table: 9.3.5.5.1	Plan ID: L12.0"

DETALLE DE LA SOPORTERIA SISMO RESISTENTE.

REGISTRO DE MODIFICACIONES		
MODIF.	FECHA	DESCRIPCION
1	--	----
2	--	----
3	--	----
4	--	----
5	--	----

REGISTRO DE REVISIONES		
REV.	FECHA	EMITIDO PARA:
0	24-06-2024	ACTUALIZACION
1	18-02-2025	ACTUALIZACION
2	--	----
3	--	----
4	--	----
5	--	----
6	--	----

CARACTERÍSTICAS ROCIADORES			
ORIENTACIÓN	K	ROSCA TEMPERATURA RESPUESTA	COBERTURA
UPRIGHT	8	3/4"	68°C
			RAPIDA
			ESTANDAR

CARACTERÍSTICAS ROCIADORES			
ORIENTACIÓN	K	ROSCA TEMPERATURA RESPUESTA	COBERTURA
PENDENT	8	3/4"	68°C
			RAPIDA
			ESTANDAR

CONVENCIONES	
	TUBERIA EXPUESTA
	TUBERIA ENTERRADA
	TUBERIA POR CÁRCAMO
	TUBERIA CPVC
	UNION RANURADA
	CODO 90° RANURADO
	TEE RANURADA
	HIDRANTE CONTRA INCENDIO
	ESTACION DE MANGUERA SISTEMA HUMEDO
	RISER (SISTEMA CONTROLADOR)
	SIAMESA CONEXION PARA BOMBEROS 4"x2 1/2"x2 1/2"
	NODO HIDRAULICO
	ÁREA DE DISEÑO
	SOPORTE COLGANTE
	SOPORTE SISMICO CUATRO VÍAS
	SOPORTE SISMO RESISTENTE LONGITUDINAL
	SOPORTE SISMO RESISTENTE LATERAL
	BLOQUE DE EMPUJE
	VALVULA DE INSPECCIÓN, PRUEBA Y DRENAJE
	VALVULA DESAIREADORA
	FUTURA CONEXIÓN
	UNIÓN SISMICA
	ESTACION DE MANGUERA CLASE II

ELABORADO POR:

ELABORADO PARA:

AYURA MOTORS ETAPA 3

ENVIGADO-ANTIOQUIA

PROYECTO:

SISTEMA DE EXTINCIÓN DE INCENDIOS

CONTIENE:

ROCIADORES PISO 4

ELABORÓ:	REVISÓ:
MODELO:	UNIDADES:
FECHA:	ESCALA:
VERSIÓN:	FORMATO:

PROYECTO No: GL 706

PLANO No. PLANO 5 de 12

NOTAS:

- LAS LONGITUDES SE INDICAN EN METROS Y LOS DIÁMETROS EN PULGADAS
- ESTE DOCUMENTO CORRESPONDE A UN PLANO DE DISEÑO, LAS DIMENSIONES INDICADAS DEBEN SER VERIFICADAS EN OBRA