



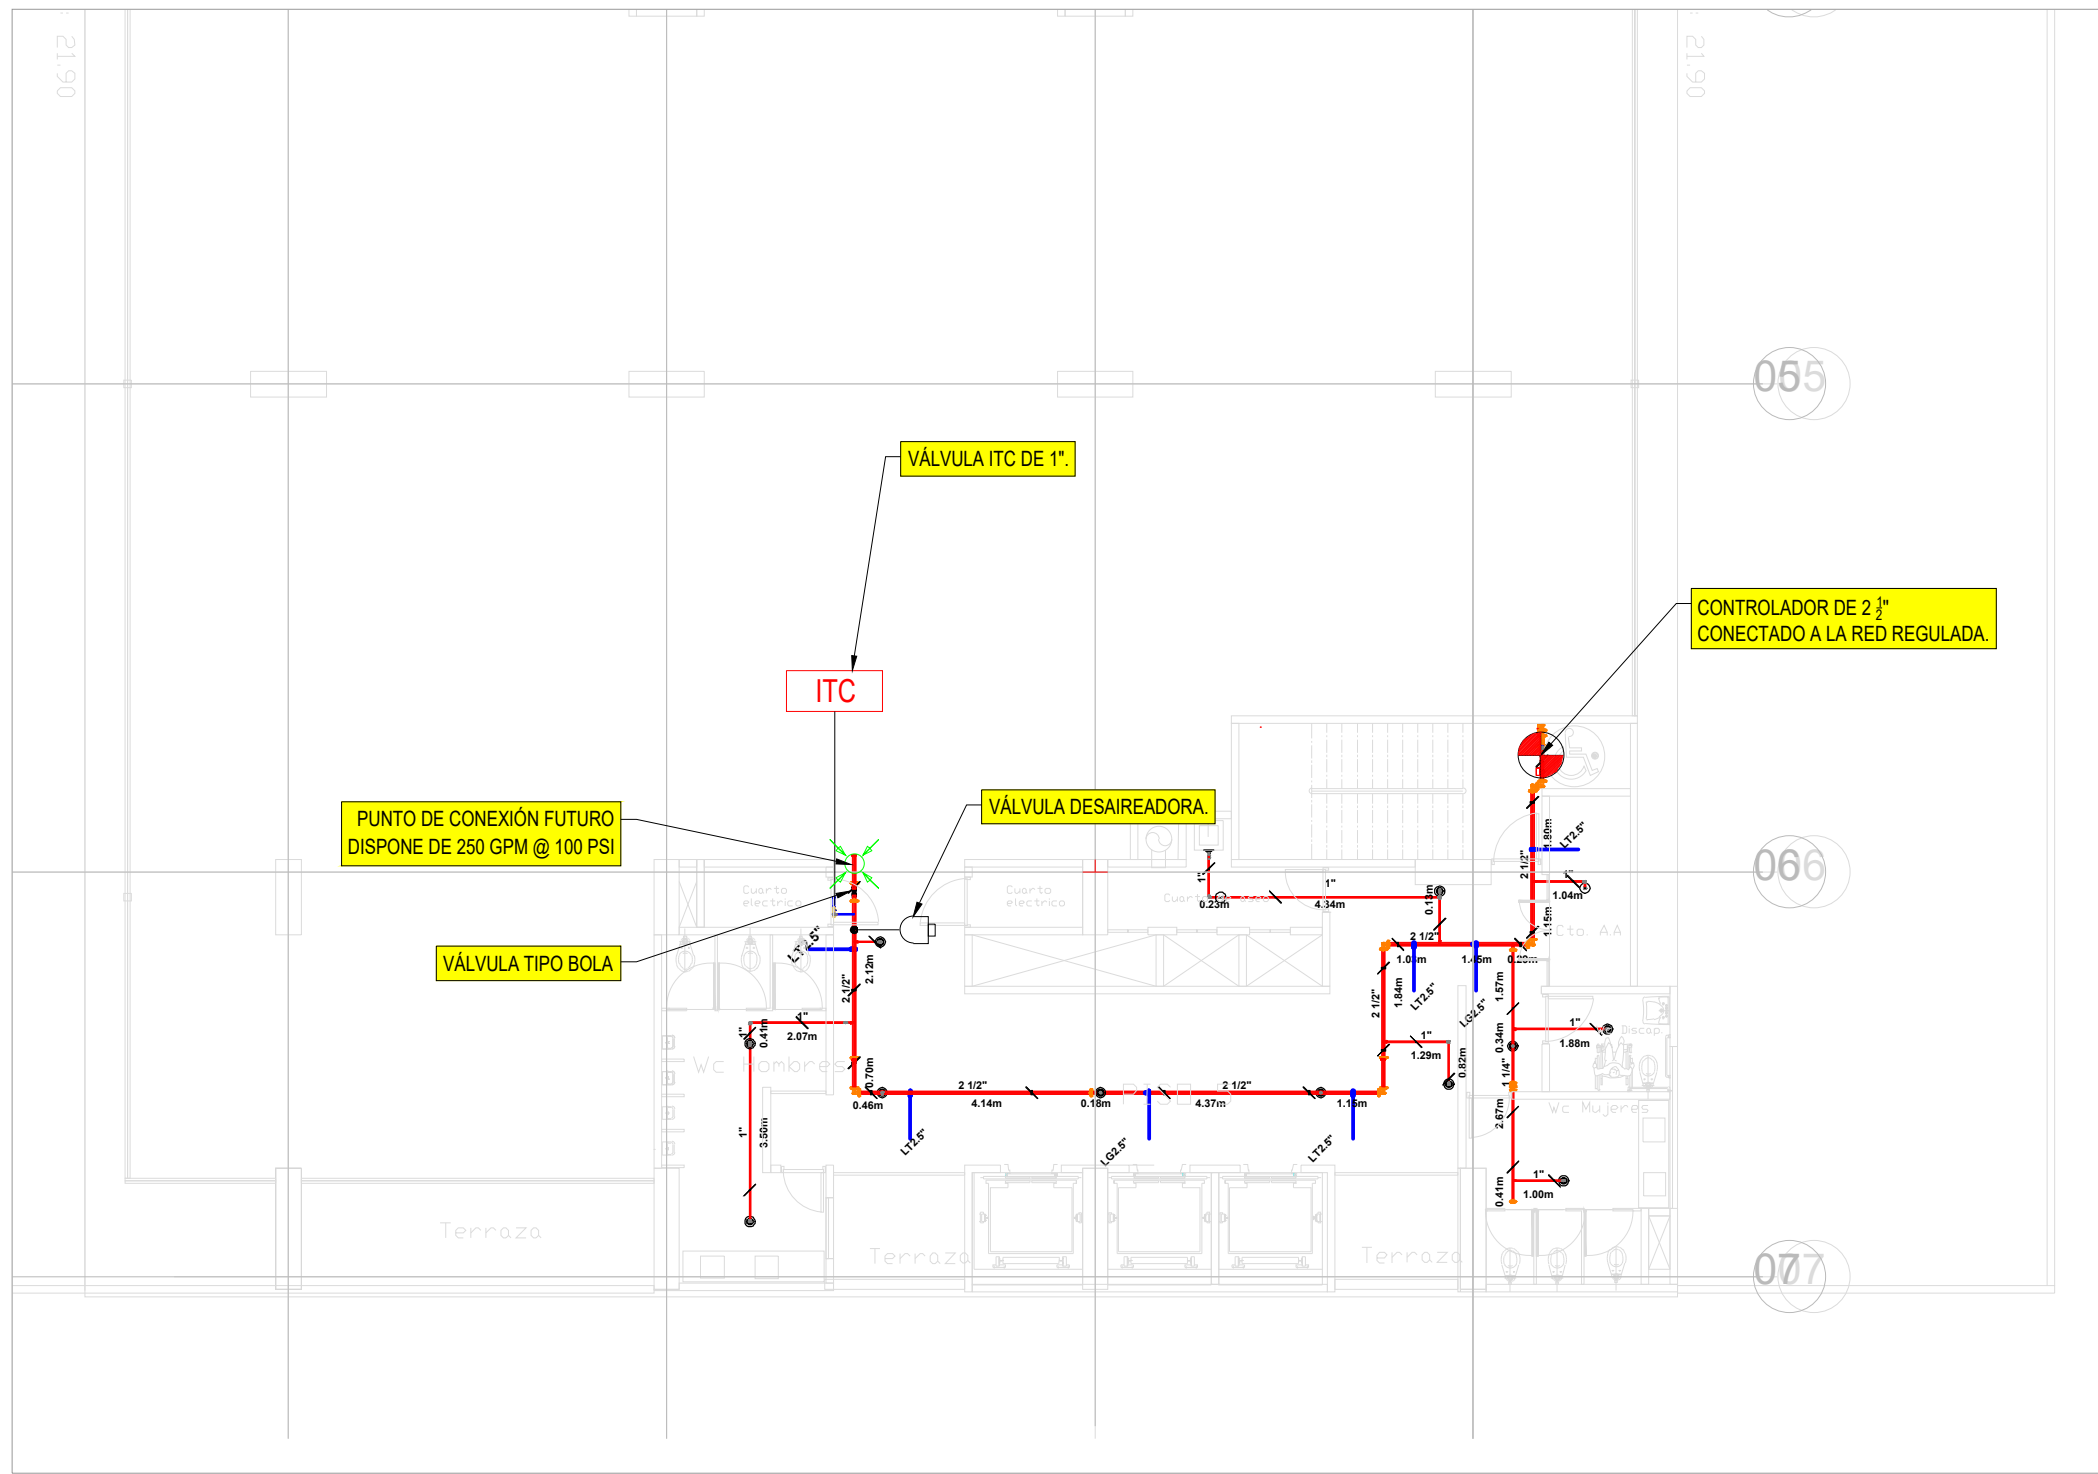

1 VISTA EN PLANTA EXTINCIÓN PISO 5
ESCALA 1:150

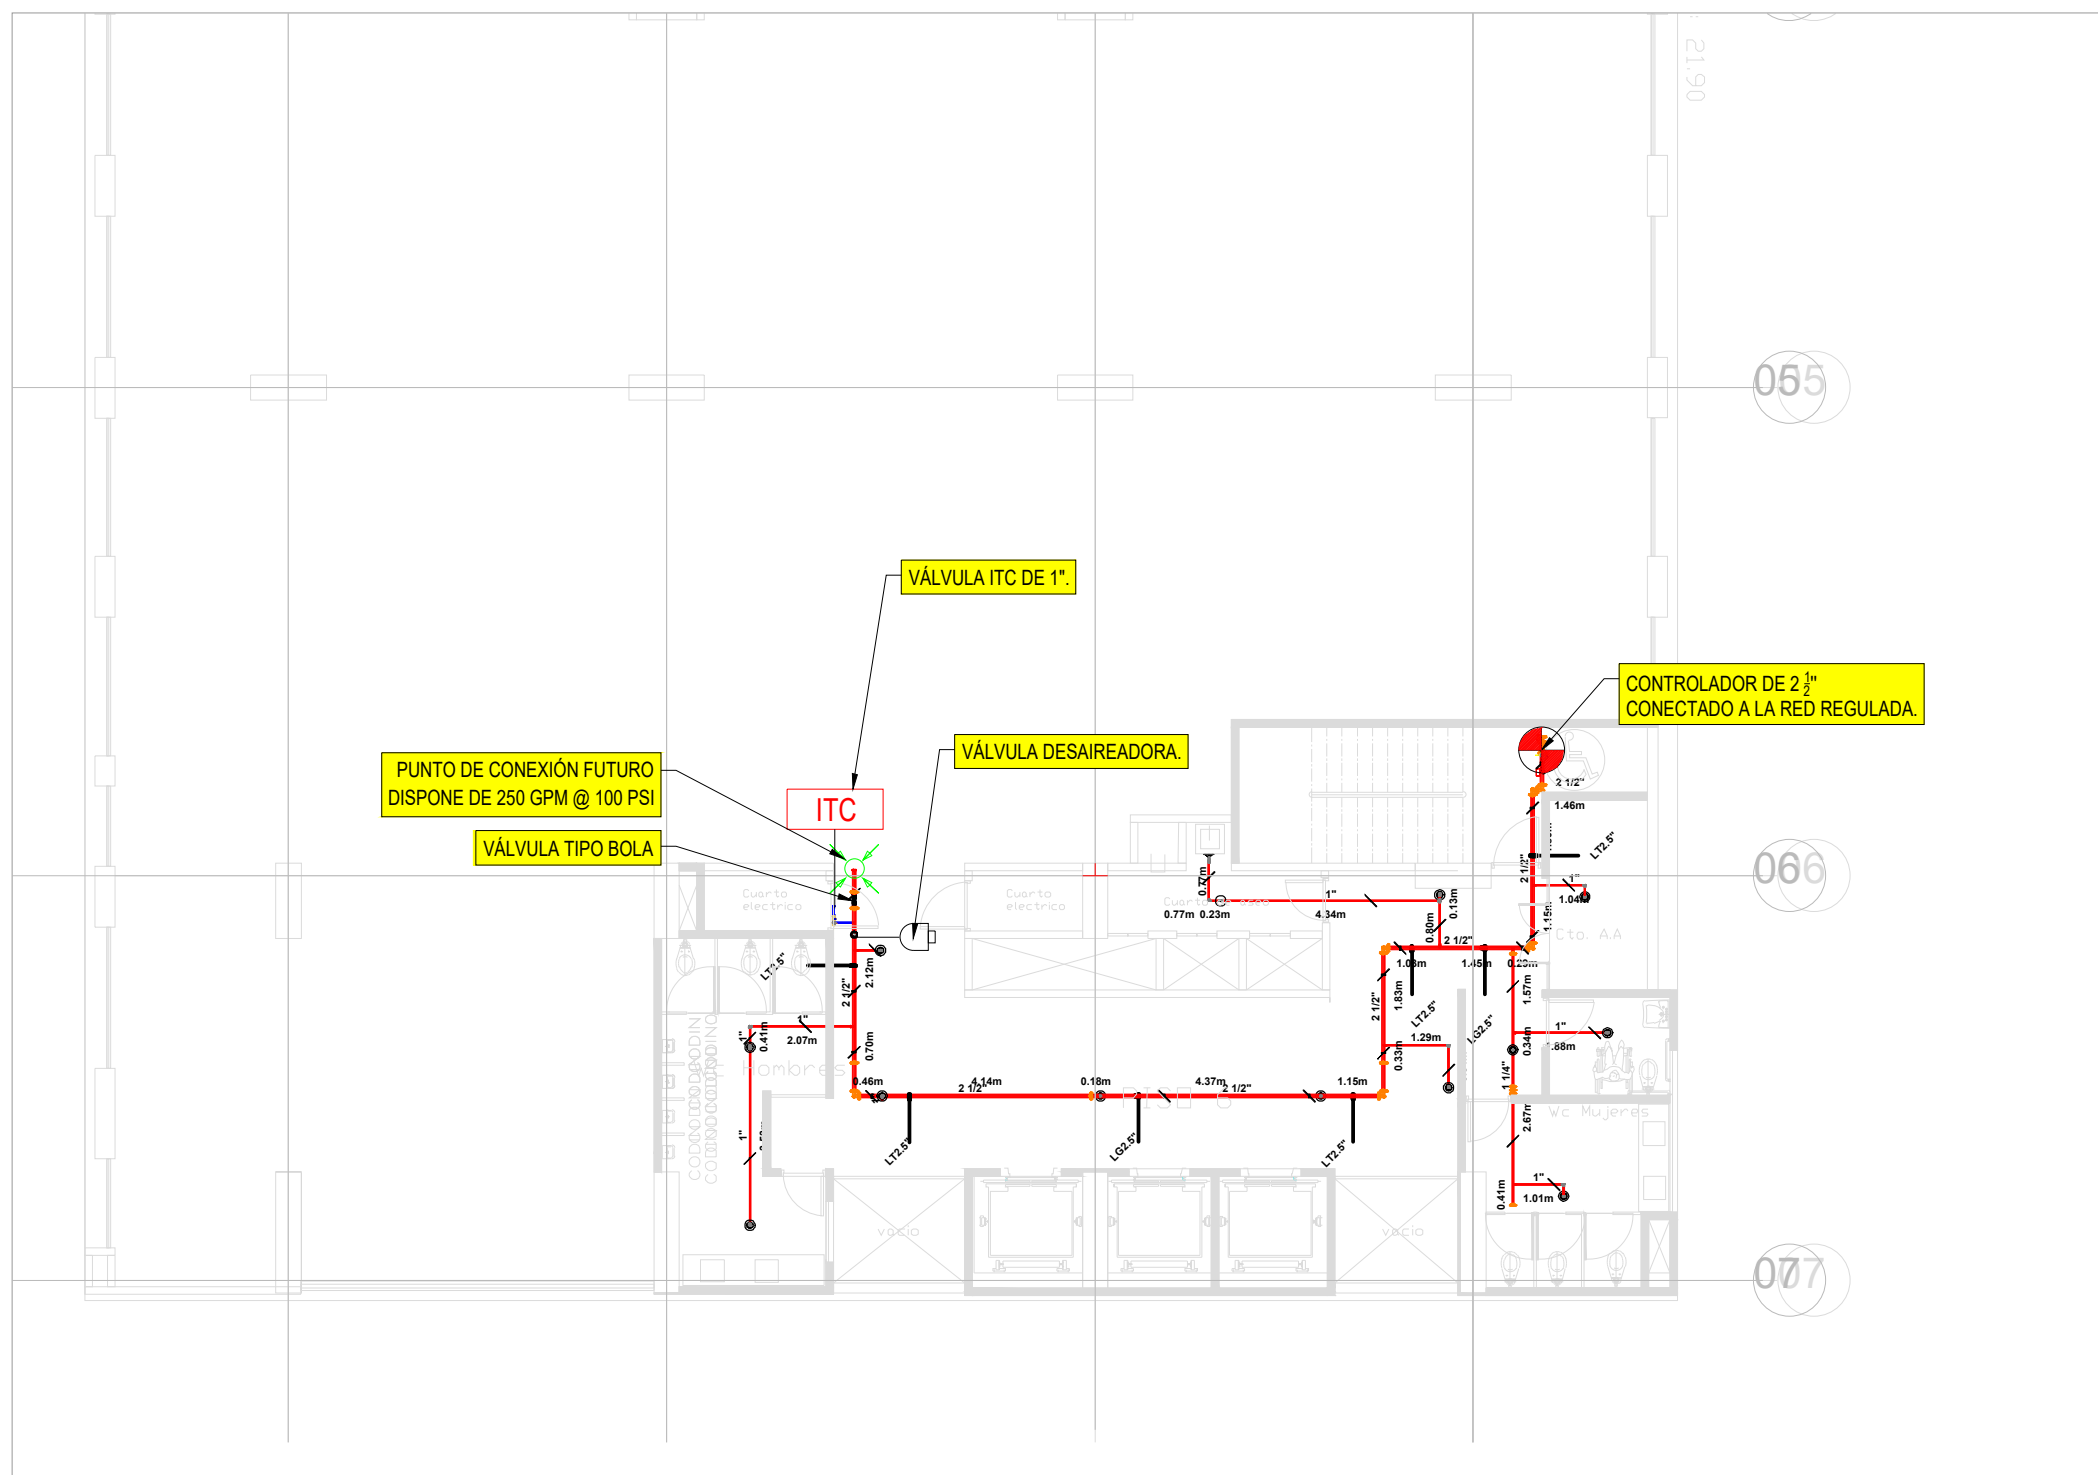

2 VISTA EN PLANTA EXTINCIÓN PISO 6
ESCALA 1:150






Sway Brace Zone Legend					
Diameter	Description	Unit Quantity	Quantity	Unit Weight	Cp =
2 1/4"	Pipe, Schedule 10	(24.24m)	13.74m	2.77kg/0.6	23.44kg
2 1/2"	Pipe, Schedule 10	(24.24m)	13.74m	2.77kg/0.6	23.44kg
3"	Pipe, Schedule 40	(24.24m)	4.71m	3.86kg/0.8	18.19kg
				Total Net Weight	65.07kg
				Total Load (x 1.15)	74.83kg

Sway Brace Tag					
Brace Type	Brace Pipe Size	Fastener Type	Fastener Orientation		
Lateral	1"	Anchor, 1/2" x 6" x 12" (C5)	WPA Type "A"		
Brace Angle	30°	Normal Weight Concrete (2400psi)	30 x 3	Maximum Fastener Load	248.93kg
		Code: WPA #13 - 2007	Table: 3.3.5.1	Plan ID: L12.2"	Manufacturer: Tolo Inc.


DETALLE DE LA SOPORTERIA SISMO RESISTENTE.

Sway Brace Zone Legend					
Diameter	Description	Unit Quantity	Quantity	Unit Weight	Cp =
2 1/4"	Pipe, Schedule 10	(24.24m)	13.74m	2.77kg/0.6	23.44kg
2 1/2"	Pipe, Schedule 10	(24.24m)	13.74m	2.77kg/0.6	23.44kg
3"	Pipe, Schedule 40	(24.24m)	4.71m	3.86kg/0.8	18.19kg
				Total Net Weight	65.07kg
				Total Load (x 1.15)	74.83kg

Sway Brace Tag					
Brace Type	Brace Pipe Size	Fastener Type	Fastener Orientation		
Longitudinal	1"	Anchor, 1/2" x 6" x 12" (C5)	WPA Type "A"		
Brace Angle	30°	Normal Weight Concrete (2400psi)	30 x 3	Maximum Fastener Load	248.93kg
		Code: WPA #13 - 2007	Table: 3.3.5.1	Plan ID: L12.2"	Manufacturer: Tolo Inc.

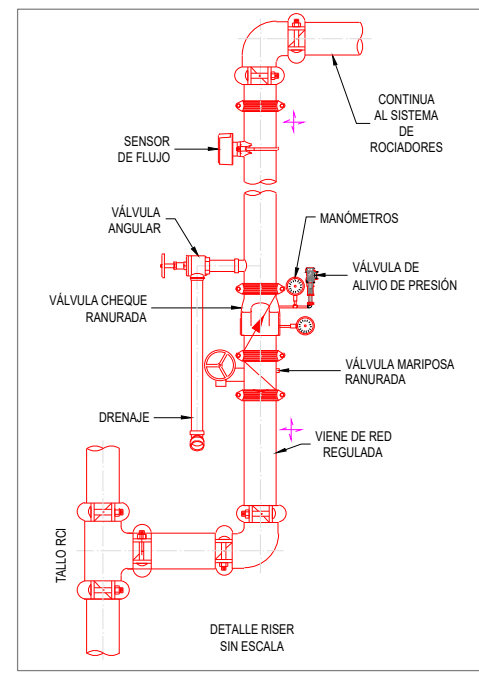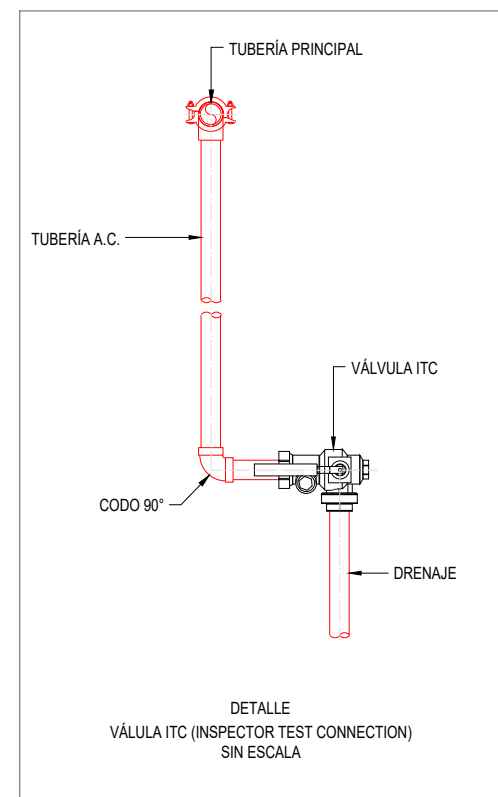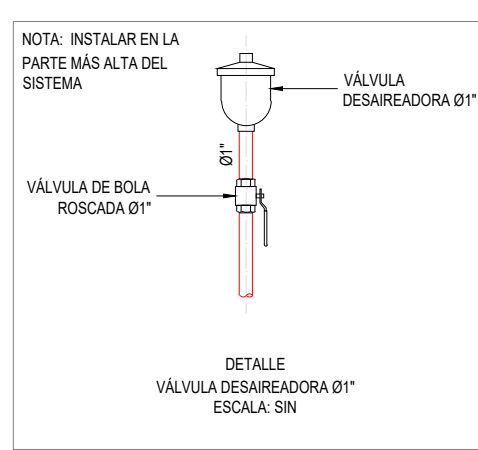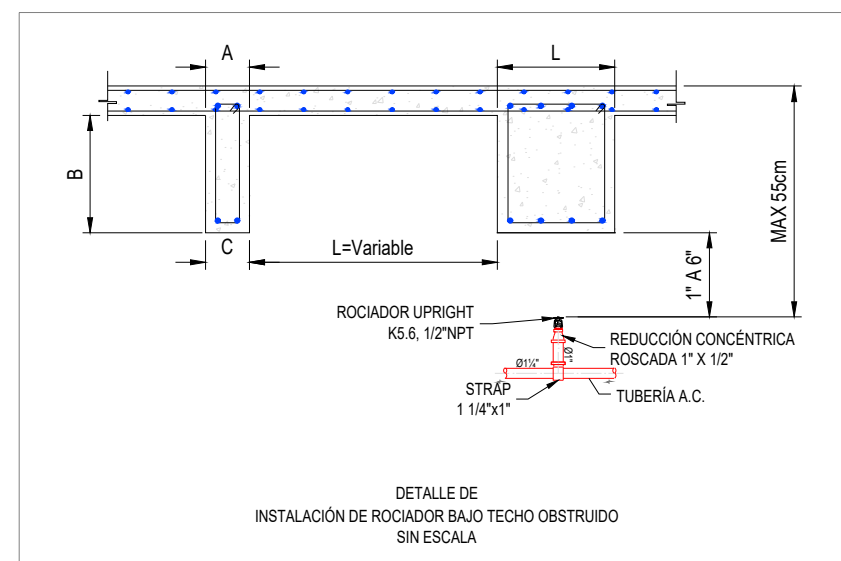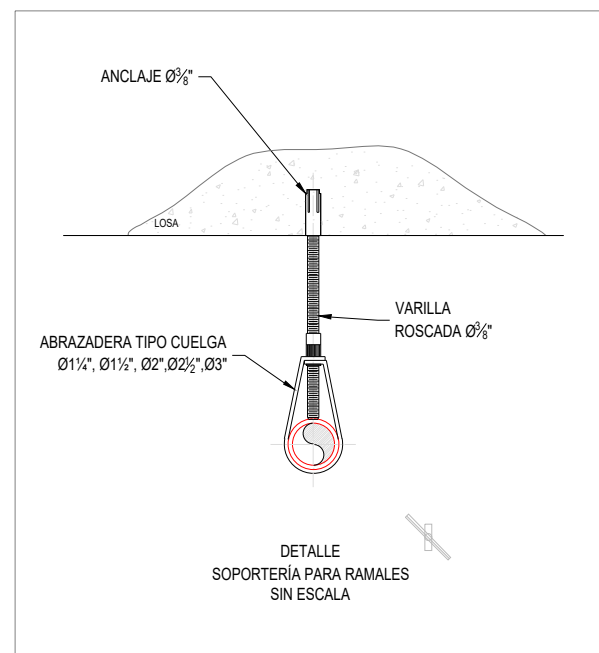

3 VISTA EN PLANTA EXTINCIÓN PISO 7
ESCALA 1:150

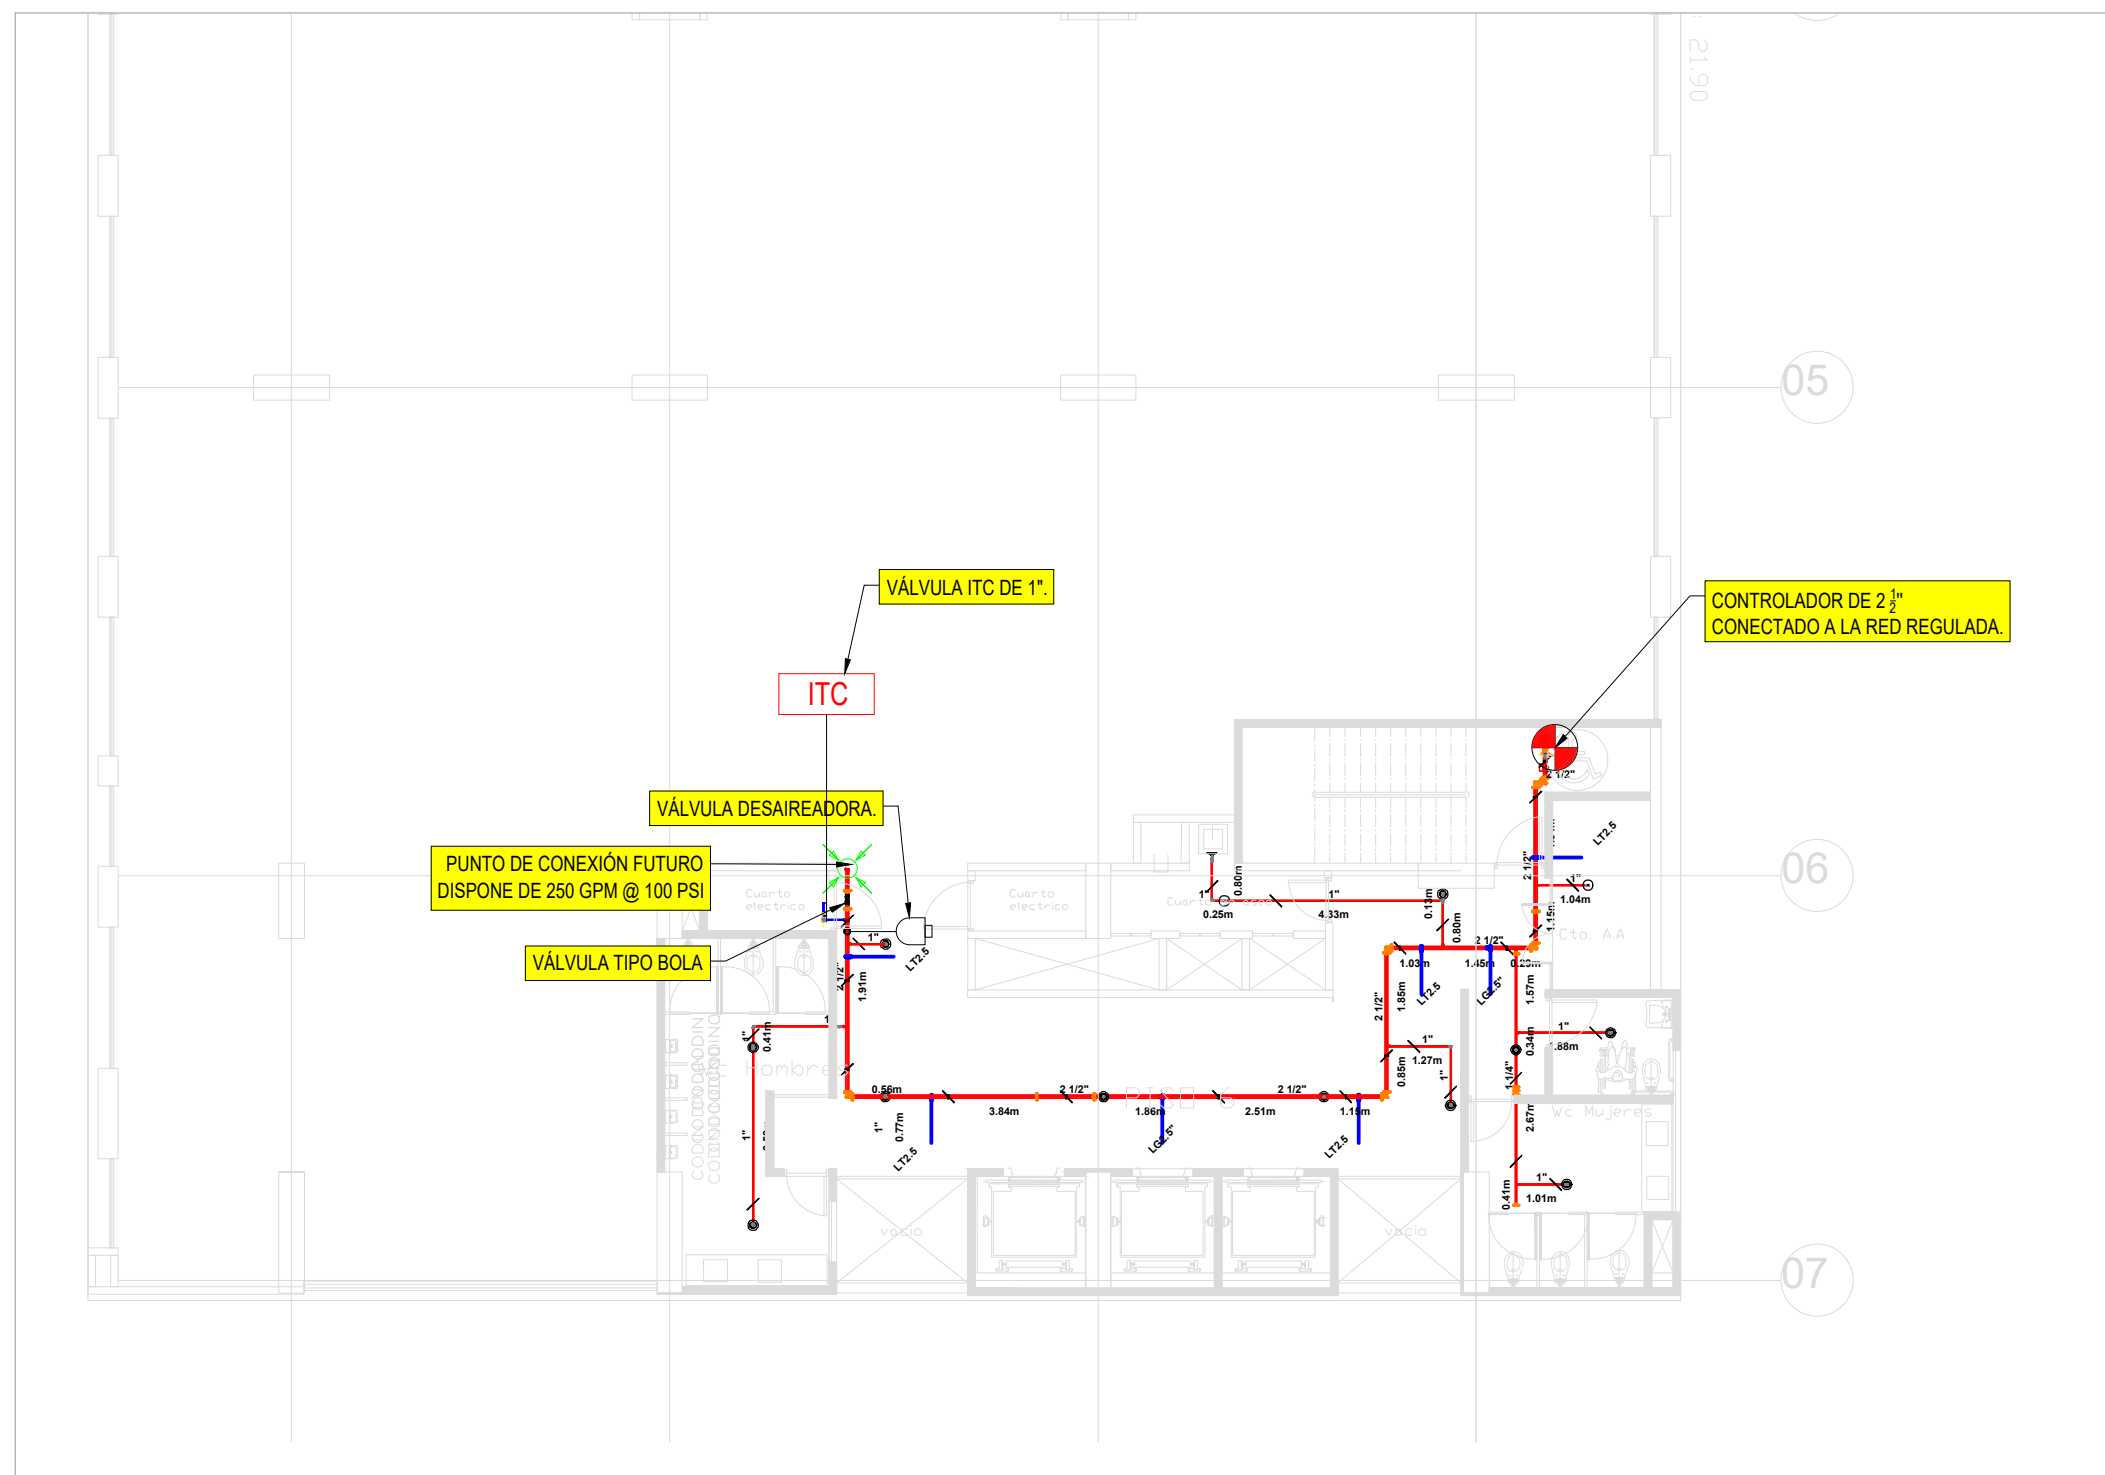

4 VISTA EN PLANTA EXTINCIÓN PISO 8
ESCALA 1:150

REGISTRO DE MODIFICACIONES		
MODIF.	FECHA	DESCRIPCIÓN
1	--	----
2	--	----
3	--	----
4	--	----

REGISTRO DE REVISIONES		
REV.	FECHA	EMITIDO PARA:
0	24-06-2024	ACTUALIZACION
1	18-02-2025	ACTUALIZACION
2	--	----
3	--	----
4	--	----
5	--	----
6	--	----

CARACTERÍSTICAS ROCIADORES				
ORIENTACIÓN	K	ROSCA	TEMPERATURA RESPUESTA	COBERTURA
UPRIGHT	8	3/4"	68°C	RAPIDA ESTANDAR

CARACTERÍSTICAS ROCIADORES				
ORIENTACIÓN	K	ROSCA	TEMPERATURA RESPUESTA	COBERTURA
PENDENT	8	3/4"	68°C	RAPIDA ESTANDAR

CONVENCIONES	
	TUBERÍA EXPUESTA
	TUBERÍA ENTERRADA
	TUBERÍA POR CÁRCAMO
	TUBERÍA CPVC
	UNIÓN RANURADA
	CODO 90° RANURADO
	TEE RANURADA
	HIDRANTE CONTRA INCENDIO
	ESTACION DE MANGUERA SISTEMA HUMEDO
	RISER (SISTEMA CONTROLADOR)
	SIAMESA CONEXION PARA BOMBEROS 4"x2 1/2"
	NODO HIDRÁULICO
	ÁREA DE DISEÑO
	SOPORTE COLGANTE
	SOPORTE SÍSMICO CUATRO VÍAS
	SOPORTE SÍSMO RESISTENTE LONGITUDINAL
	SOPORTE SÍSMO RESISTENTE LATERAL
	BLOQUE DE EMPUJE
	VÁLVULA DE INSPECCIÓN, PRUEBA Y DRENAJE
	VÁLVULA DESAIREADORA
	FUTURA CONEXIÓN
	UNIÓN SÍSMICA
	ESTACION DE MANGUERA CLASE II

ELABORADO POR:

ELABORADO PARA:

AYURA MOTORS ETAPA 3

ENVIGADO-ANTIOQUIA

PROYECTO:

SISTEMA DE EXTINCIÓN DE INCENDIOS

CONTIENE:

ROCIADORES PISO 5 A 8

ELABORÓ:	REVISÓ:
MODELO:	UNIDADES: Metros
FECHA: 14-11-2025	ESCALA: INDICADAS
VERSIÓN: 05	VERS. MOD: 05
PROYECTO No: GL 706	FORMATO: A1
PLANO No. PLANO 6 de 12	

NOTAS:

- LAS LONGITUDES SE INDICAN EN METROS Y LOS DIÁMETROS EN PULGADAS
- ESTE DOCUMENTO CORRESPONDE A UN PLANO DE DISEÑO, LAS DIMENSIONES INDICADAS DEBEN SER VERIFICADAS EN OBRA