




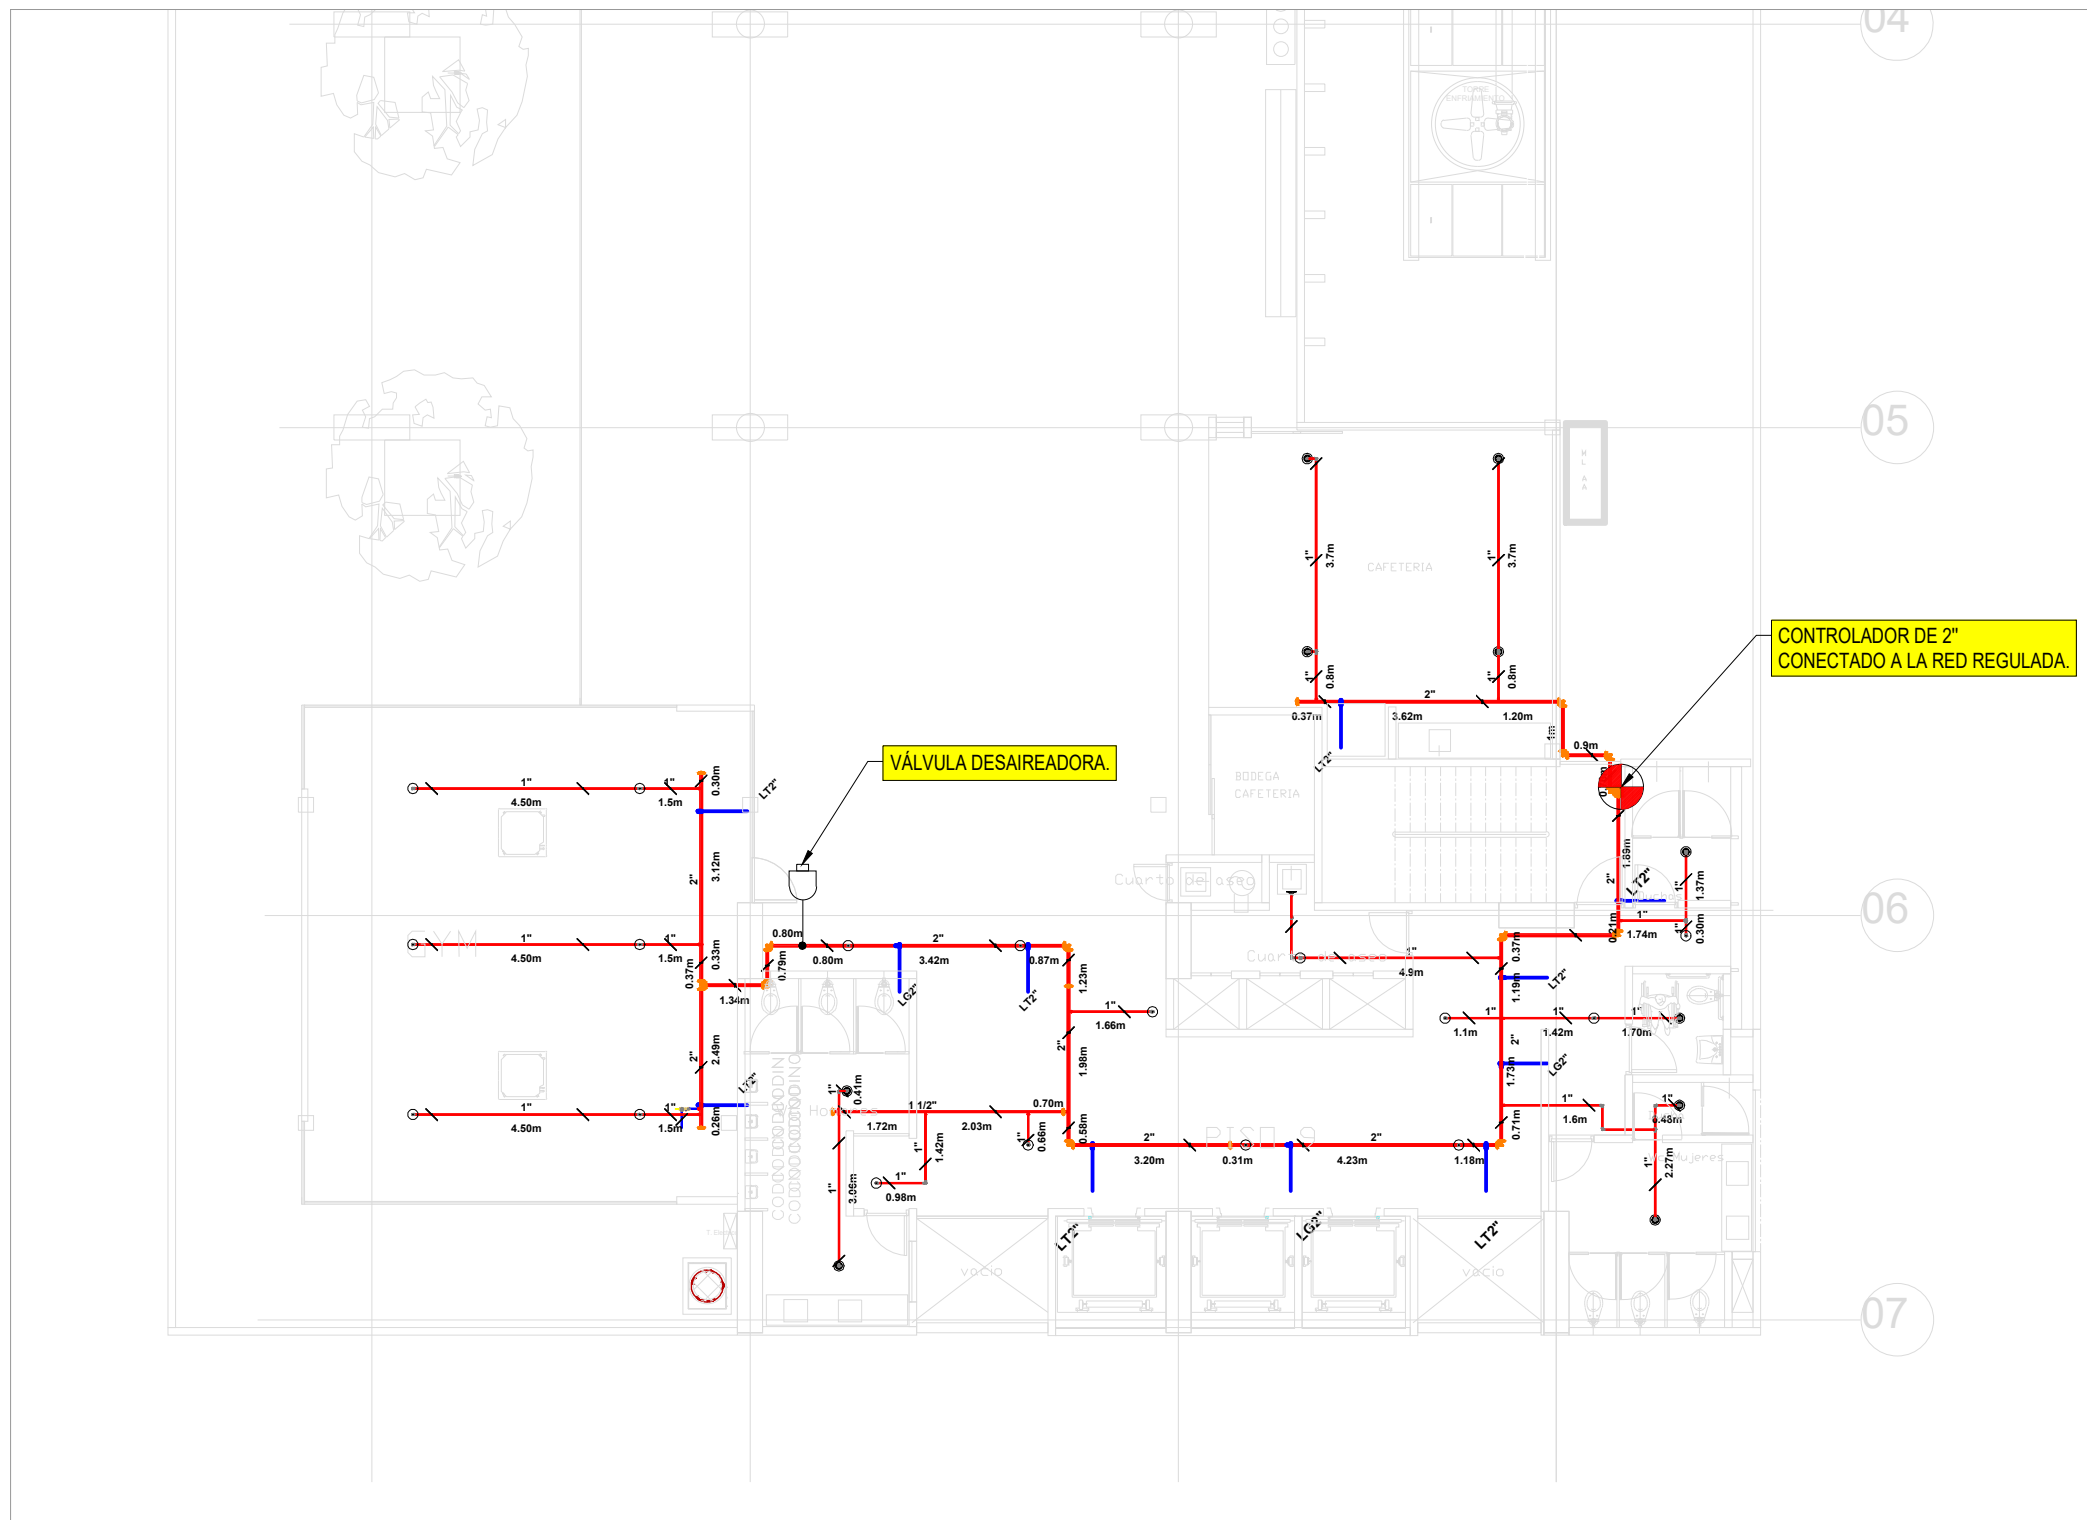


1 VISTA EN PLANTA EXTINCIÓN PISO 9
ESCALA 1:150

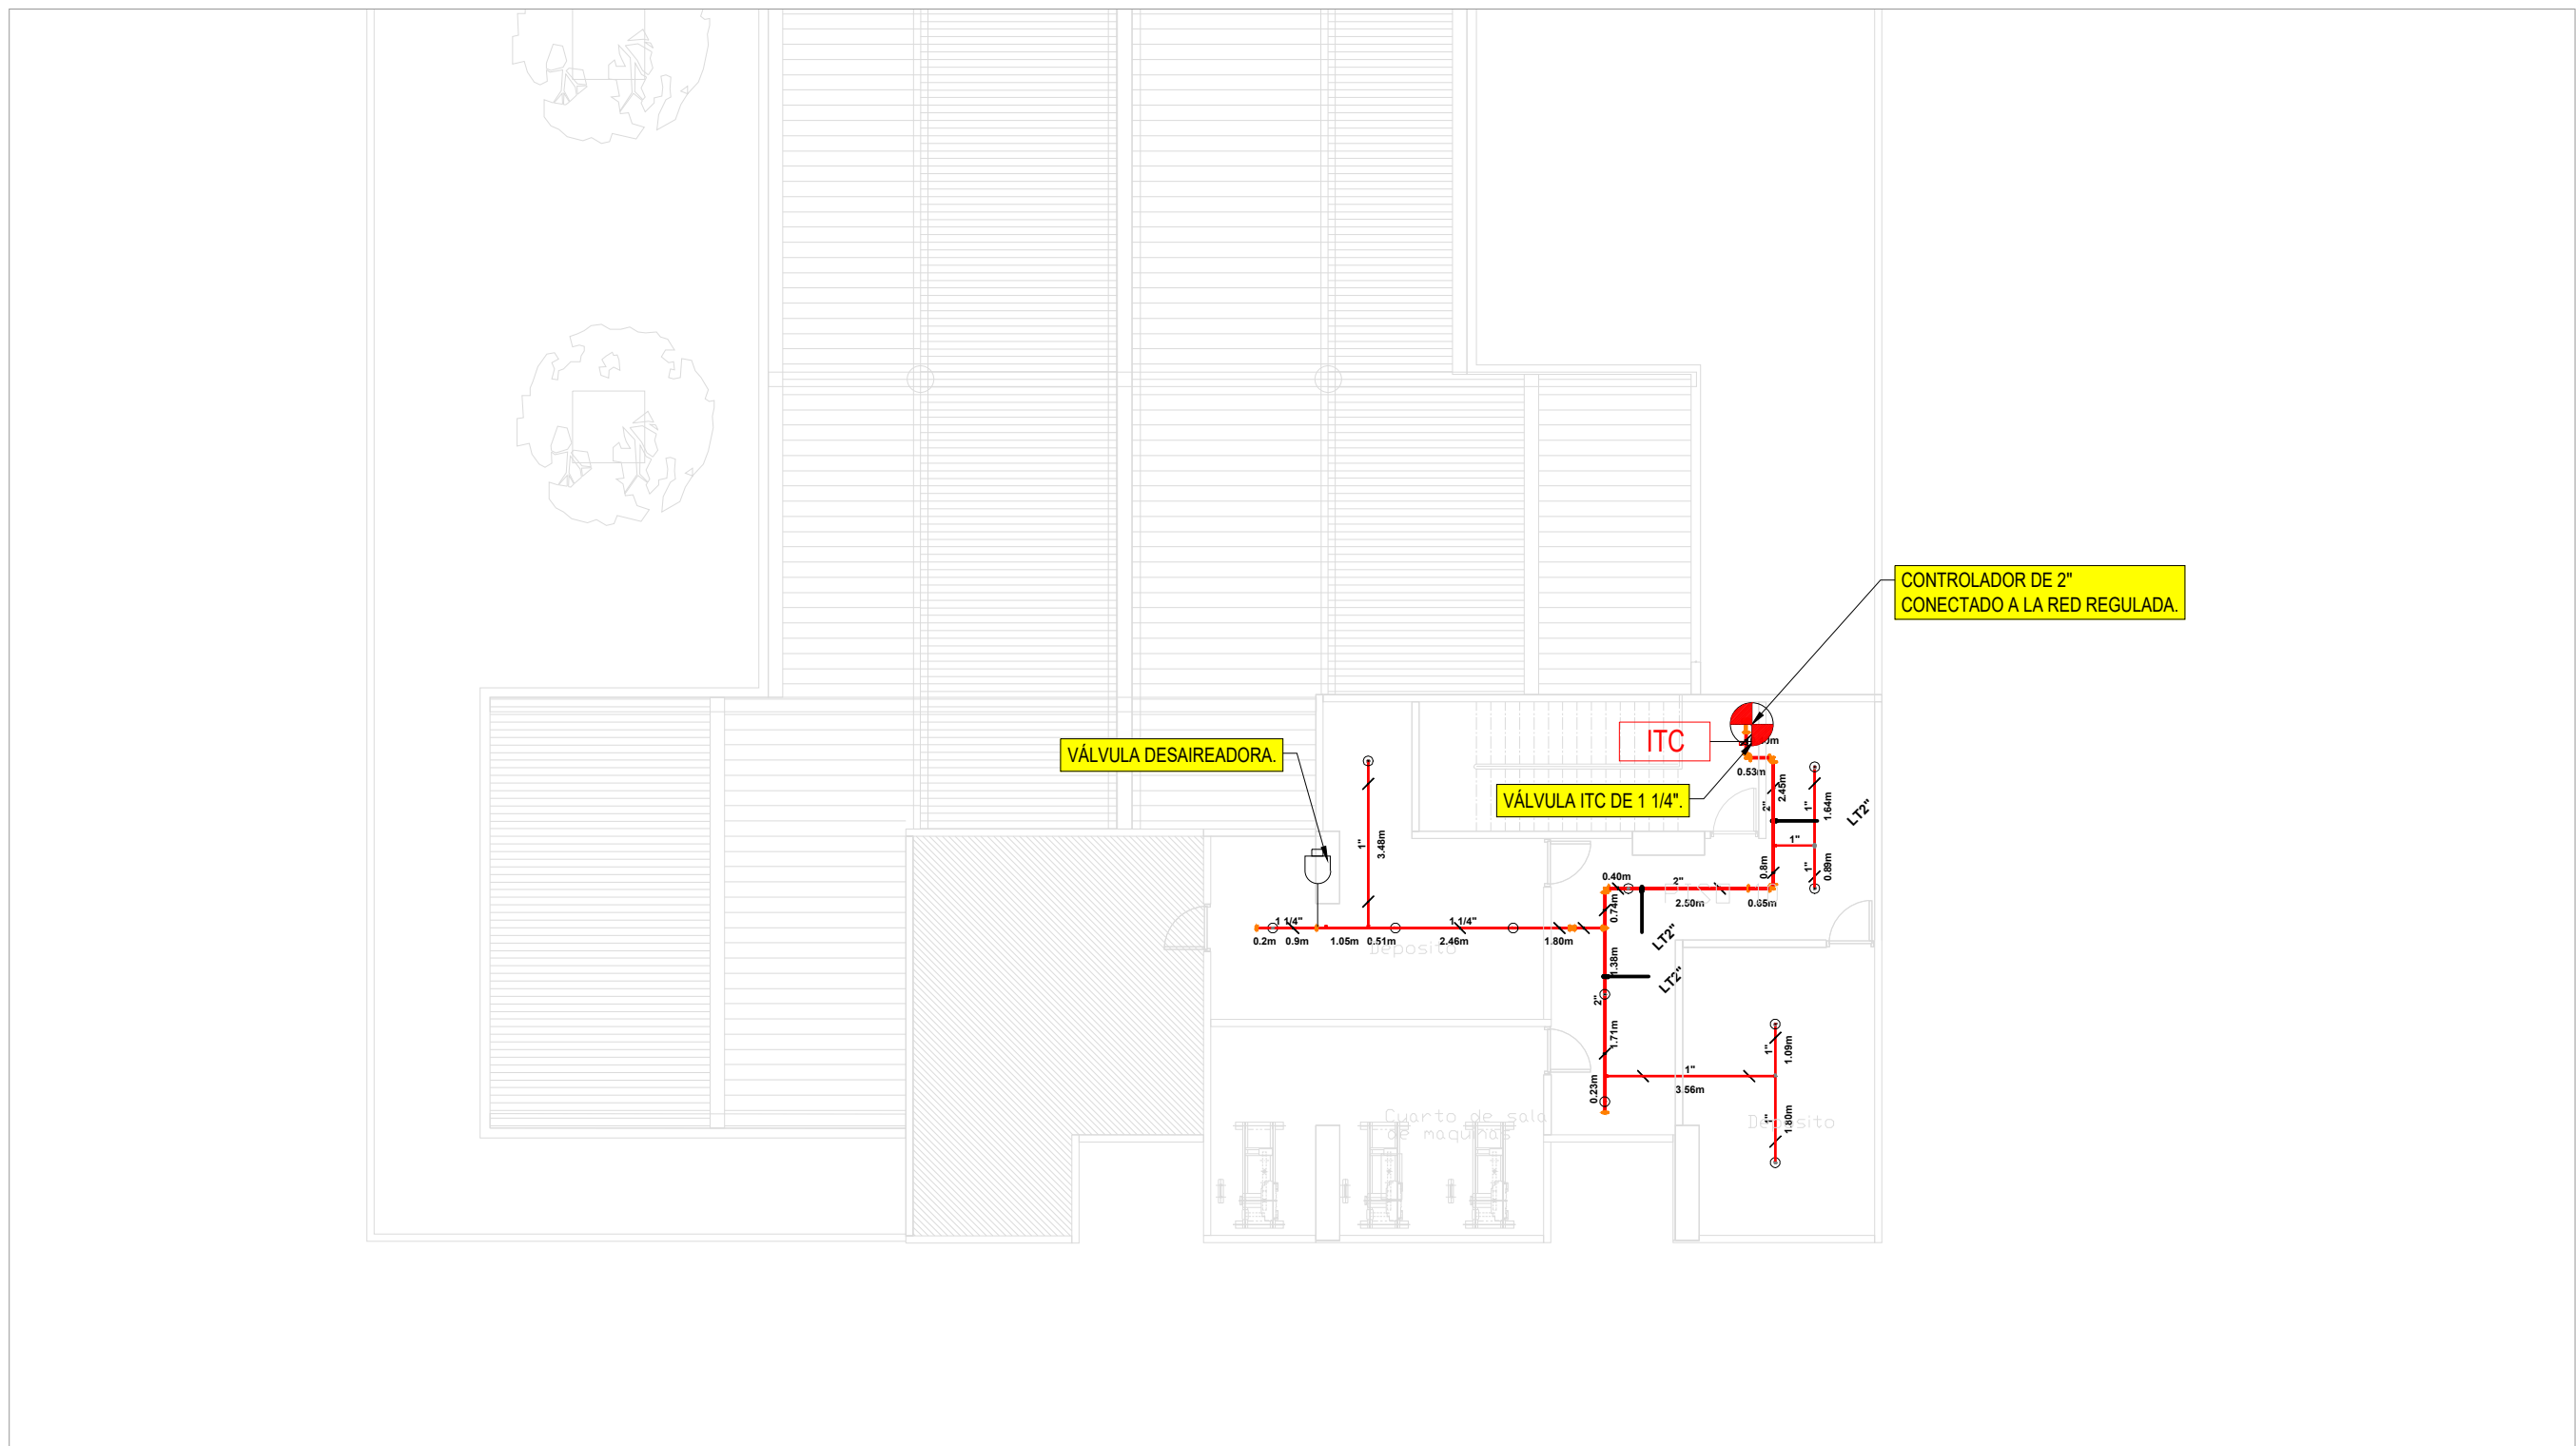


2 VISTA EN PLANTA EXTINCIÓN CUBIERTA
ESCALA 1:150

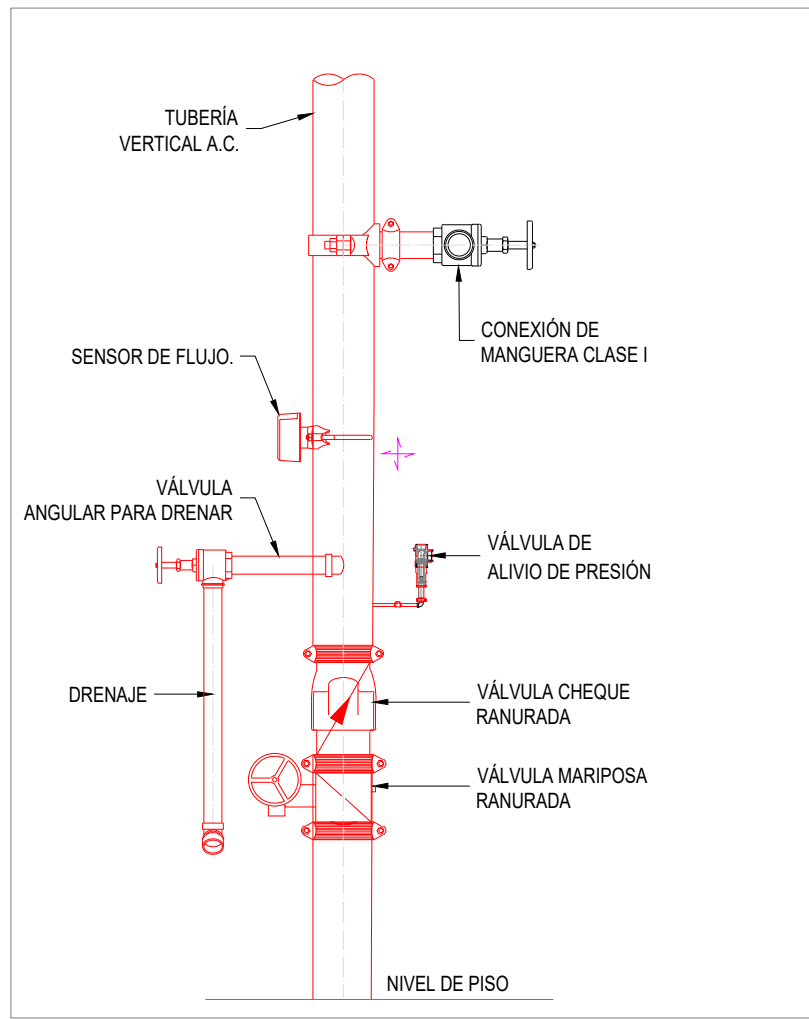


DETALLE PARA TUBERÍA VERTICAL PRIMER NIVEL SIN ESCALA

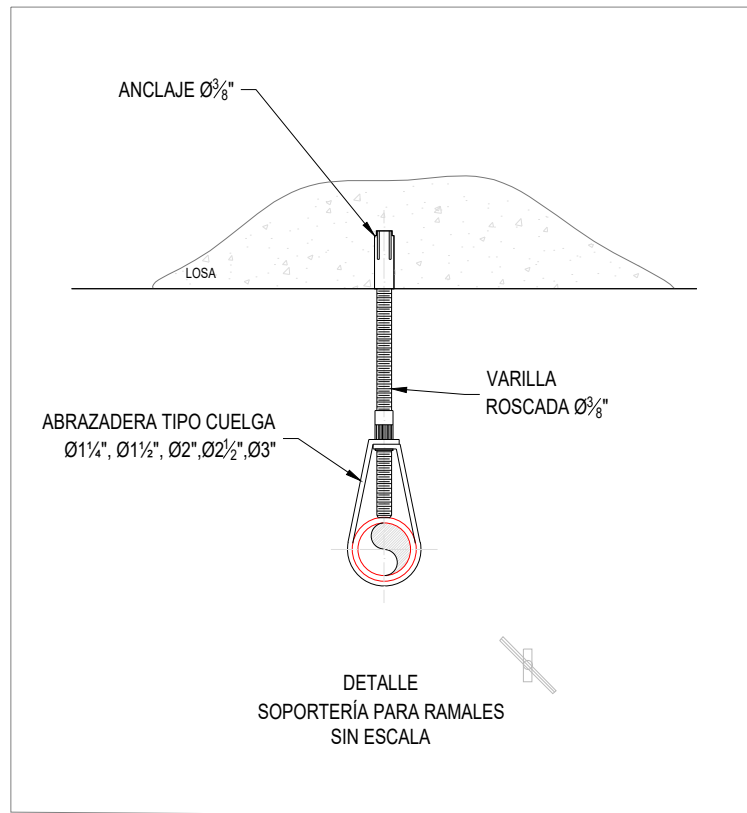


DETALLE SOPORTERÍA PARA RAMALES SIN ESCALA

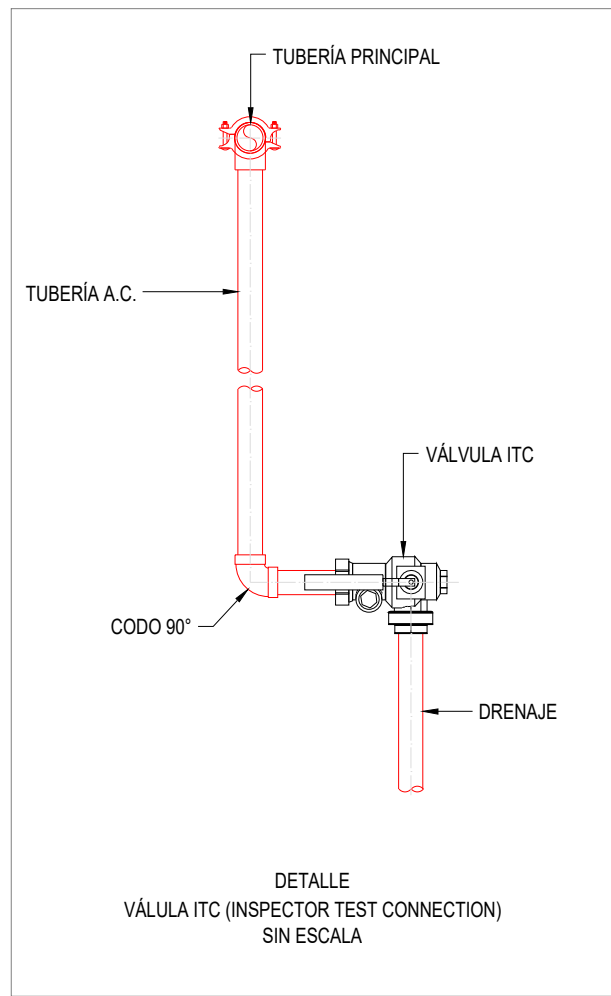

DETALLE VÁLVULA ITC (INSPECTOR TEST CONNECTION) SIN ESCALA

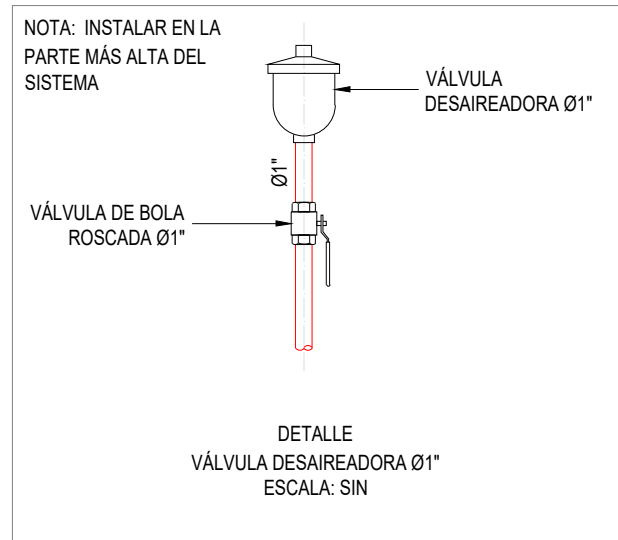

DETALLE VÁLVULA DESAIREADORA Ø1" ESCALA: SIN

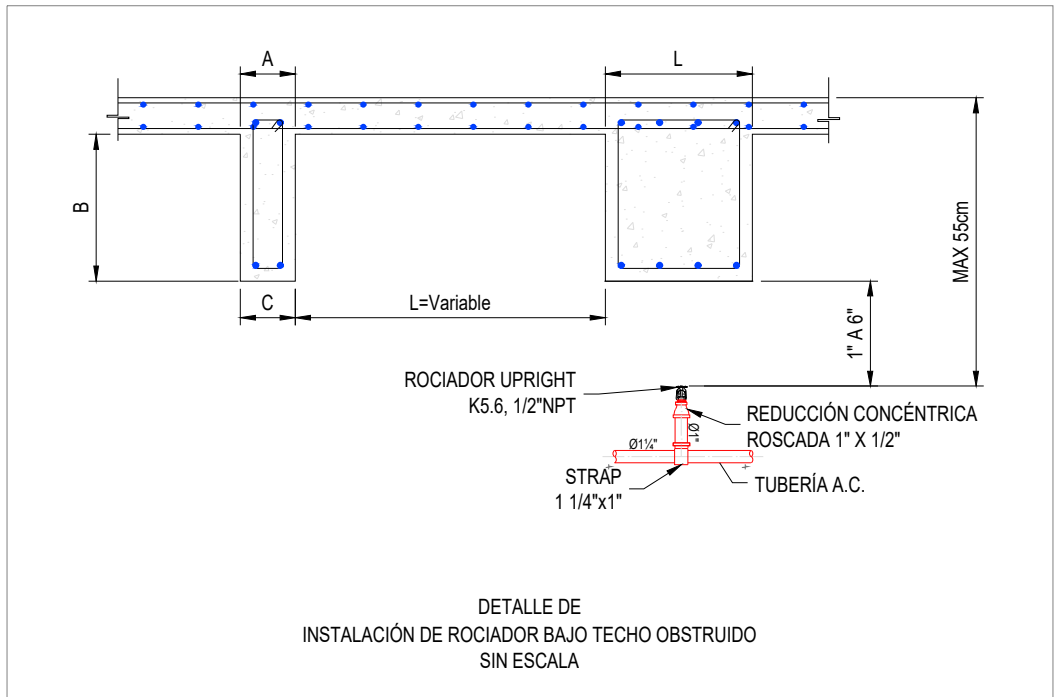

DETALLE DE INSTALACIÓN DE ROCIADOR BAJO TECHO OBSTRUIDO SIN ESCALA


REGISTRO DE MODIFICACIONES		
MODIF.	FECHA	DESCRIPCIÓN
1	--	----
2	--	----
3	--	----
4	--	----

REGISTRO DE REVISIONES		
REV.	FECHA	EMITIDO PARA:
0	24-06-2024	ACTUALIZACION
1	18-02-2025	ACTUALIZACION
2	--	----
3	--	----
4	--	----
5	--	----
6	--	----

CARACTERÍSTICAS ROCIADORES				
ORIENTACIÓN	K	ROSCA	TEMPERATURA RESPUESTA	COBERTURA
UPRIGHT	8	3/4"	68°C	RAPIDA ESTANDAR

CARACTERÍSTICAS ROCIADORES				
ORIENTACIÓN	K	ROSCA	TEMPERATURA RESPUESTA	COBERTURA
PENDENT	8	3/4"	68°C	RAPIDA ESTANDAR

CONVENCIONES	
	TUBERÍA EXPUESTA
	TUBERÍA ENTERRADA
	TUBERÍA POR CÁRCAMO
	TUBERÍA CPVC
	UNIÓN RANURADA
	CODO 90° RANURADO
	TEE RANURADA
	HIDRANTE CONTRA INCENDIO
	ESTACION DE MANGUERA SISTEMA HUMEDO
	RISER (SISTEMA CONTROLADOR)
	SIAMESA CONEXION PARA BOMBEROS 4"x2 1/2"x2 1/2"
	NODO HIDRAULICO
	ÁREA DE DISEÑO
	SOPORTE COLGANTE
	SOPORTE SISMICO CUATRO VÍAS
	SOPORTE SISMO RESISTENTE LONGITUDINAL
	SOPORTE SISMO RESISTENTE LATERAL
	BLOQUE DE EMPUJE
	VÁLVULA DE INSPECCIÓN, PRUEBA Y DRENAJE
	VÁLVULA DESAIREADORA
	FUTURA CONEXIÓN
	UNIÓN SISMICA
	ESTACION DE MANGUERA CLASE II

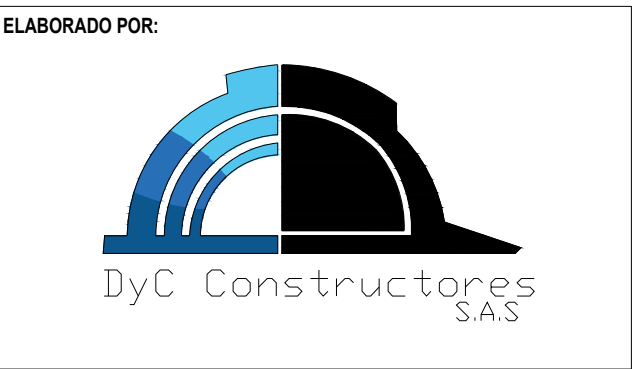

ELABORADO POR:	
AYURA MOTORS ETAPA 3	
ENIGADO-ANTIOQUIA	
PROYECTO:	
SISTEMA DE EXTINCIÓN DE INCENDIOS	
CONTIENE:	
ROCIADORES PISO 9 Y CUBIERTA	
ELABORÓ:	DAVID ORTIZ
REVISÓ:	DAVID ORTIZ
MODELO:	01-03-2024
FECHA:	UNIDADES: Metros
VERSIÓN:	04
VERS. MOD:	04
FORMATO:	A1
PROYECTO No:	GL 706
PLANO No:	PLANO 7 de 12
NOTAS:	
- LAS LONGITUDES SE INDICAN EN METROS Y LOS DIÁMETROS EN PULGADAS	
- ESTE DOCUMENTO CORRESPONDE A UN PLANO DE DISEÑO. LAS DIMENSIONES INDICADAS DEBEN SER VERIFICADAS EN OBRA.	