



UNION DE SEPARACION SISMICA DE 8" CRUZADA POR TUBERIA DE 84" (PARA OTRAS DISTANCIAS DE SEPARACION Y DIAMETROS DE TUBERIA LONGITUDES Y DISTANCIAS DEBEN SER MODIFICADAS PROPORCIONALMENTE).

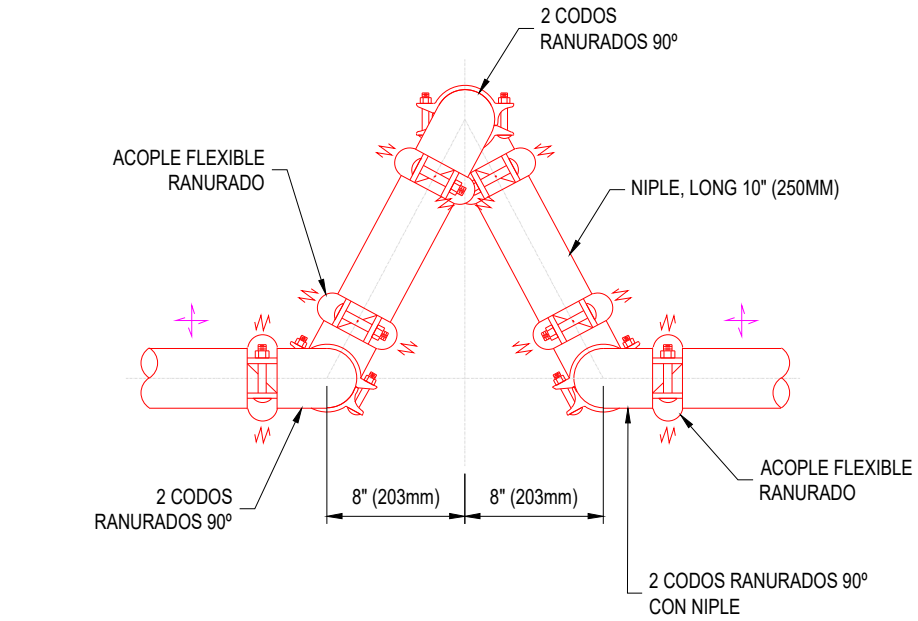


VISTA EN PLANTA
VISTA EN ELEVACION

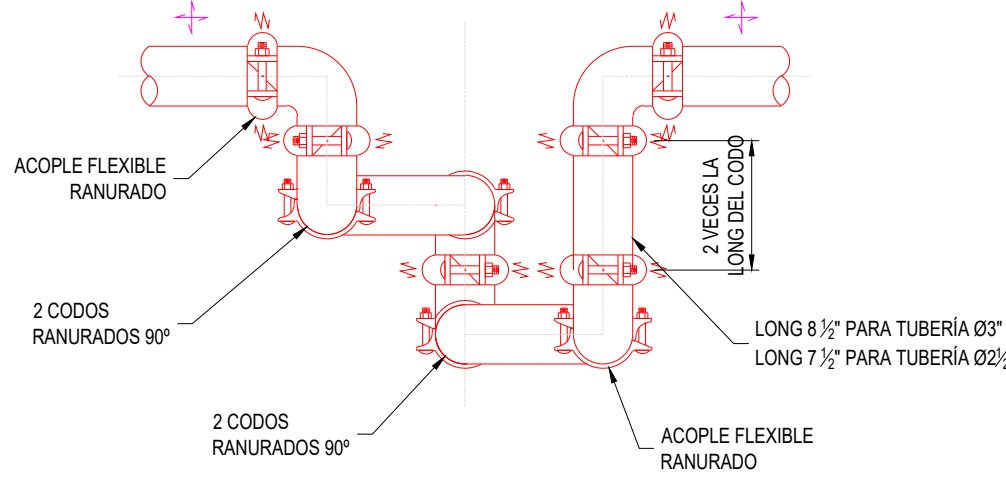

DETALLE
UNION DE SEPARACION SISMO RESISTENTE
SIN ESCALA

1 VISTA EN PLANTA RED GENERAL PISO 2

ESCALA 1:100

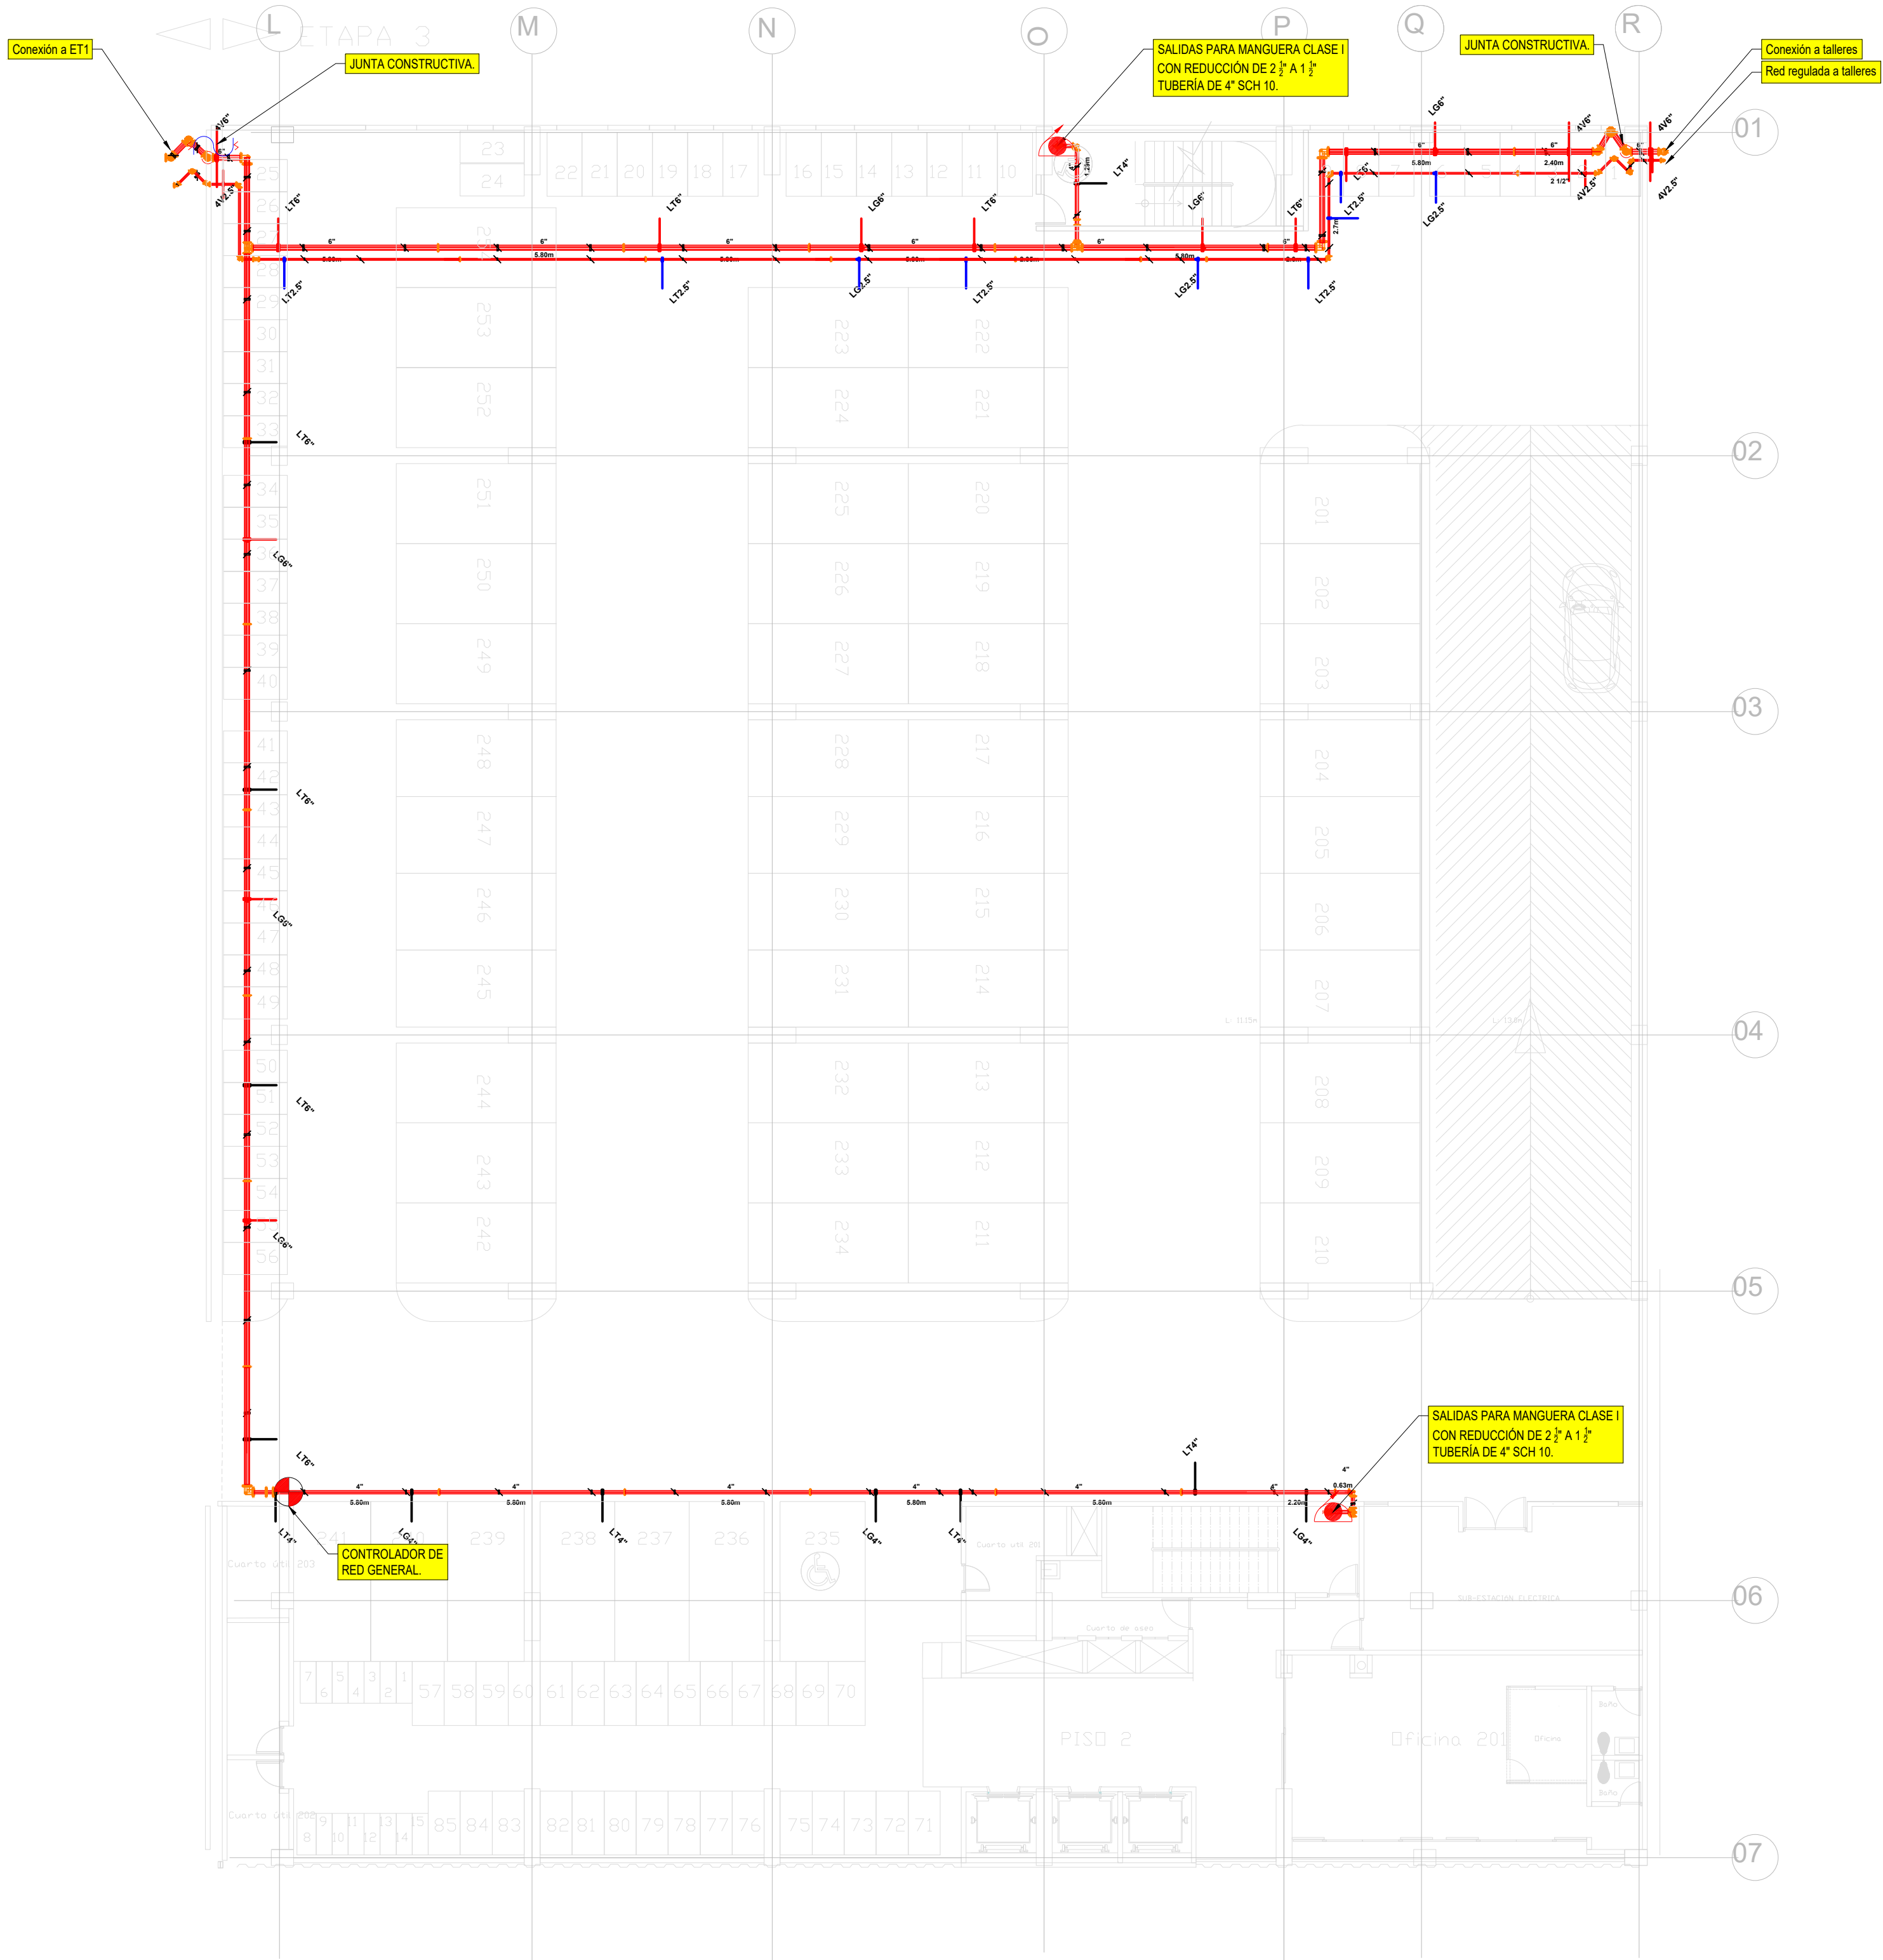

REGISTRO DE MODIFICACIONES

MODIF.	FECHA	DESCRIPCION
1	--	----
2	--	----
3	--	----
4	--	----


REGISTRO DE REVISIONES

REV.	FECHA	EMITIDO PARA:
0	24-06-2024	ACTUALIZACION
1	18-02-2025	ACTUALIZACION
2	--	----
3	--	----
4	--	----
5	--	----
6	--	----

CONVENCIONES

	TUBERIA EXPUESTA
	TUBERIA ENTERRADA
	TUBERIA POR CARCAMIO
	TUBERIA CPVC
	UNION RANURADA
	CODO 90° RANURADO
	TEE RANURADA
	HIDRANTE CONTRA INCENDIO
	ESTACION DE MANGUERA SISTEMA HUMEDO
	RISER (SISTEMA CONTROLADOR)
	SIAMESA CONEXION PARA BOMBEROS 4"x2 1/2"x2 1/2"
	NODO HIDRAULICO
	AREA DE DISEÑO
	SOPORTE COLGANTE
	SOPORTE SISMICO CUATRO VIAS
	SOPORTE SISMO RESISTENTE LONGITUDINAL
	SOPORTE SISMO RESISTENTE LATERAL
	BLOQUE DE EMPUJE
	VÁLVULA DE INSPECCIÓN, PRUEBA Y DRENAJE
	VÁLVULA DESAIREADORA
	FUTURA CONEXIÓN
	UNIÓN SISMICA
	ESTACION DE MANGUERA CLASE II

ELABORADO POR:

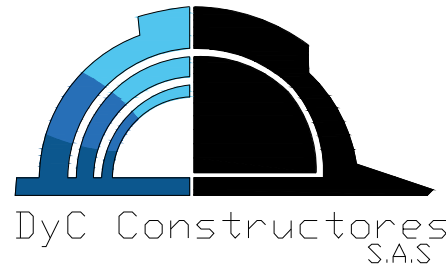

ELABORADO PARA:

AYURA MOTORS ETAPA 3

ENVIADO-AÑIOQUIA

PROYECTO:

SISTEMA DE EXTINCION DE INCENDIOS

CONTIENE:

RED GENERAL
PISO 2

ELABORÓ:

REVISÓ:

MODELO:

UNIDADES:

FECHA:

14-11-2025

ESCALA:

INDICADAS

VERSIÓN:

05

VERS. MOD:

05

FORMATO:

A1

PROYECTO No:


GL 706

PLANO No.

PLANO 8 de 12

NOTAS:

- LAS LONGITUDES SE INDICAN EN METROS Y LOS DIAMETROS EN PULGADAS
- ESTE DOCUMENTO CORRESPONDE A UN PLANO DE DISEÑO, LAS DIMENSIONES INDICADAS DEBEN SER VERIFICADAS EN OBRA.

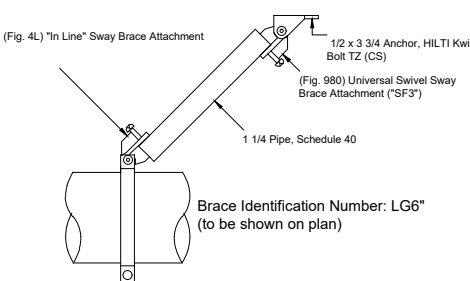


Sway Brace Zone Legend

Diameter	Description	Unit Quantity	Quantity	Unit Weight	Cp =	Net Weight
6	Pipe, Schedule 40	(2)5.80m	11.60m	47.16kg	0.5	273.53kg
				Total Net Weight		273.53kg
				Total Load (x 1.15)		314.56kg

Sway Brace Tag

Brace Type	Brace Pipe Size	Fastener Type	Fastener Orientation
Longitudinal	1 1/4"	Anchor, HILTI Kwik Bolt TZ (CS)	NFPA Type "A"
Brace Angle	Attached To	Fastener Size	Maximum Fastener Load
30	Normal Weight Concrete (6000psi)	1/2 x 3/4	374.44kg
Code: NFPA #13 - 2007	Table: 9.3.5.9.1	Plan ID: LG6"	Manufacturer: Tolco Inc

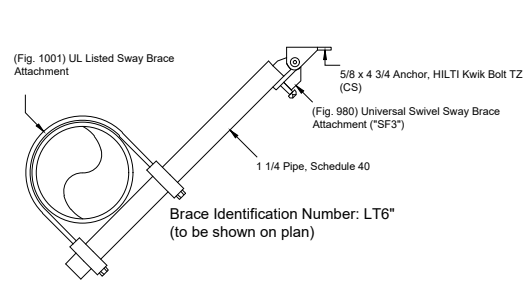


Sway Brace Zone Legend

Diameter	Description	Unit Quantity	Quantity	Unit Weight	Cp =	Net Weight
6	Pipe, Schedule 40	2.73m=(2)5.80m	14.33m	47.16kg	0.5	337.92kg
				Total Net Weight		337.92kg
				Total Load (x 1.15)		388.61kg

Sway Brace Tag

Brace Type	Brace Pipe Size	Fastener Type	Fastener Orientation
Lateral	1 1/4"	Anchor, HILTI Kwik Bolt TZ (CS)	NFPA Type "A"
Brace Angle	Attached To	Fastener Size	Maximum Fastener Load
30	Normal Weight Concrete (6000psi)	5/8 x 4 3/4	731.19kg
Code: NFPA #13 - 2007	Table: 9.3.5.9.1	Plan ID: LT6"	Manufacturer: Tolco Inc

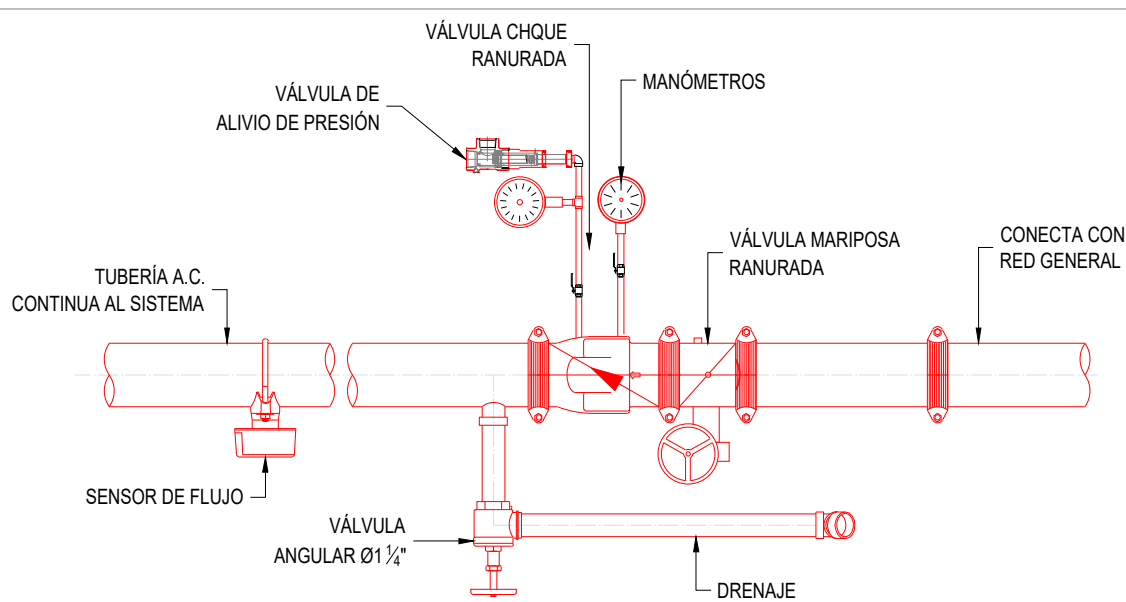

DETALLE RISER HORIZONTAL
SIN ESCALA