



ETAPA 2

ETAPA 3

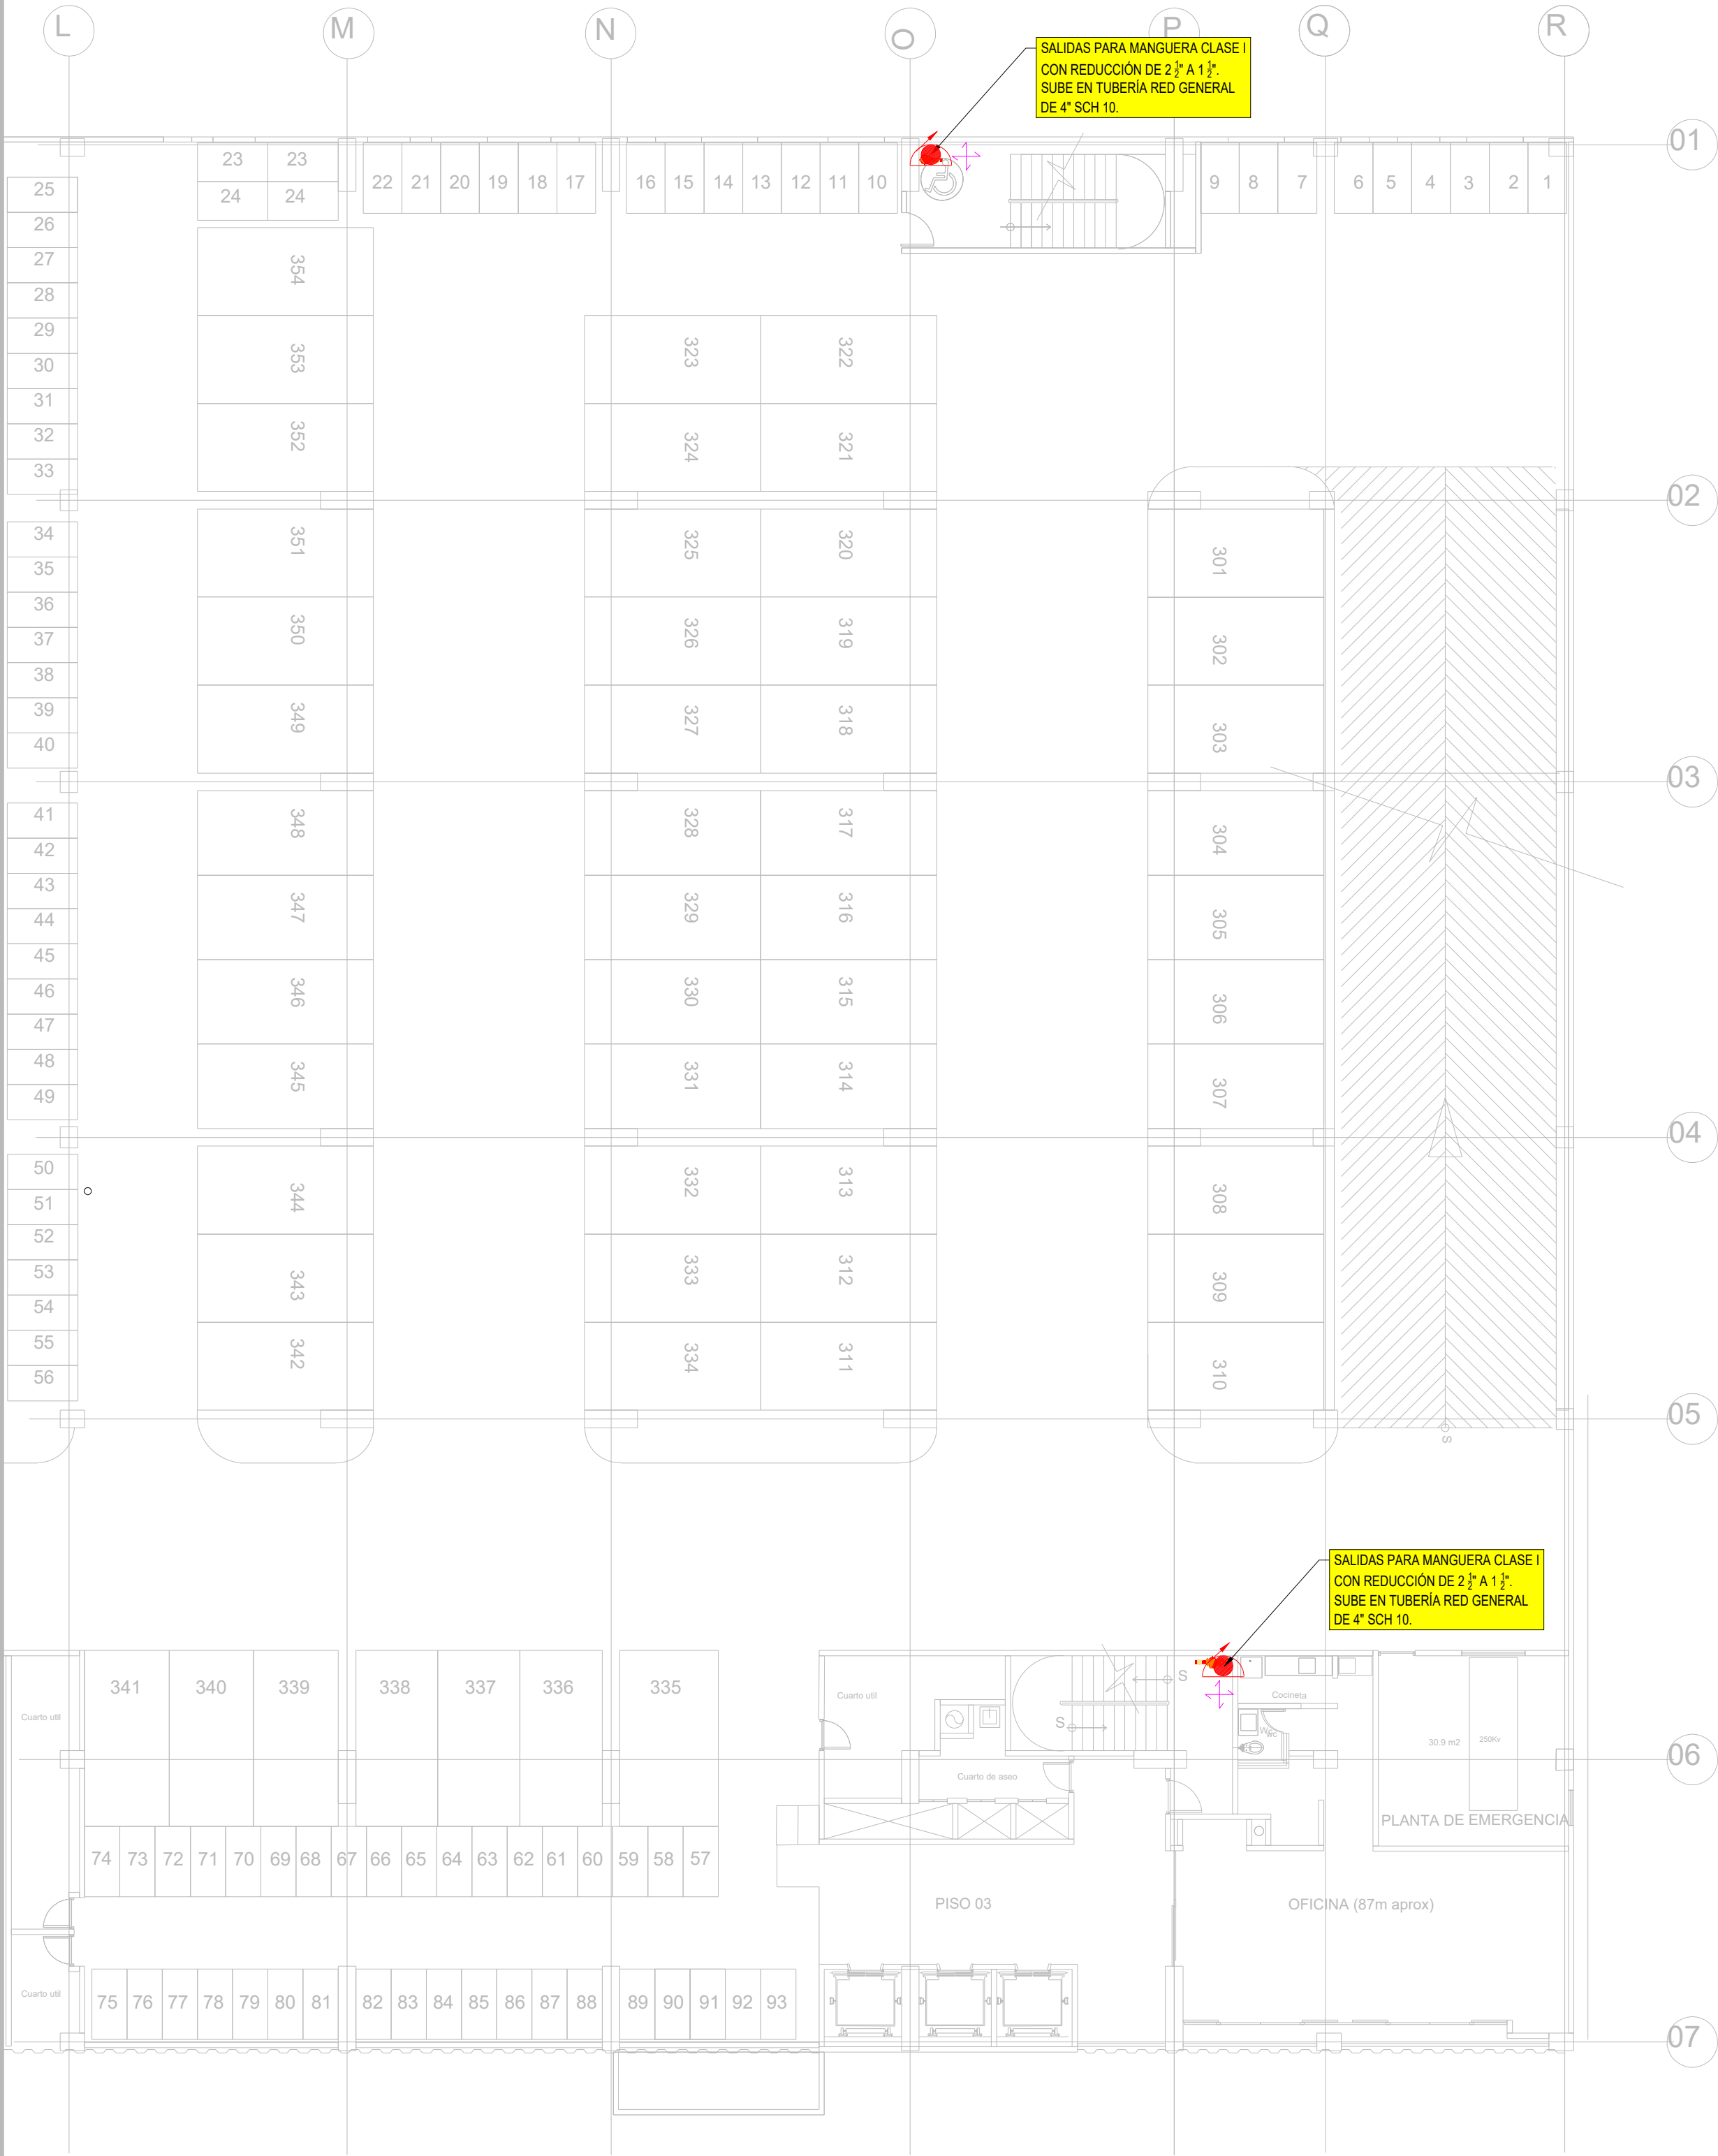


1 VISTA EN PLANTA RED GENERAL PISO 3 A 5
ESCALA 1:150

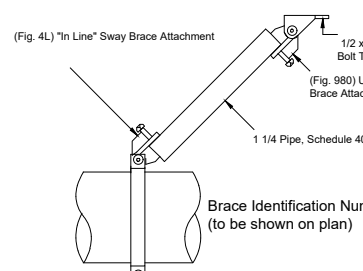


Sway Brace Zone Legend					
Diameter	Description	Unit Quantity	Quantity	Unit Weight	Cp =
6	Pipe, Schedule 40	(2)5.80m	11.60m	47.16kg	0.5
				Total Net Weight	
				273.53kg	
				Total Load (x 1.15)	
				314.55kg	

Sway Brace Tag			
Brace Type	Brace Pipe Size	Fastener Type	Fastener Orientation
Longitudinal	1 1/4"	Anchor, HLT Kwik Bolt TZ (CS)	NFPA Type "A"
Brace Angle	Attached To	Fastener Size	Maximum Fastener Load
30	Normal Weight Concrete (6000psi)	1/2 x 3/4	374.44kg
Code: NFPA #13 - 2007		Table: 9.3.5.9.1	Plan ID: LG6*
		Manufacturer: Tolco Inc	

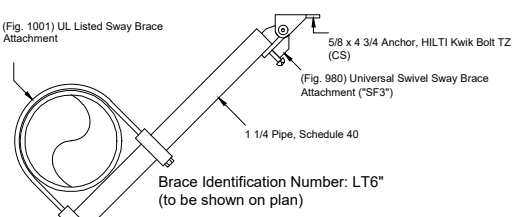

Sway Brace Zone Legend					
Diameter	Description	Unit Quantity	Quantity	Unit Weight	Cp =
6	Pipe, Schedule 40	2.73m+(2)5.80m	14.33m	47.16kg	0.5
				Total Net Weight	
				337.92kg	
				Total Load (x 1.15)	
				388.61kg	

Sway Brace Tag			
Brace Type	Brace Pipe Size	Fastener Type	Fastener Orientation
Lateral	1 1/4"	Anchor, HLT Kwik Bolt TZ (CS)	NFPA Type "A"
Brace Angle	Attached To	Fastener Size	Maximum Fastener Load
30	Normal Weight Concrete (6000psi)	5/8 x 4 3/4	731.19kg
Code: NFPA #13 - 2007		Table: 9.3.5.9.1	Plan ID: LT6*
		Manufacturer: Tolco Inc	

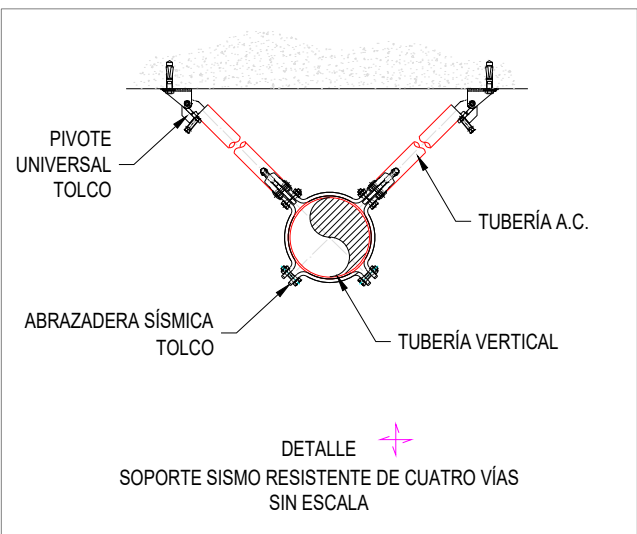

DETALLE DE LA SOPORTERIA SISMO RESISTENTE

REGISTRO DE MODIFICACIONES

MODIF.	FECHA	DESCRIPCIÓN
1	--	----
2	--	----
3	--	----
4	--	----


REGISTRO DE REVISIONES

REV.	FECHA	EMITIDO PARA:
0	24-06-2024	ACTUALIZACION
1	18-02-2025	ACTUALIZACION
2	--	----
3	--	----
4	--	----
5	--	----
6	--	----

CONVENCIONES

	TUBERÍA EXPUESTA
	TUBERÍA ENTERRADA
	TUBERÍA POR CÁRCAMO
	TUBERÍA CPVC
	UNIÓN RANURADA
	CODO 90° RANURADO
	TEE RANURADA
	HIDRANTE CONTRA INCENDIO
	ESTACION DE MANGUERA SISTEMA HUMEDO
	RISER (SISTEMA CONTROLADOR)
	SIAMESA CONEXION PARA BOMBEROS 4"x2 1/2"x2 1/2"
	NODO HIDRAULICO
	ÁREA DE DISEÑO
	SOPORTE COLGANTE
	SOPORTE SISMICO CUATRO VÍAS
	SOPORTE SISMO RESISTENTE LONGITUDINAL
	SOPORTE SISMO RESISTENTE LATERAL
	BLOQUE DE EMPUJE
	VÁLVULA DE INSPECCIÓN, PRUEBA Y DRENAJE
	VÁLVULA DESAIREADORA
	FUTURA CONEXIÓN
	UNIÓN SISMICA
	ESTACION DE MANGUERA CLASE II

ELABORADO POR:

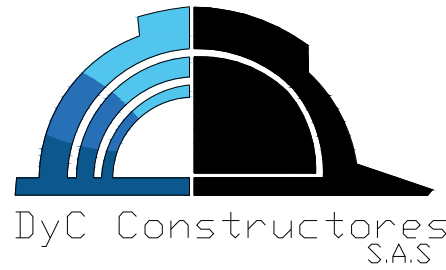

ELABORADO PARA:

AYURA MOTORS ETAPA 3

ENIGUADO-ANTIOQUIA

PROYECTO:

SISTEMA DE EXTINCIÓN DE INCENDIOS

CONTIENE:

RED GENERAL

PISO 3 A 5

ELABORÓ:

REVISÓ:

MODELO:

UNIDADES:

Metros

FECHA:

14-11-2025

VERSIÓN:

05

VERS. MOD:

05

FORMATO:


A1

PROYECTO No:

GL 706

PLANO No.

PLANO 9 de 12

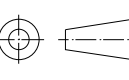

NOTAS:

- LAS LONGITUDES SE INDICAN EN METROS Y LOS DIÁMETROS EN PULGADAS
- ESTE DOCUMENTO CORRESPONDE A UN PLANO DE DISEÑO, LAS DIMENSIONES INDICADAS DEBEN SER VERIFICADAS EN OBRA